
Умовні позначення

- Газоблок
- Вентеляційні канали та отвори для підключення
- Новий розподільчий ел. щит
- Стояк каналізації, Д 110
- Конструкції із гіпсокартону
- Конструкції із вологостійкого гіпсокартону
- Радіатор опалення

Примітки:

1. Усі розміри та мітки вказані в міліметрах. Всі розміри уточнюються за фактом.
2. Всі розміри вказані по кладці та гіпсокартонним конструкцій (без урахування оздоблення).
3. За позначку 0,000 прийнято рівень чистої підлоги.
4. Обшити інсталяцію вологостійким гіпсокартоном у два шари h уточнити після вибору колекції плитки.
5. Здійснити звукоізоляцію труб стояка.
6. Всі гіпсокартонні конструкції в місцях "мокрих" зон, виконати з вологостійкого гіпсокартону (див. позначення).
7. "Мокрі" зони перед укладкою плитки обробити гідроізоляцією в 2 шари.
8. Необхідна висота дверних отворів у чистоті 2070 мм від рівня чистої підлоги.
9. Даний лист розглядати разом із листами "Обмірний" план", "План демонтажу" та розгортками стін.

* Розглянути можливість штроблення стіни замість нарощування

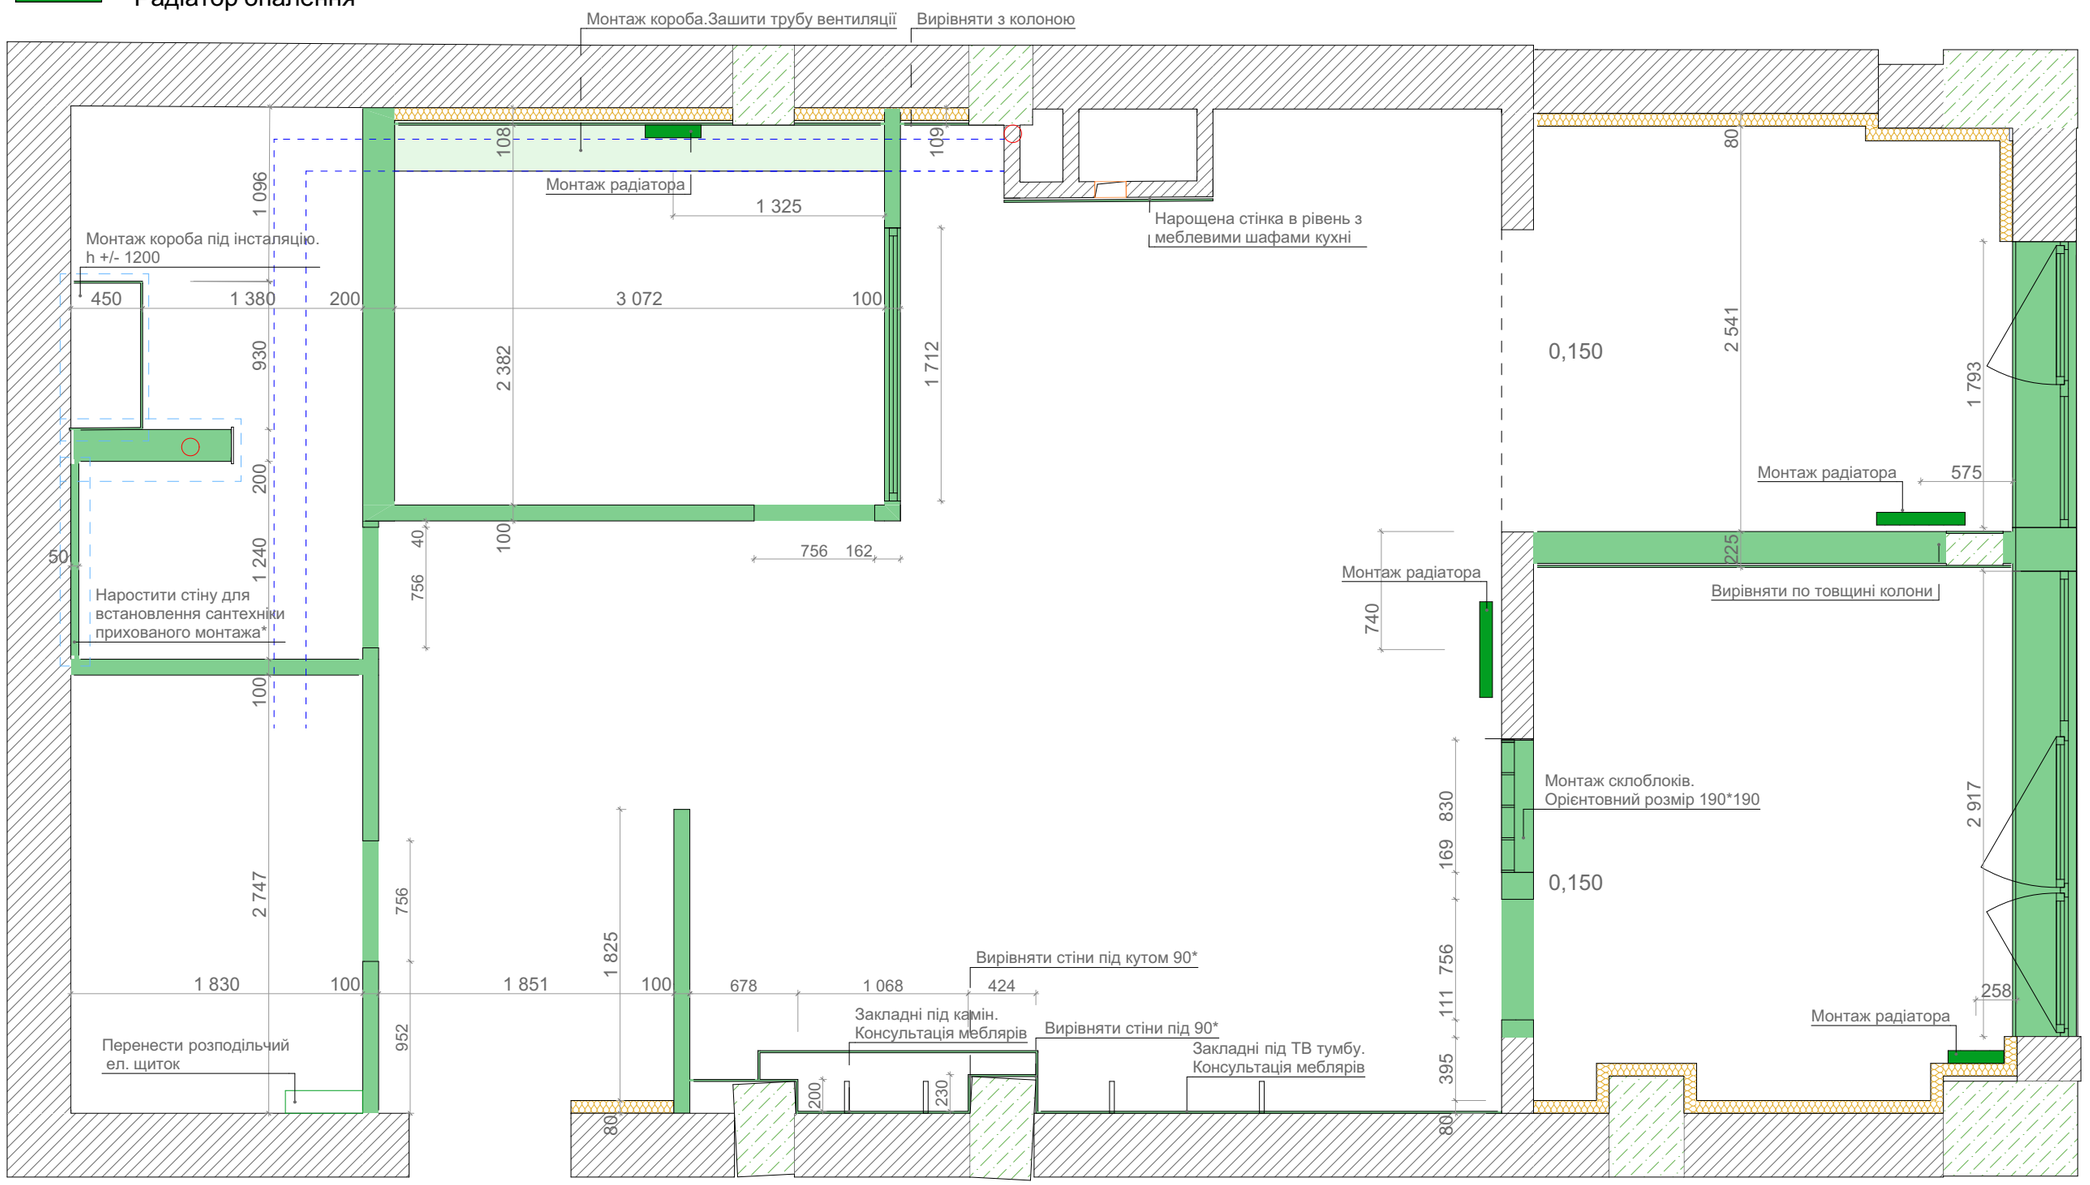

Технічний дизайн-проєкт.
Квартира 71 м²

План монтажу

Арк 06