## Умовні позначення


| | | |
|---|---|---|
| | Точковий світильник | 31 шт |
| | Люстра стельова | 3 шт |
| | Підвісні світильники | 2 шт |
| | LED стрічка | Заміри |
| | Люстра підвісна | 1 шт |

| | | |
|---|---|---|
| | Вимикач одноклавішний | 10 шт |
| | Вимикач двоклавішний | 7 шт |
| | Вимикач прохідний | 3 шт |
| | Майстер вимикач | 1 шт |
| | Регулятор теплої підлоги | 2 шт |

| | | |
|---|---|---|
| | Електровиводи | 25 шт |
| | Розподільчий ел. щит | 1 шт |
| 000 | Розмірний ряд світильників | |
| 000 | Розмірний ряд вимикачів і ел. виводів | |

Примітки:

1. Прив'язки розеток вказані по центру групи (по горизонталі та по вертикалі) та від рівня чистої підлоги.
2. Висота для кухонних розеток вказана при висоті робочої поверхні 900 мм.
4. Висоту встановлення та відстані від стін коригувати на місці в залежності від обраних моделей обладнання.

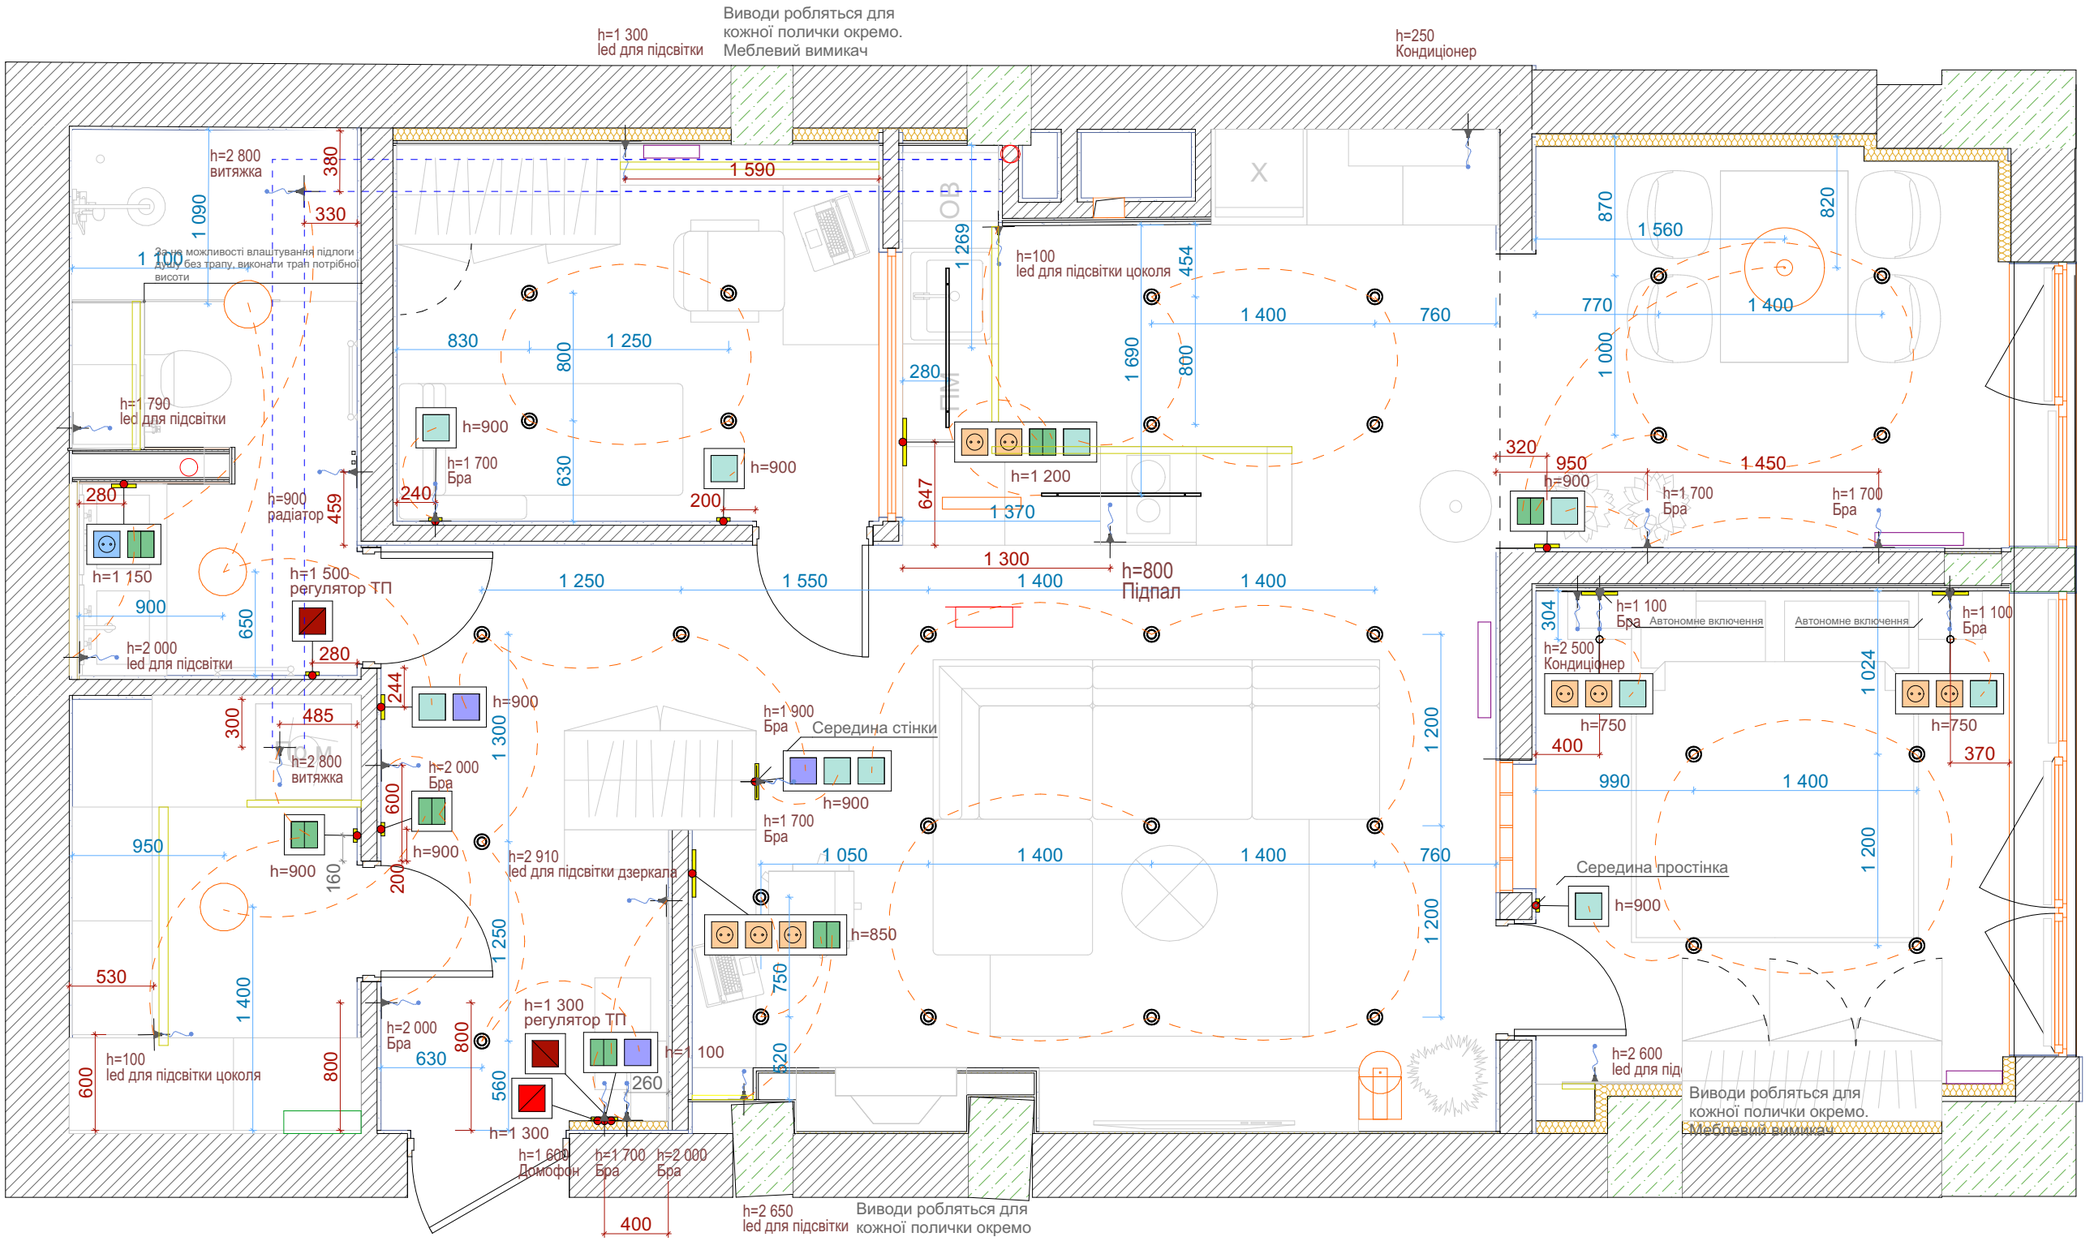


Технічний дизайн-проєкт.
Квартира 71 м$^2$

План освітлювальних приладів

| Арк | 08 |
|---|---|