
Умовні позначення

	Розетка	47 шт
	Розетка вологостійка	1 шт
	Розетка мережева	1 шт
	Кабель-канал	1 шт

Примітки:

1. Прив'язки розеток вказані по центру групи (по горизонталі та по вертикалі) та від рівня чистої підлоги.
2. Висота для кухонних розеток вказана при висоті робочої поверхні 900 мм.
4. Висоту встановлення та відстані від стін коригувати на місці в залежності від обраних моделей обладнання.

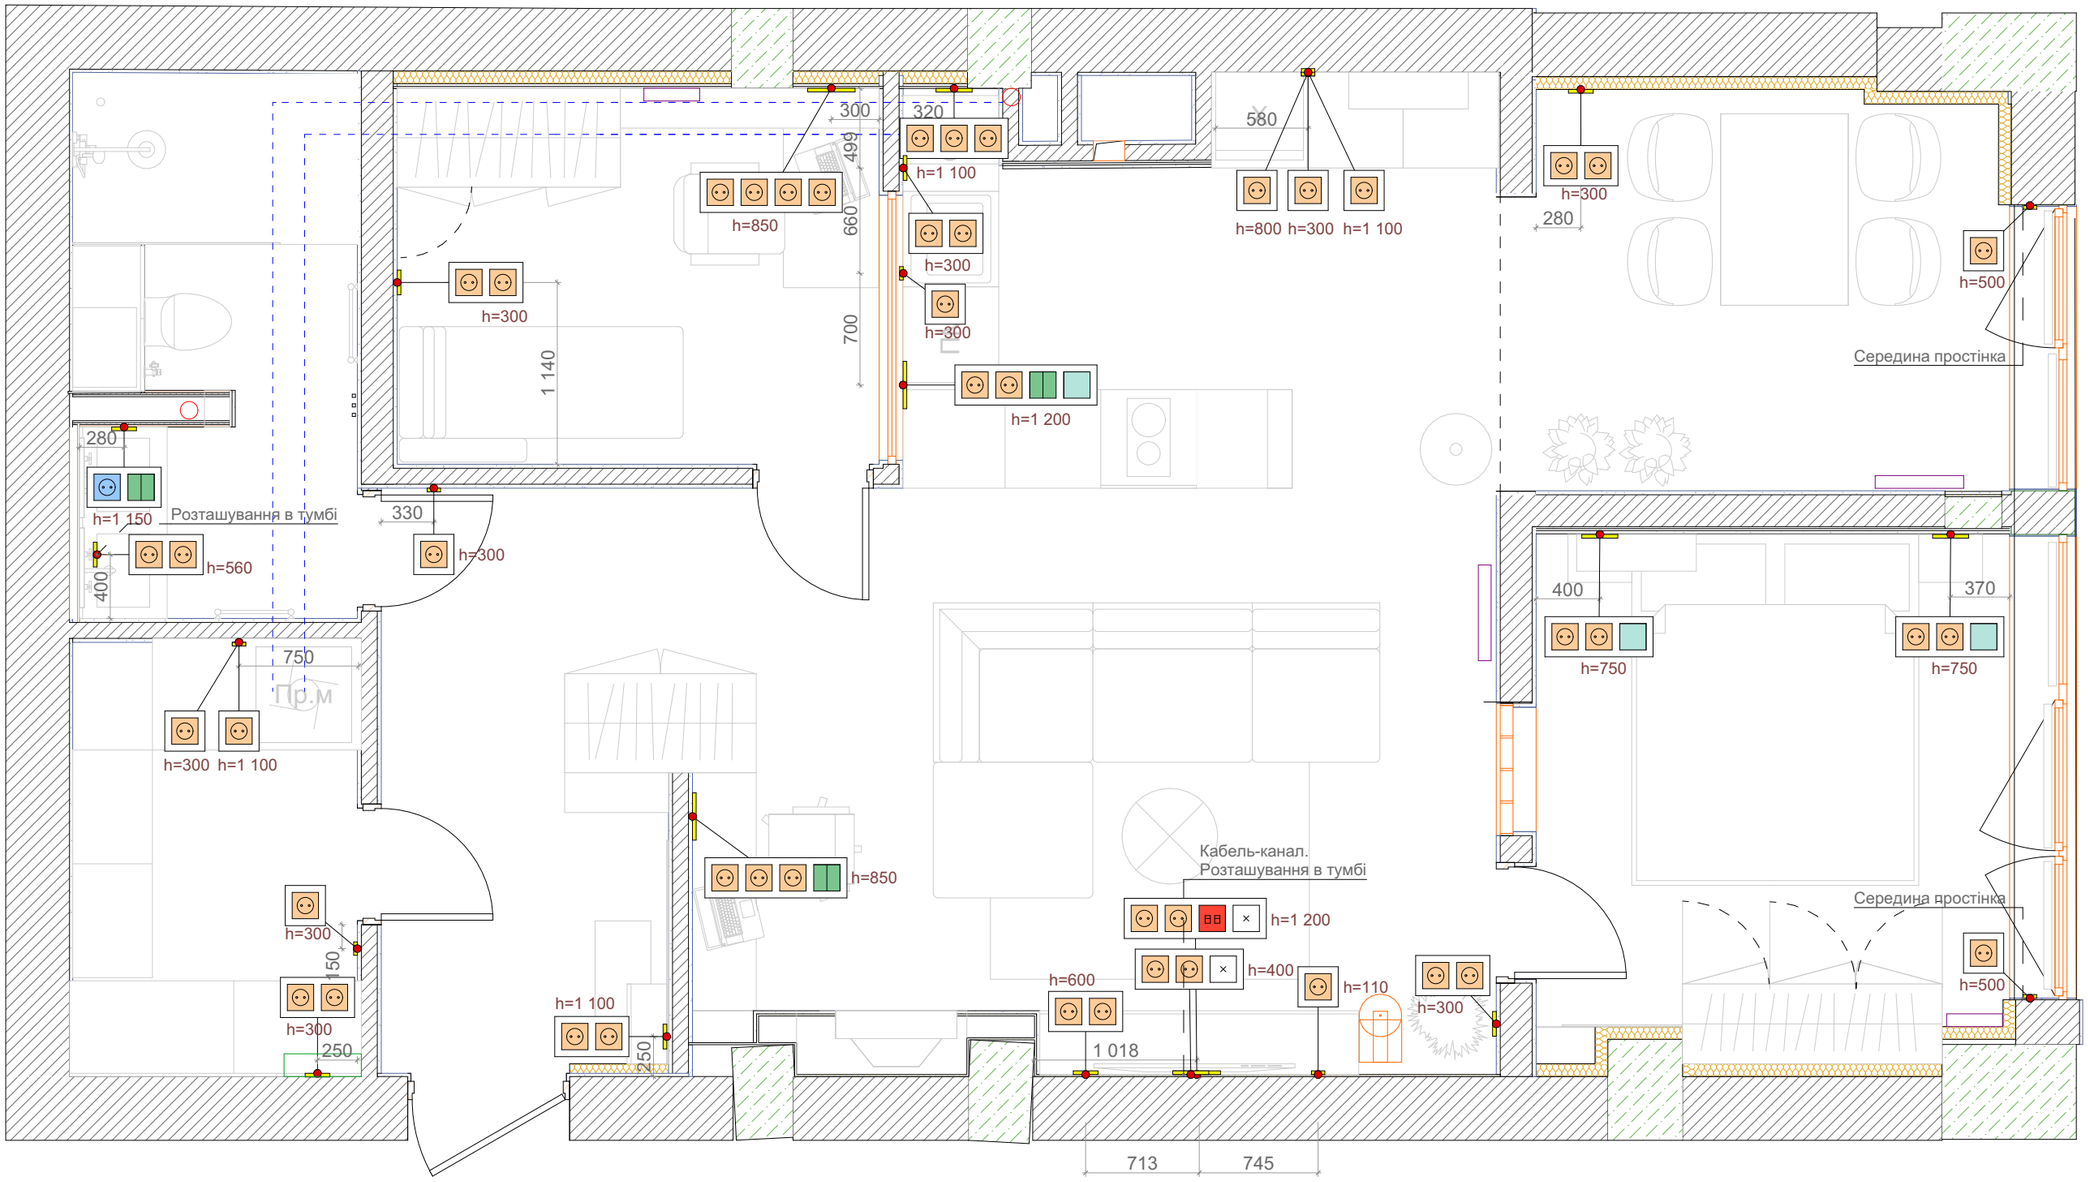

Технічний дизайн-проєкт.
Квартира 71 м²

План розміщення розеток

Арк 09