
АРХІТЕКТУРНА ДИЗАЙН-КОНЦЕПЦІЯ

квартири за адресою м. Київ, вул. Вавилових 11, секція 3, кв. 114

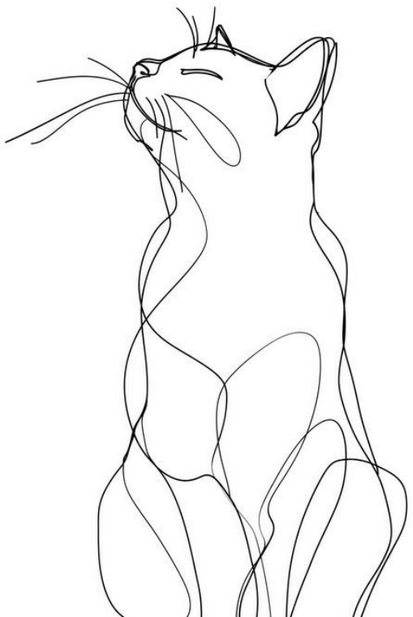

17.05.2026 architect.sofi

Зміст документу

3 Схема існуючого стану
4 Схема демонтажу стін
5 Схема монтажу стін
6 Схема після перепланування
7 Схема після перепланування з меблями
8 Схема освітлення приміщень №2 та №3
9 3д вид | кухня
10 3д вид | вітальня
11 3д вид | лоджія
12 3д вид | спальня
13 3д вид | ванна
14 3д вид | душова
15 Контакти

ПРИМІТКА

Даний документ є концептуальним матеріалом. Матеріали відображають попередню ідею та напрямок проєктного рішення і не є завершеною архітектурною або робочою документацією. Для реалізації об’єкта необхідна подальша розробка повної архітектурної концепції, проєктної та робочої документації.

До розробки концепції було проведено аналіз та дослідження об’єкта і виконано креслення **"ОБМІРНИЙ ПЛАН станом на 25.04.2026".**



СХЕМА ІСНУЮЧОГО СТАНУ
станом на 25.04.2026

квартири за адресою м. Київ, вул. Вавилових 11, секція 3, кв. 114

ПРИМІТКА

Фактична загальна **площа $S_{заг}$= 77,4 м²**

Відмітка ±0.000 приянята від рівня стяжки.

Стіни - газоблок, бетон, в приміщенні 7 оздоблення тинькуванням.
Стеля - бетонні плити перекриття.
Підлога - цемента стяжка окрім приміщень 2,3.

Більше про існучий стан дивіться крселення "ОБМІРНИЙ ПЛАН станом на 25.04.2026"

УМОВНІ ПОЗНАЧКИ

- існуючі стіни
- існуючі несучі стіни
- вхід/вихід


Пн

0 0,5 1,5 2 м

М 1: 50 А3 17.05.2026

СХЕМА ДЕМОНТАЖУ СТІН

квартири за адресою м. Київ, вул. Вавилових 11, секція 3, кв. 114

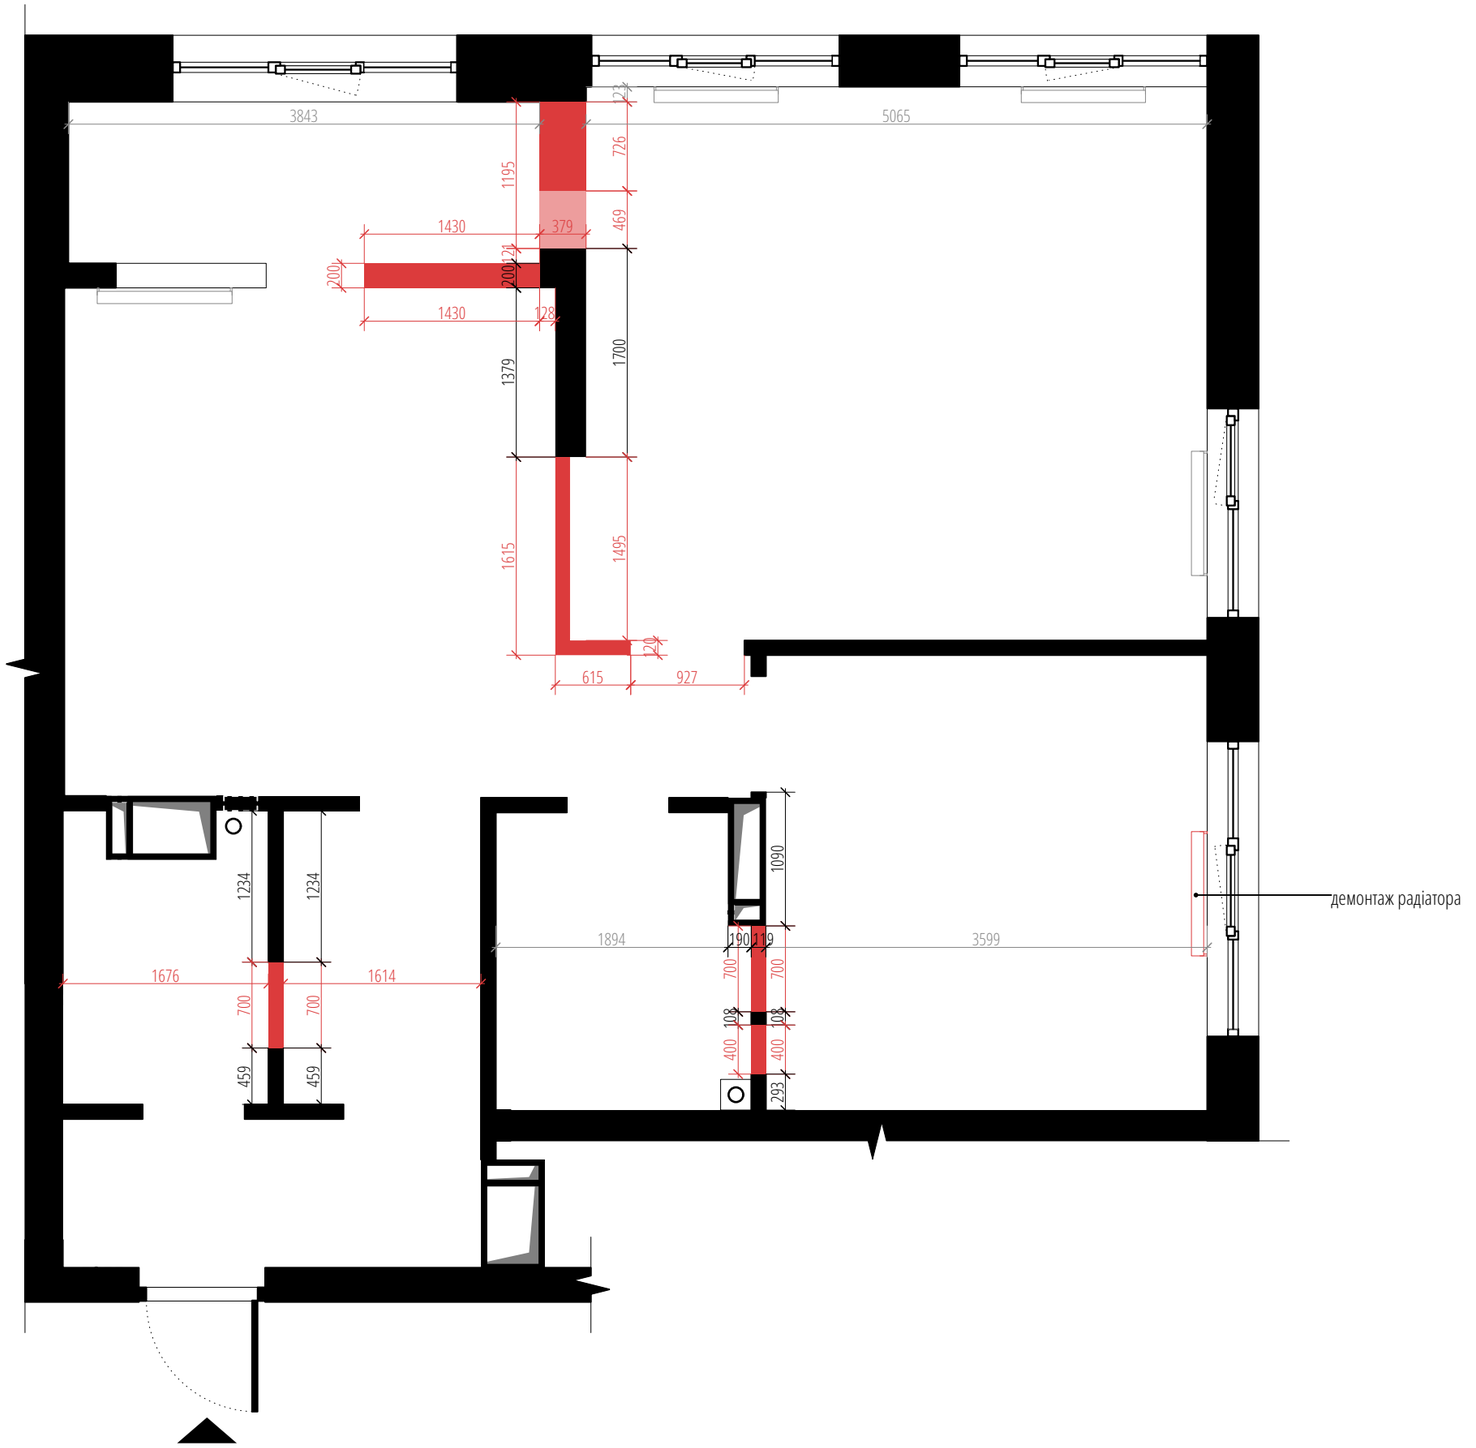

УМОВНІ ПОЗНАЧКИ

- існуючі стіни
- повністю демонтовані стіни
- частково демонтовані стіни ($h_{збереженої\ стіни\ від\ стяжки}$ = 700мм)
- демонтаж радіатора
- вхід/вихід


Пн

0 0,5 1,5 2 м

М 1: 50 А3 17.05.2026

СХЕМА МОНТАЖУ СТІН

квартири за адресою м. Київ, вул. Вавилових 11, секція 3, кв. 114

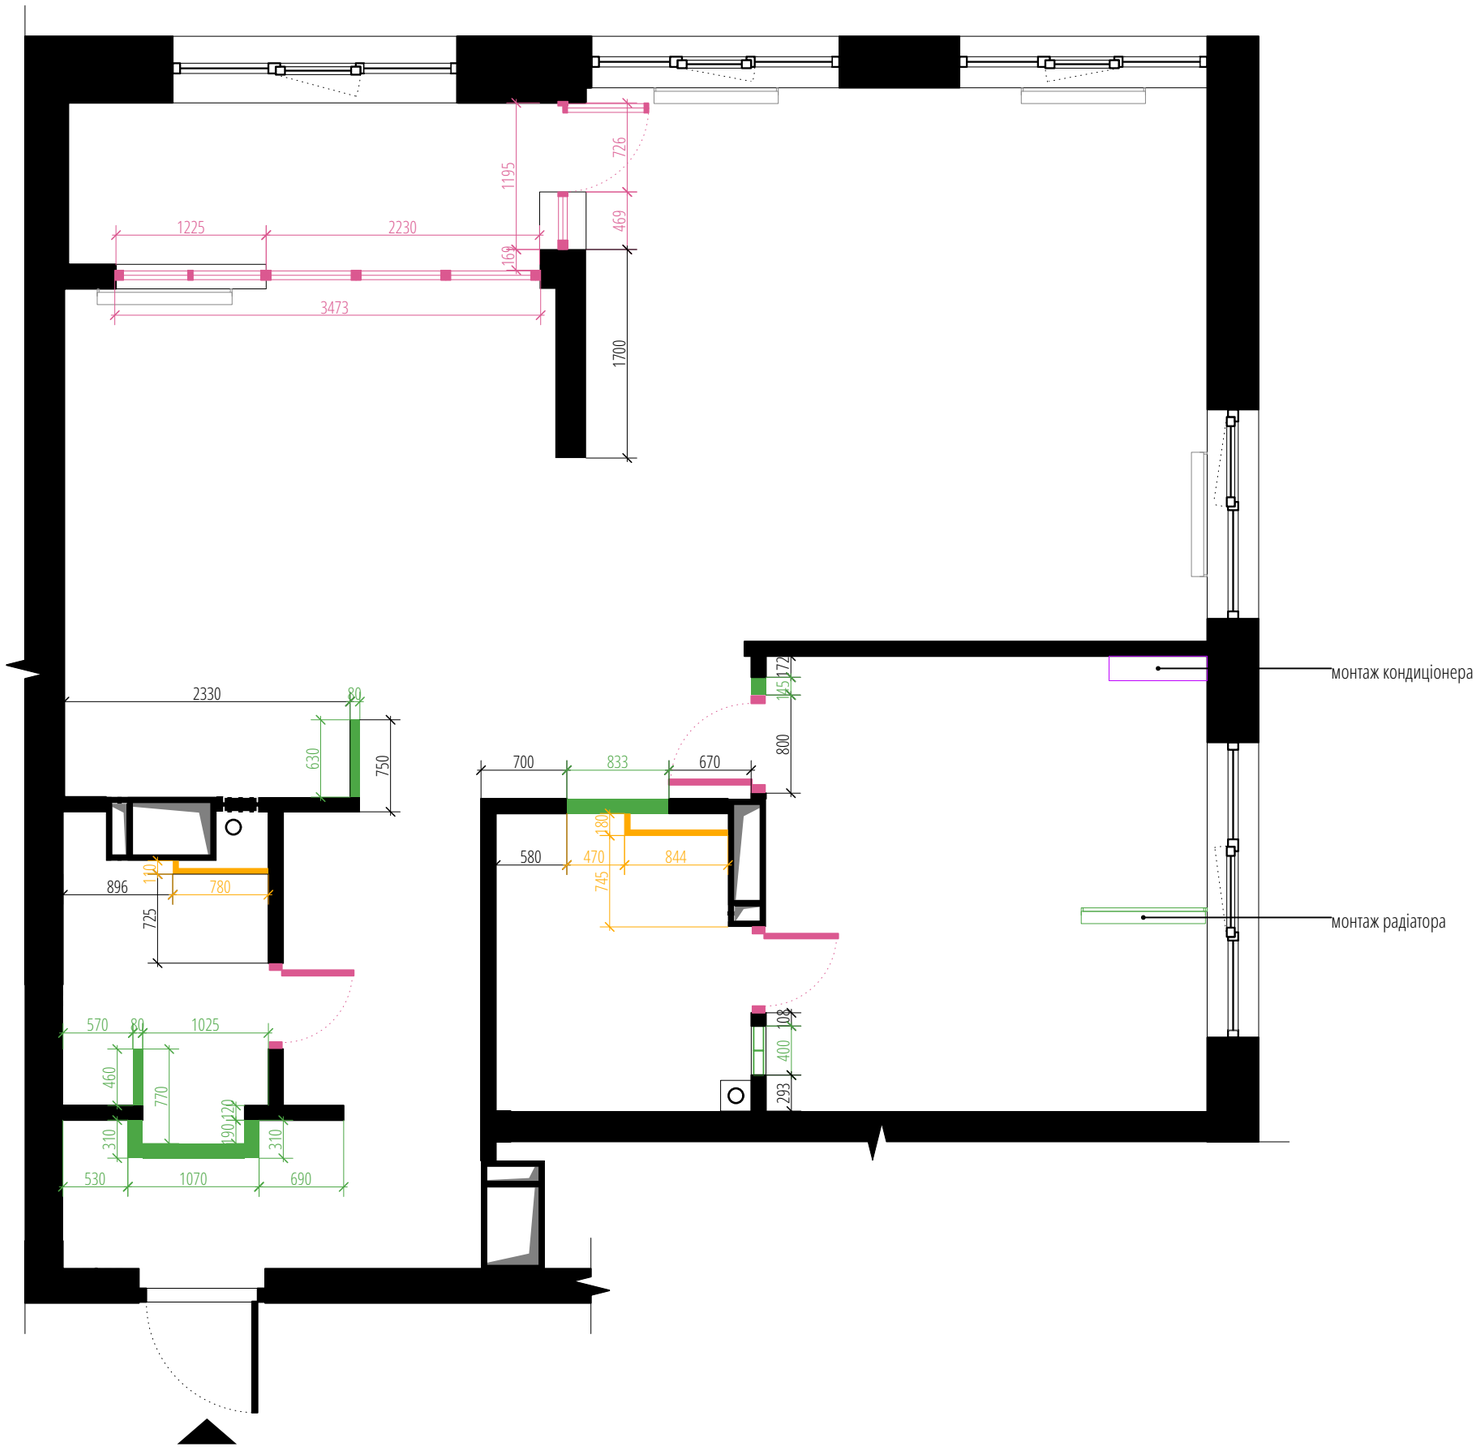

УМОВНІ ПОЗНАЧКИ

- існуючі стіни
- нові монтовані стіни
- інсталяція унітаз
- монтаж напольного радіатора (ховається в сходинку конструкції ліжка)
- монтаж кондиціонера
- монтаж дверей та скляних перегородок
- вхід/вихід


Пн

0 0,5 1,5 2 м

М 1: 50 А3 17.05.2026

СХЕМА ПІСЛЯ ПЕРЕПЛАНУВАННЯ

квартири за адресою м. Київ, вул. Вавилових 11, секція 3, кв. 114

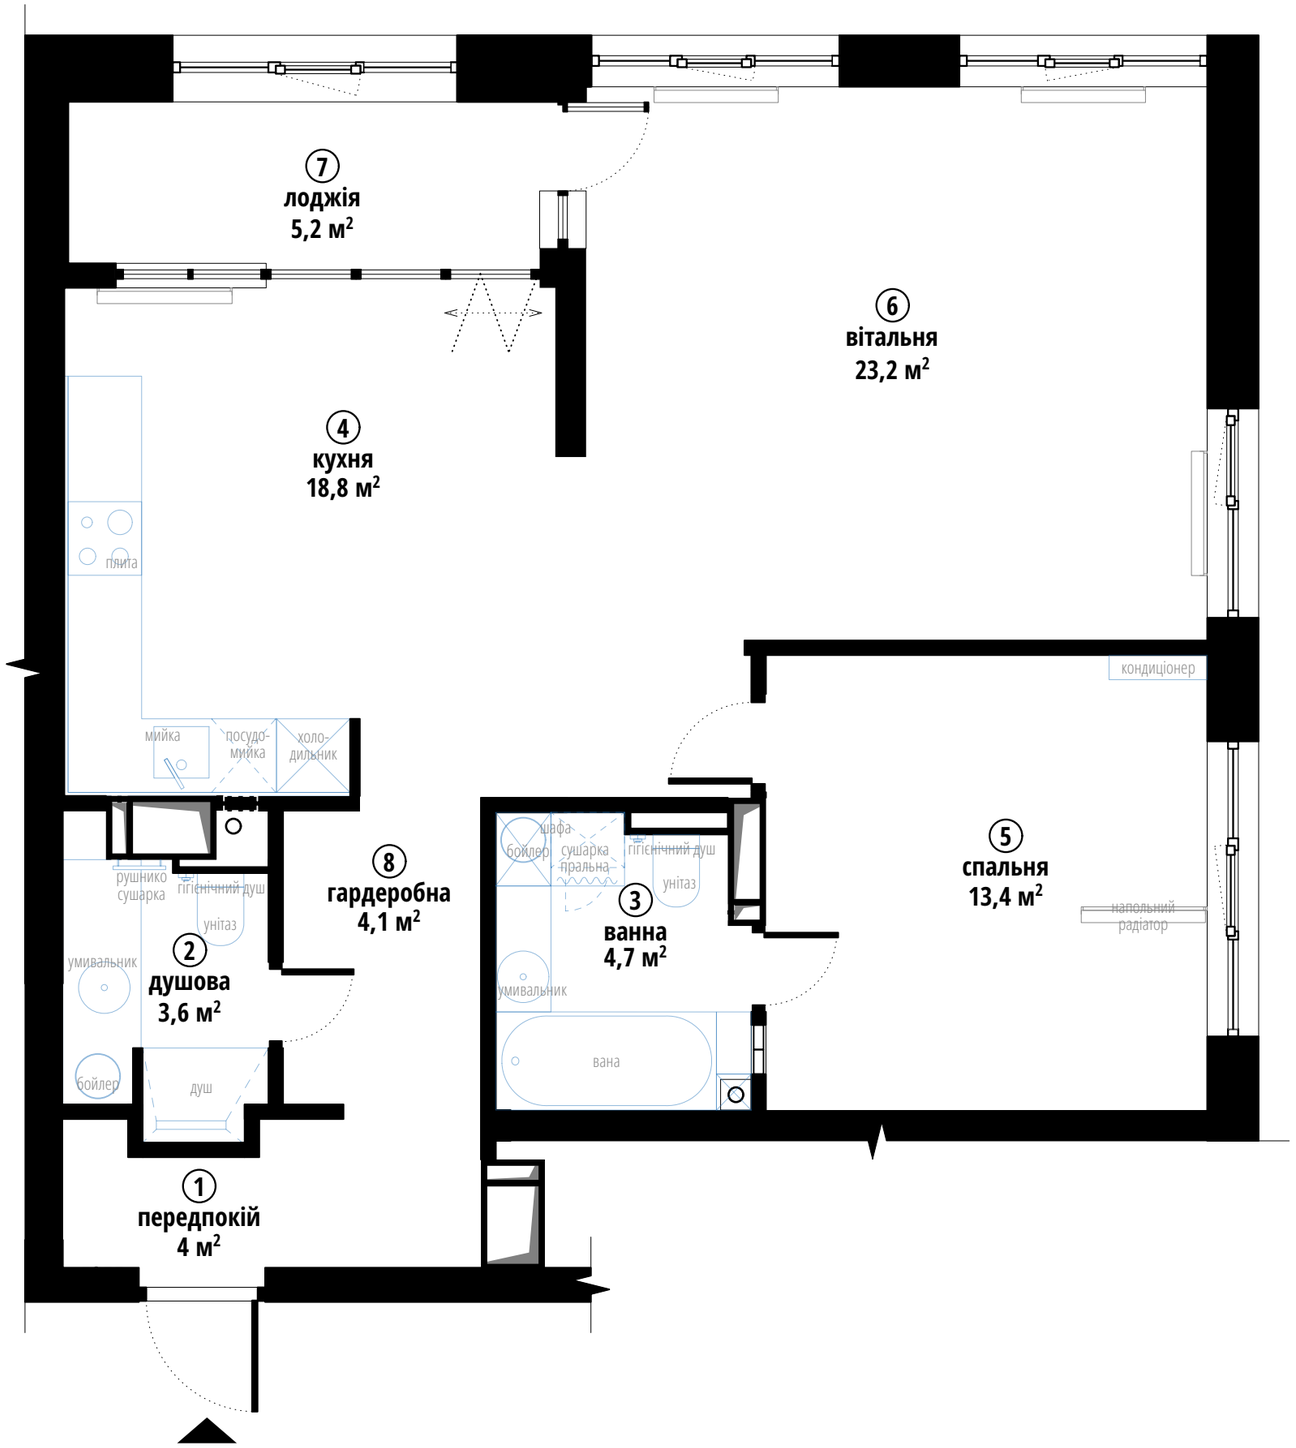


Пн

0 0,5 1,5 2 м

М 1: 50 А3 17.05.2026

СХЕМА ПІСЛЯ ПЕРЕПЛАНУВАННЯ З МЕБЛЯМИ

квартири за адресою м. Київ, вул. Вавилових 11, секція 3, кв. 114

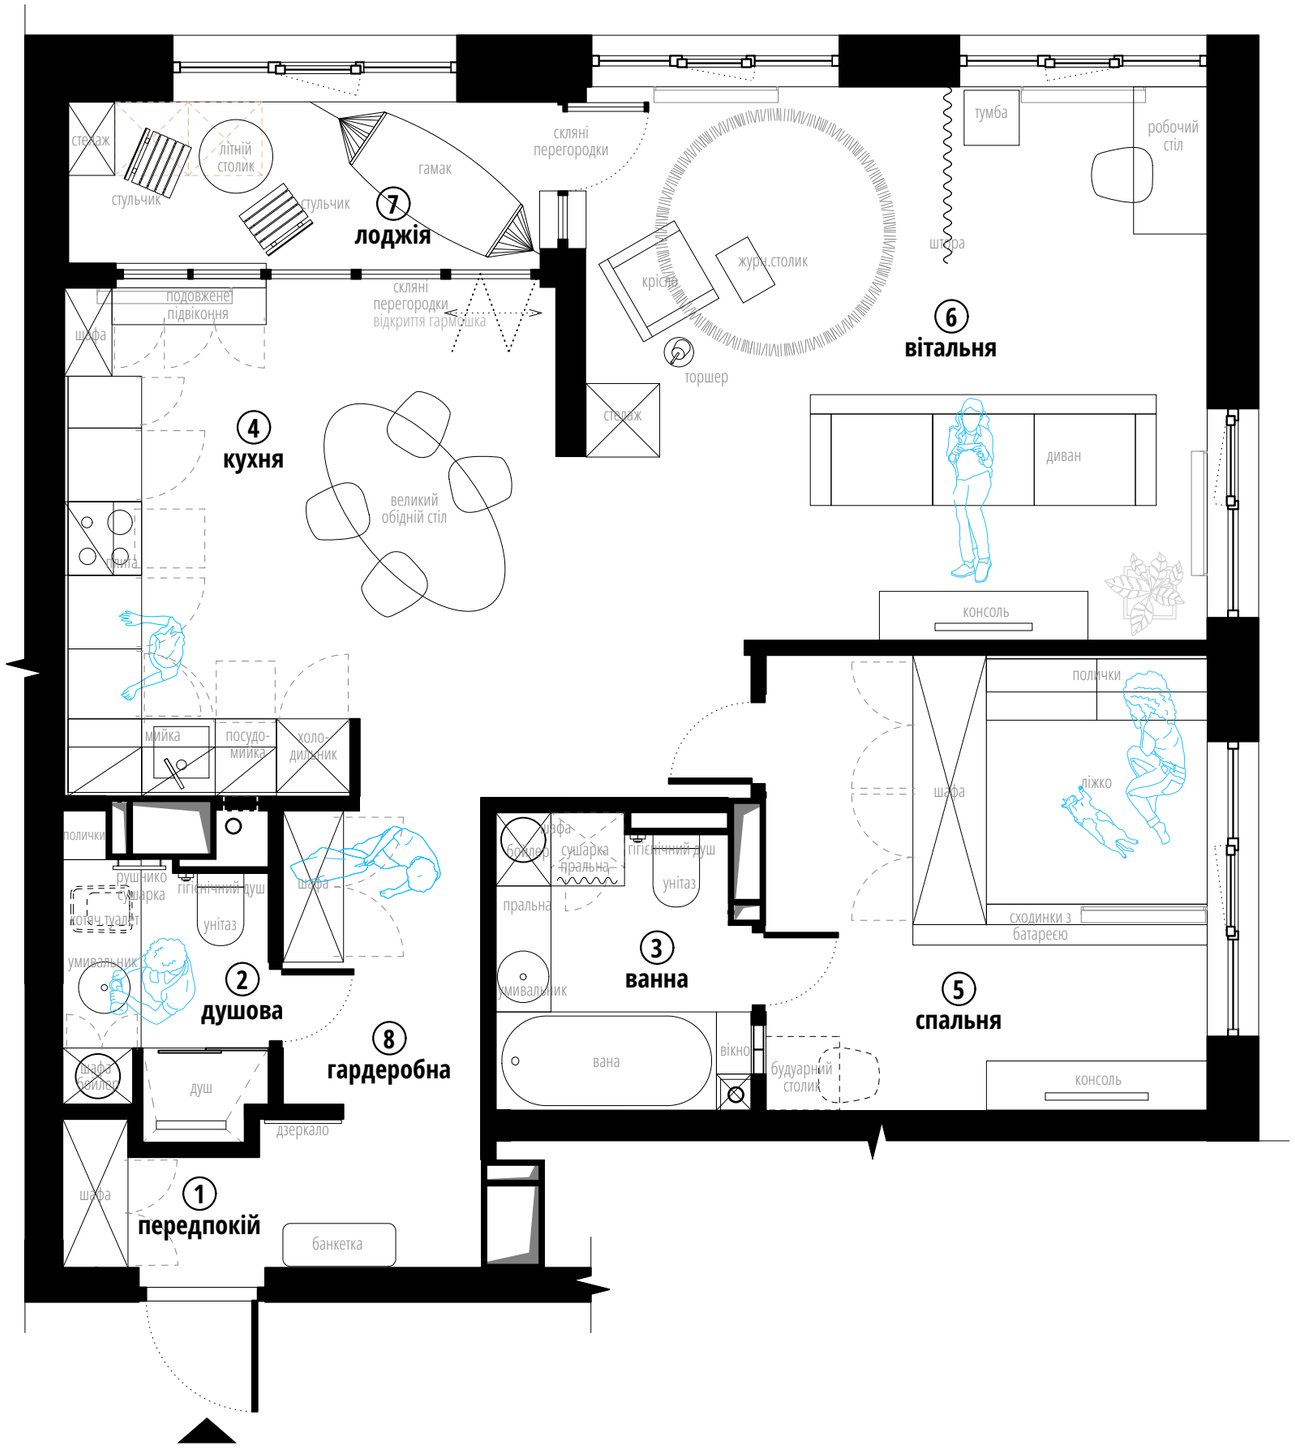

УМОВНІ ПОЗНАЧКИ

незадимлюваний простір для евакуації


Пн

0 0,5 1,5 2 м

М 1: 50 А3 17.05.2026

СХЕМА ОСВІТЛЕННЯ ПРИМІЩЕНЬ №2 та №3


квартири за адресою м. Київ, вул. Вавилових 11, секція 3, кв. 114

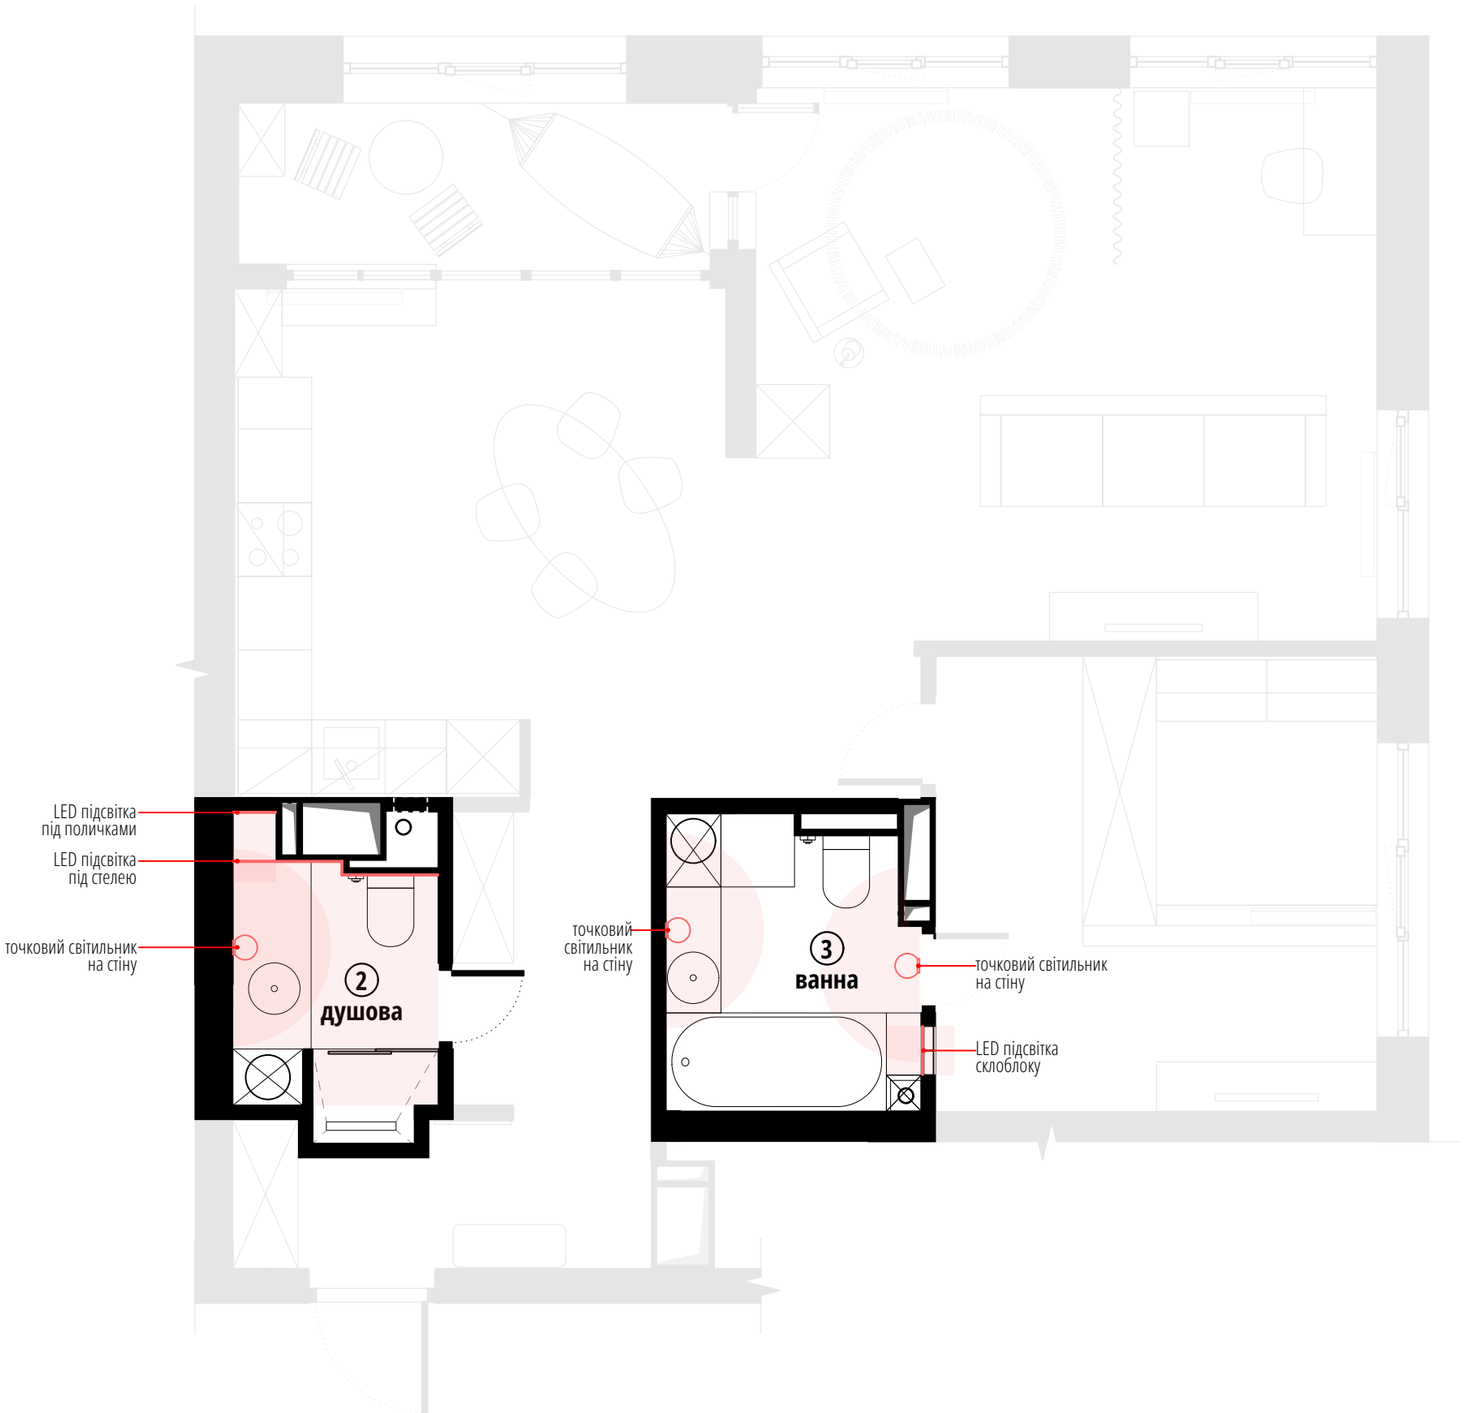

РЕФЕРЕНСИ



LED підсвітка під поличками та стелі

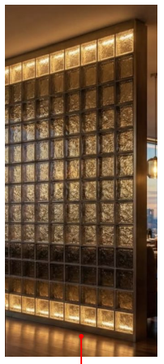

LED підсвітка склоблоку



точковий світильник на стіну

ЛЕГЕНДА

радіус освітлення
LED стічка
точковий світильник (на стіну)

Пн

0 0,5 1,5 2 м

М 1: 50 А3 17.05.2026

3д види | кухня


квартири за адресою м. Київ, вул. Вавилових 11, секція 3, кв. 114

1



2



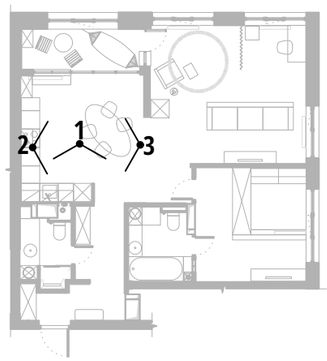


3



3д види | вітальня

квартири за адресою м. Київ, вул. Вавилових 11, секція 3, кв. 114

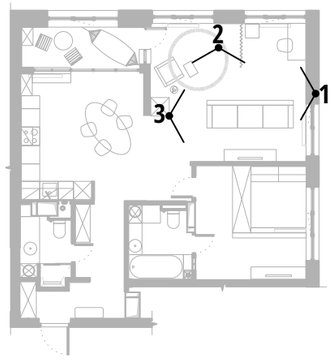

1



2



3



3д види | лоджія


квартири за адресою м. Київ, вул. Вавилових 11, секція 3, кв. 114

1



2



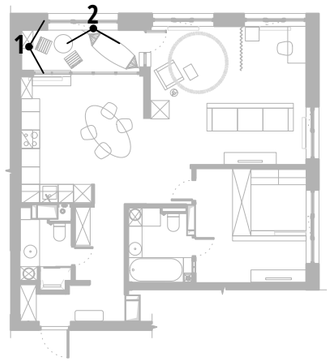


3д види | спальня


квартири за адресою м. Київ, вул. Вавилових 11, секція 3, кв. 114

1




2

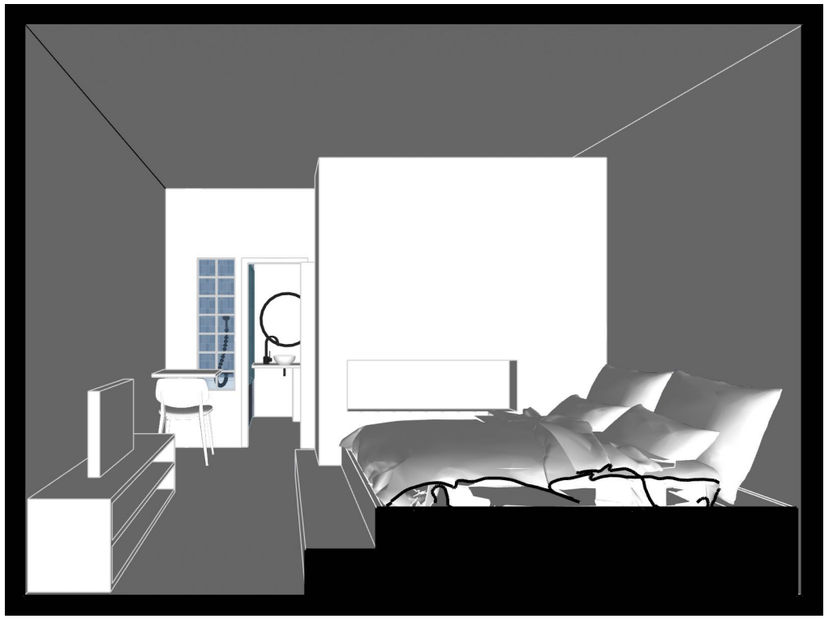

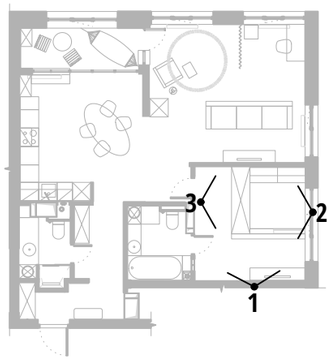

3

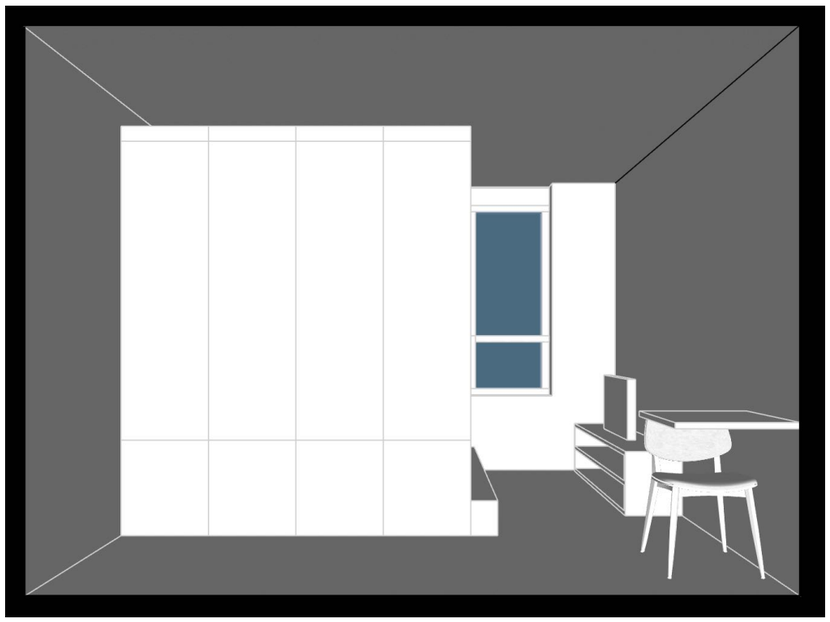

3д види | ванна


квартири за адресою м. Київ, вул. Вавилових 11, секція 3, кв. 114

1




2



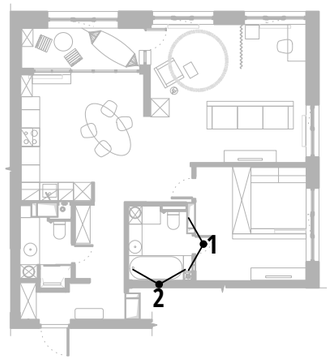

3д види | душова, гардеробна, передпокій


квартири за адресою м. Київ, вул. Вавилових 11, секція 3, кв. 114

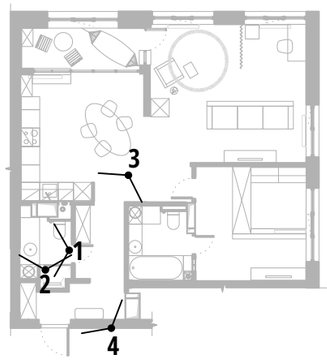


1




2

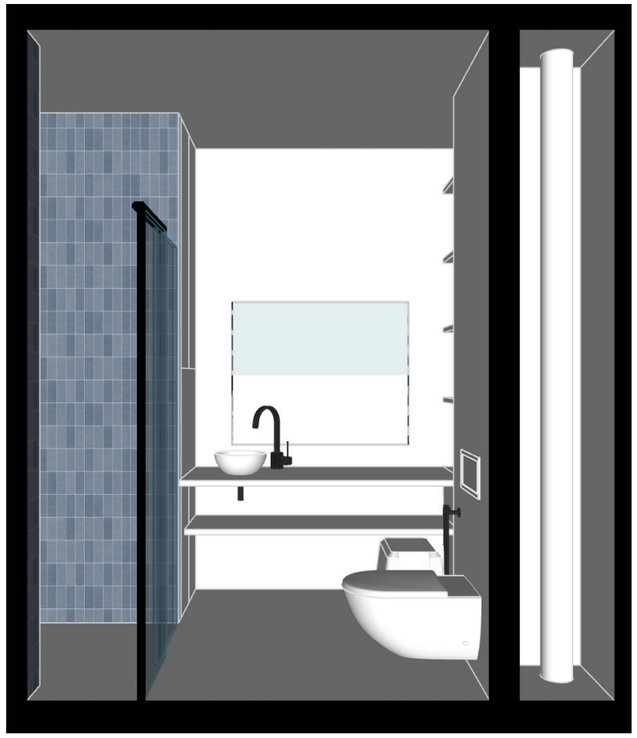

3

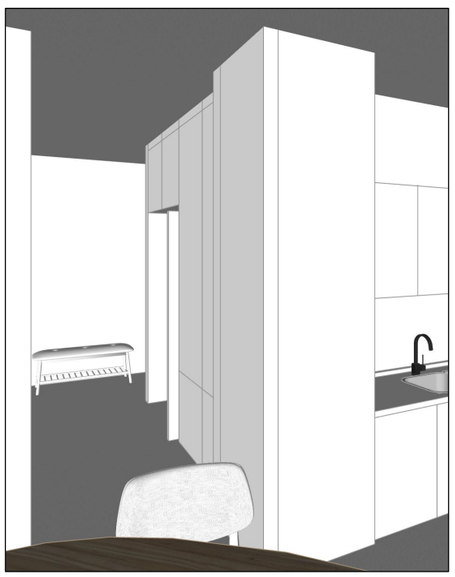

4

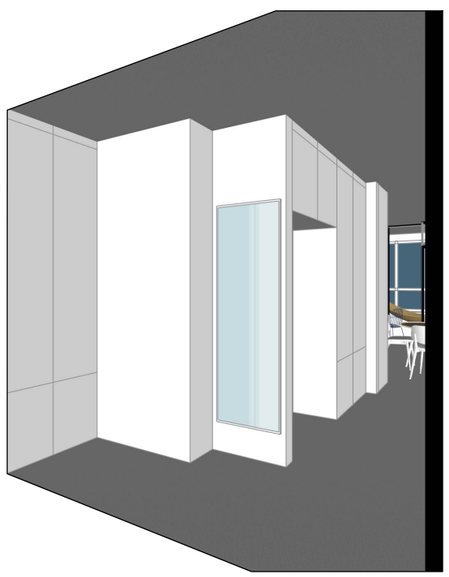

архітектурна дизайн-концепція

квартири за адресою м. Київ, вул. Вавилових 11, секція 3, кв. 114

авторка та розробниця проєкту
Софія Бондар

architect.sofi@gmail.com
+380 93 927 00 26