ВІДОМІСТЬ КРЕСЛЕНЬ

A-01 Титульний аркуш
A-02 Відомість креслень
A-03 Пояснювальна записка
A-04 Візуалізація
A-05 Візуалізація
A-06 Візуалізація
A-07 Візуалізація
A-08 Візуалізація
A-09 Візуалізація
A-10 Візуалізація
A-11 Візуалізація
A-12 Візуалізація
A-13 Візуалізація
A-14 Візуалізація
A-15 Візуалізація
A-16 План обмірів
A-17 План демонтажу
A-18 3D-схема демонтажу
A-19 План монтажу
A-20 3D-схема монтажу
A-21 План меблів
A-22 3D-схема №1
A-23 3D-схема №2
A-24 План заповнення дверних прорізів
A-25 Специфікація дверей
A-26 План опалення

ВІДОМІСТЬ КРЕСЛЕНЬ

A-27 Плани та розгортки сантехніки
A-28 План підлог
A-29 План оздоблювальних матеріалів стін
A-30 План вентиляції та кондиціонування
A-31 План стель
A-32 План розміщення освітлювальних приладів
A-33 План груп світла й вимикачів
A-34 План розеток та електровиводів
A-35 Специфікації освітлення та електрофурнітури
A-36 План розгорток
A-37 Розгортка передпокою
A-38 Розгортка кухні
A-39 3D-схема кухні
A-40 Розгортка кабінету
A-41 3D-схема кабінету
A-42 Розгортка балкону
A-43 Розгортка спальні
A-44 3D-схема спальні
A-45 Розгортка гардеробу
A-46 Розгортка санвузла
A-47 3D-схема санвузла
A-48 Специфікація меблів та сантехніки
A-49 Загальна специфікація матеріалів
A-50 Меблі на замовлення
A-51 Меблі на замовлення
A-52 Візитна картка

SMIRNOVA
INTERIOR DESIGN

Назва проєкту:	Квартира
Адреса проєкту:	вул.Вавілових 11, кв.216

Відомість креслень
A-02

ПОЯСНЮВАЛЬНА ЗАПИСКА

Даний комплект креслень розроблений для реалізації дизайн-проєкту та є робочим інструментом, що допомагає коректно втілити проєктні рішення під час ремонту.
Усі рішення базуються на принципах: — функціональності
— ергономіки
— логіки користування простором

1. Перед початком ремонтних робіт погодити перепланування (за наявності) у БТІ та отримати новий техпаспорт. 2. Виконати запуск та перевірку газового або електричного котла та газового обладнання (за наявності).

2. Основні розміри та прив'язки
Усі розміри та прив'язки, зазначені в кресленнях, виконані:
з урахуванням чистових розмірів приміщень із дотриманням стандартів ергономіки та зручності користування
У проєкті вказані:
відстані від стін, кутів та осей перегородок, прив'язки меблів, сантехнічного обладнання, розеток і вимикачів
висотні відмітки розеток, вимикачів та виводів освітлення, габарити меблів і ширина проходів.
Перед виготовленням вбудованих меблів та монтажем обладнання рекомендується виконати контрольні чистові заміри приміщення.

3. Планування та розміщення меблів
Планувальні рішення та розміщення меблів розроблені: з урахуванням сценаріїв життя ,логіки переміщення комфортних відстаней між об'єктами
Усі рішення виконані з дотриманням стандартів ергономіки та розраховані на щоденне зручне користування.

4. Освітлення та сценарії світла
Проєктом передбачені сценарії освітлення для різних задач і часу доби.
Важливо:
Для реалізації проєкту необхідно заздалегідь визначити конкретні моделі світильників, зокрема:
- тип світильників (вбудовані / накладні)
- спосіб увімкнення та вимкнення:
- керування від настінного вимикача або вимикач,
- вбудований у корпус світильника напрямок світлового потоку колірну температуру
- можливість димування
У разі, якщо настінні світильники (бра) мають вимикач на корпусі, окремий настінний вимикач для них не передбачається.

5. Електрика та обладнання
Розташування розеток, вимикачів та електровиводів виконане з урахуванням запроєктованих меблів і обладнання.
Остаточне розташування електровиводів уточнюється після вибору:
- побутової техніки
- сантехнічного обладнання
- освітлювальних приладів
- кліматичного обладнання

6. Підлоги та оздоблювальні рішення
Під час реалізації проєкту необхідно враховувати:
- товщину підлогових покриттів, підкладки, стики різних матеріалів
Рішення щодо рівнів підлоги слід погодити до початку чистових робіт, особливо в зонах дверей, вбудованих меблів і плінтусів.

7. Вентиляція та кондиціонування
Проєктні рішення з вентиляції та кондиціонування розроблені концептуально та підлягають уточненню після вибору конкретних моделей обладнання.
Під час реалізації необхідно передбачити: -прокладання трас, дренаж, доступ до ревізійних зон

8. Допуски та коригування
У процесі реалізації можливі незначні коригування проєктних рішень, пов'язані з:
- конструктивними особливостями об'єкта, інженерними обмеженнями, уточненням обладнання

Усі зміни обов'язково погоджуються з дизайнером.
9. Загальні рекомендації
Рекомендується:
дотримуватись послідовності ремонтних робіт
не розпочинати чистові етапи без узгодження інженерних рішень
у разі виникнення питань звертатися до дизайнера

ПОЯСНЮВАЛЬНА ЗАПИСКА **для будівельників**

Креслення є робочими та призначені для реалізації проєкту.

Основні положення:

- усі розміри вказані по чистовим поверхням
- прив'язки виконані від стін, кутів та осей перегородок
- розміщення меблів виконане з дотриманням норм ергономіки

Перед початком робіт:

- виконати контрольні чистові заміри
- уточнити моделі:
- світильників
- побутової техніки
- сантехнічного обладнання
- кондиціонерів


Освітлення:
- до монтажу визначити моделі світильників
- уточнити:
" тип світильників,
" спосіб увімкнення / вимкнення (від настінного вимикача або вимикач на корпусі)
" за наявності у бра вимикача на корпусі — окремий вимикач не передбачається
- сценарії освітлення реалізуються згідно з кресленнями

Електрика та інженерія:
- розташування електровиводів уточнюється після вибору обладнання
- рішення з вентиляції та кондиціонування коригуються під вибрані моделі

Важливо:

* усі відхилення від проєкту погоджуються **з дизайнером**
самовільні зміни без погодження не допускаються

Бажаю гарного втілення проєкту!

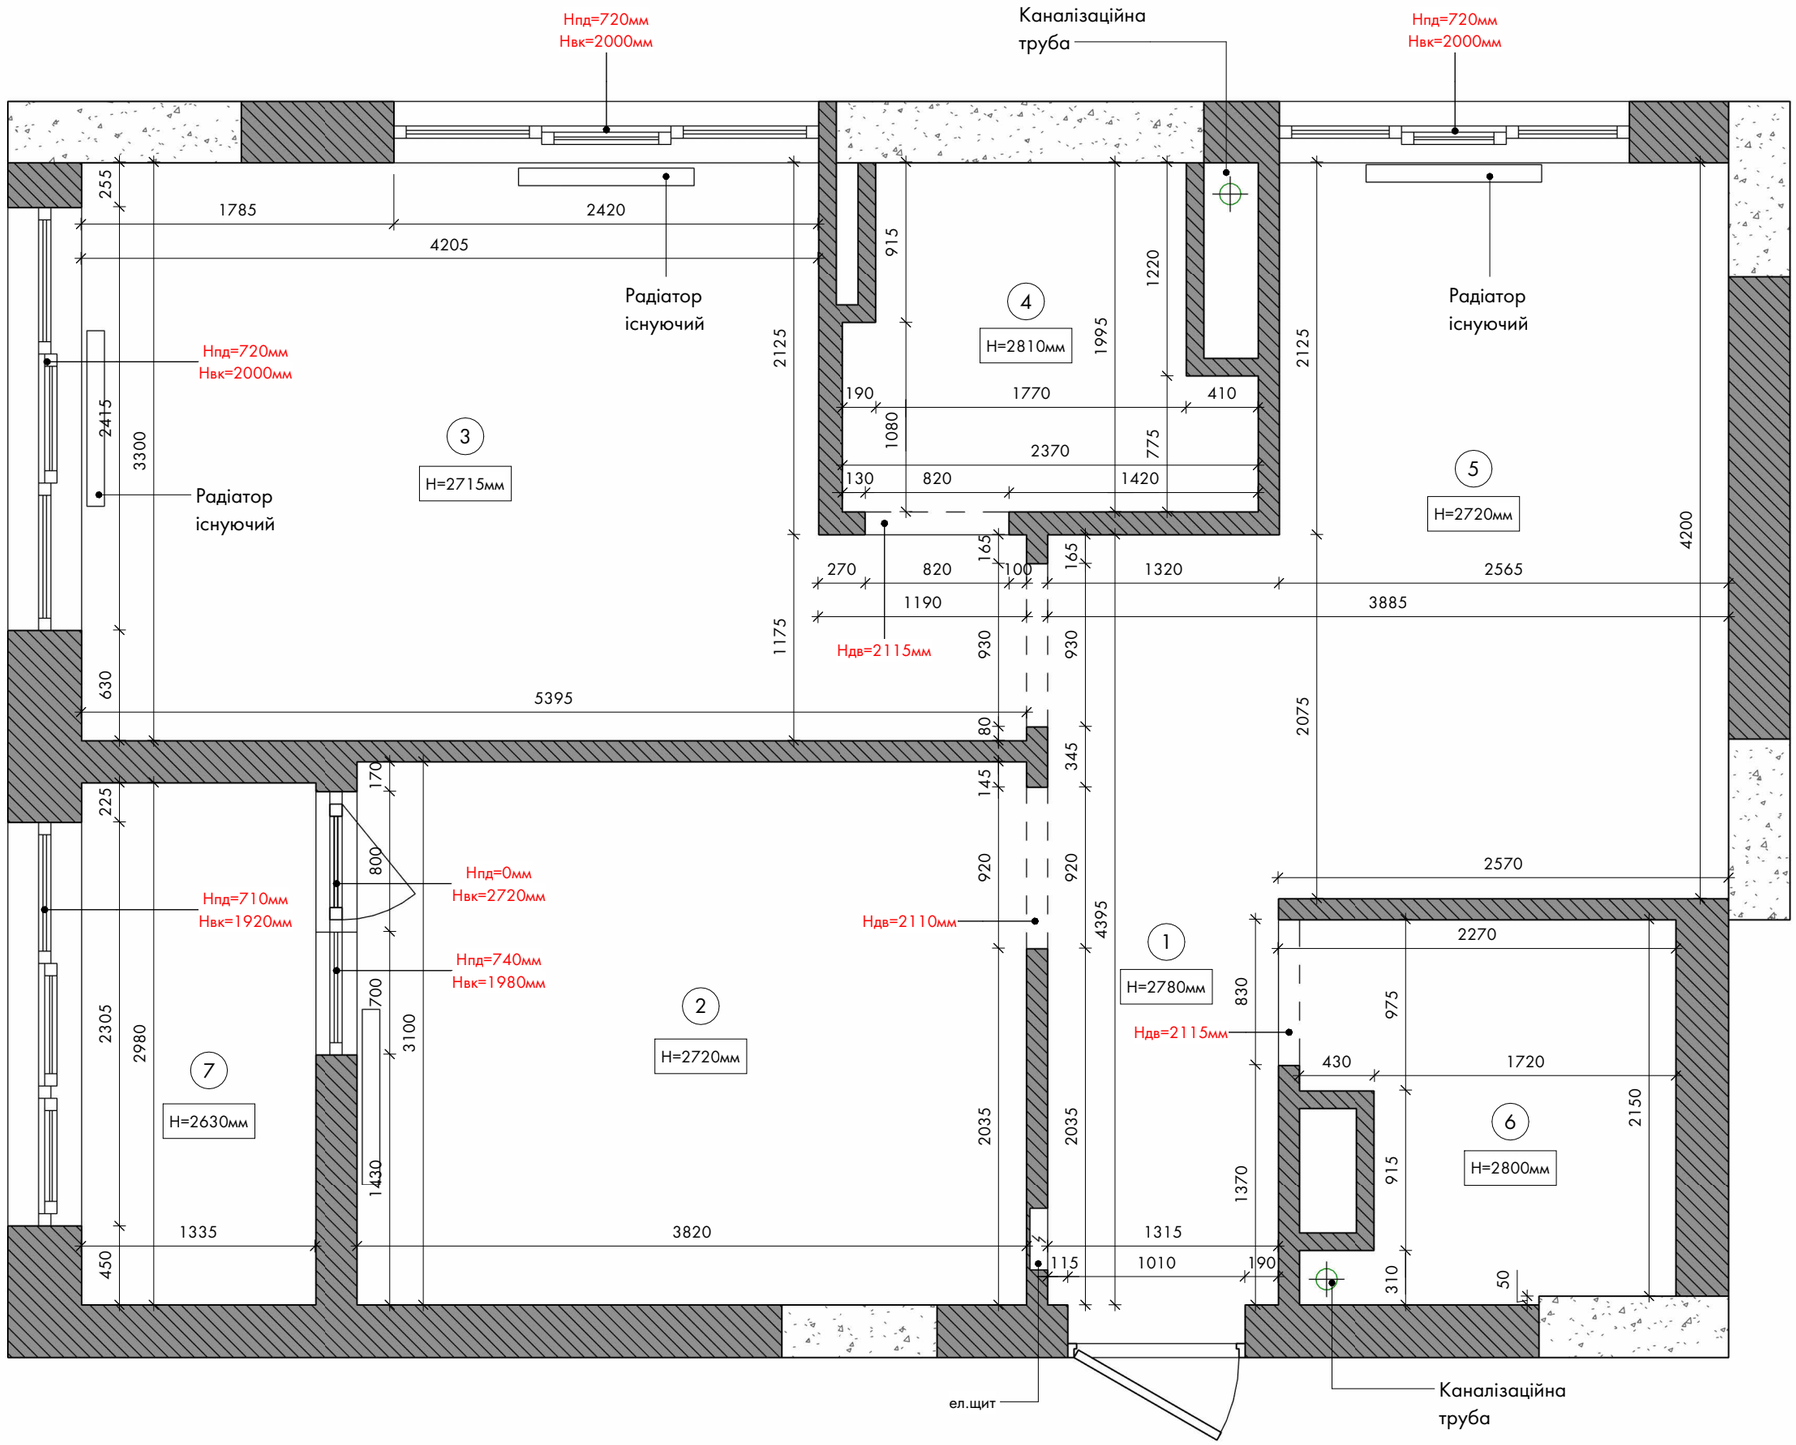

ПРИМІТКИ:

1. Всі розміри уточнити на місці.


Специфікація приміщень (обміри)

№	Назва	Площа
1	Передпокій	3.05 м²
2	Спальня 1	11.84 м²
3	Спальня 2	15.27 м²
4	Санвузол	4.05 м²
5	Кухня-вітальня	13.51 м²
6	Санвузол	4.30 м²
7	Балкон	3.98 м²
Загальна площа:		56.01 м²

SMIRNOVA
INTERIOR DESIGN

Назва проєкту:	Квартира
Адреса проєкту:	вул.Вавілових 11, кв.216

План обмірів
А-16

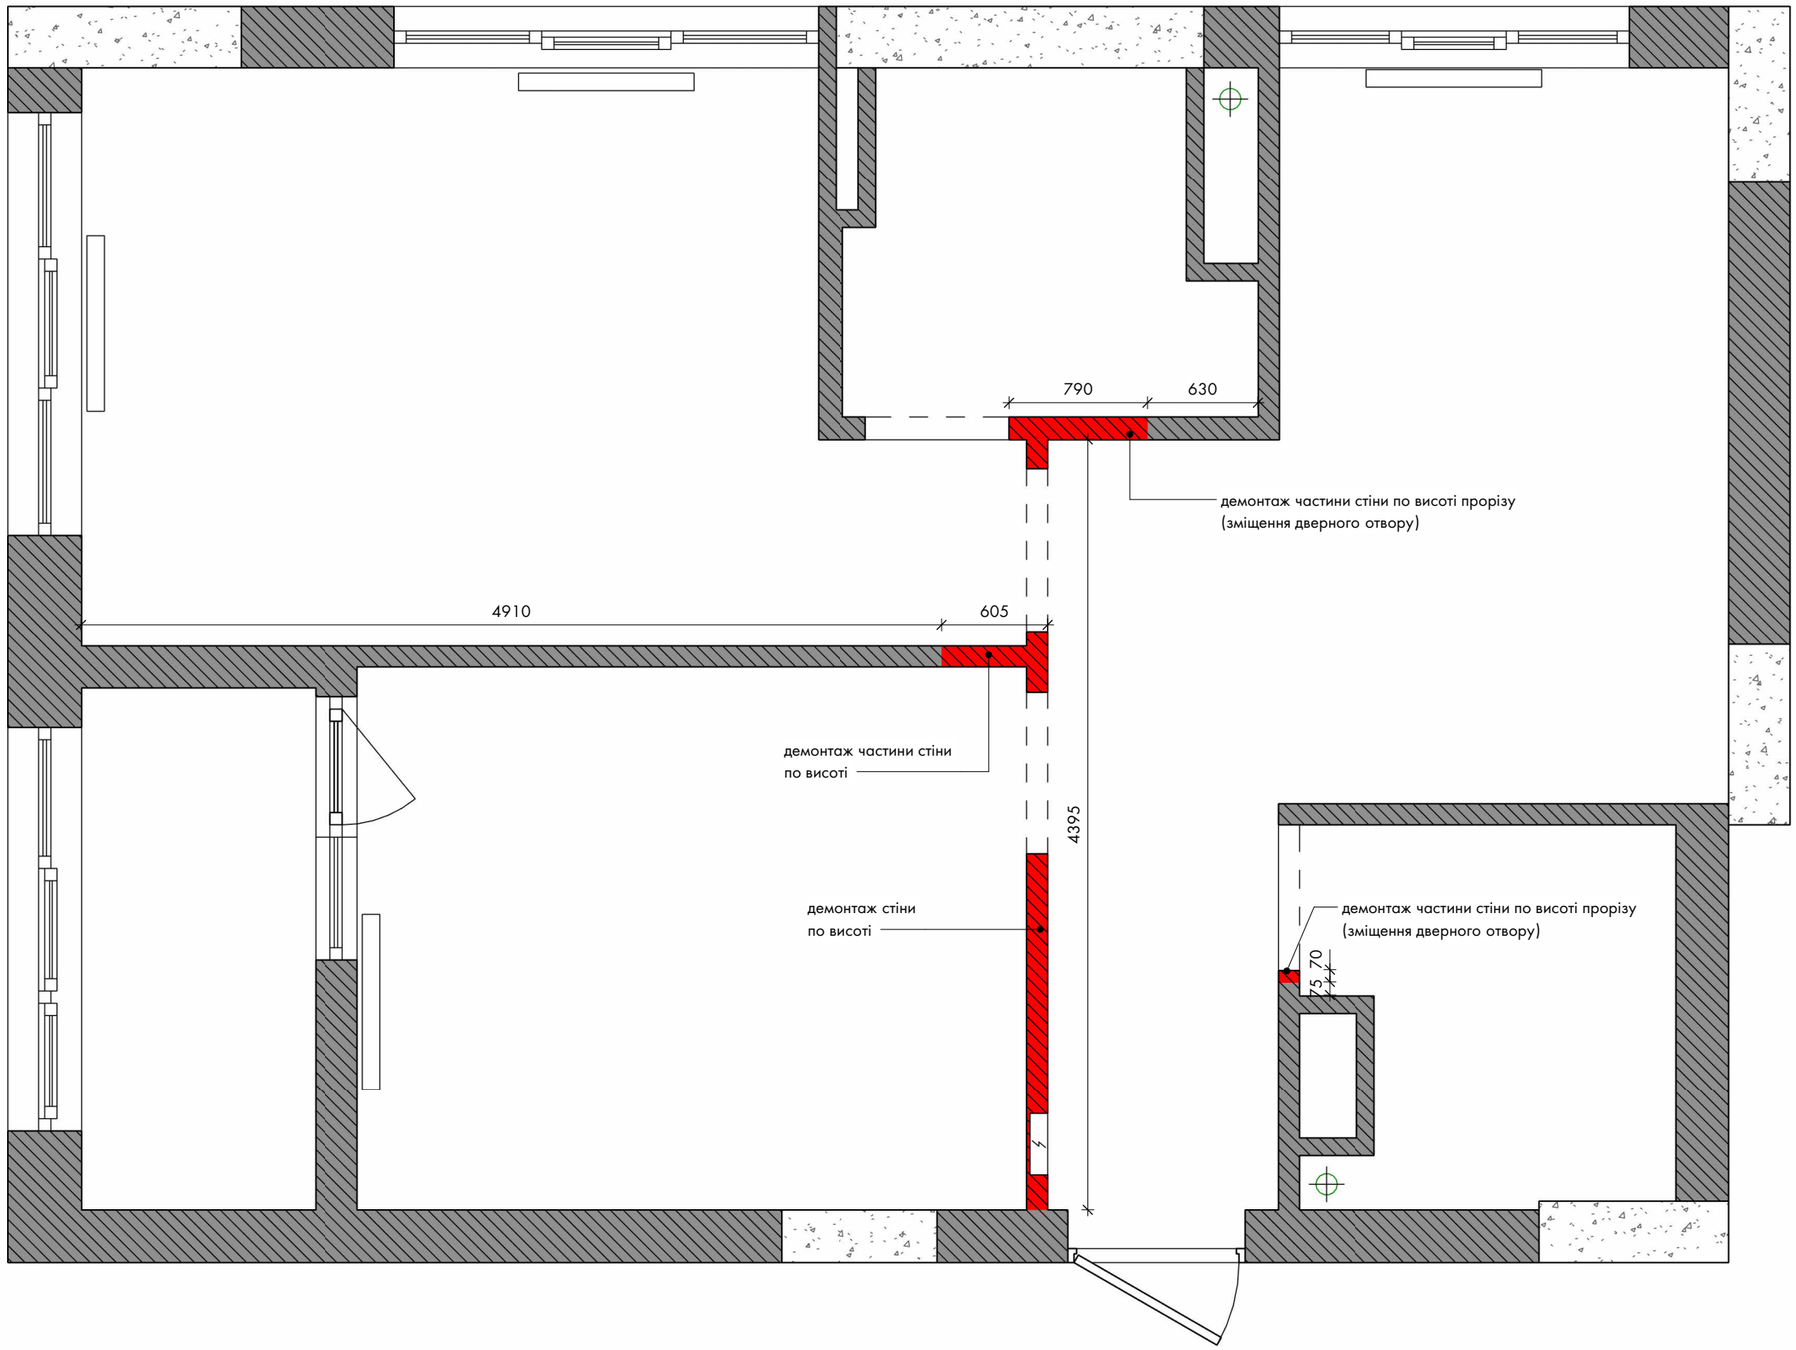

УМОВНІ ПОЗНАЧЕННЯ:

- демонтаж існуючих елементів


ПРИМІТКИ:

1. Всі розміри уточнити по місцю.

SMIRNOVA
INTERIOR DESIGN

Назва проєкту:	Квартира
Адреса проєкту:	вул.Вавілових 11, кв.216


План демонтажу
А-17

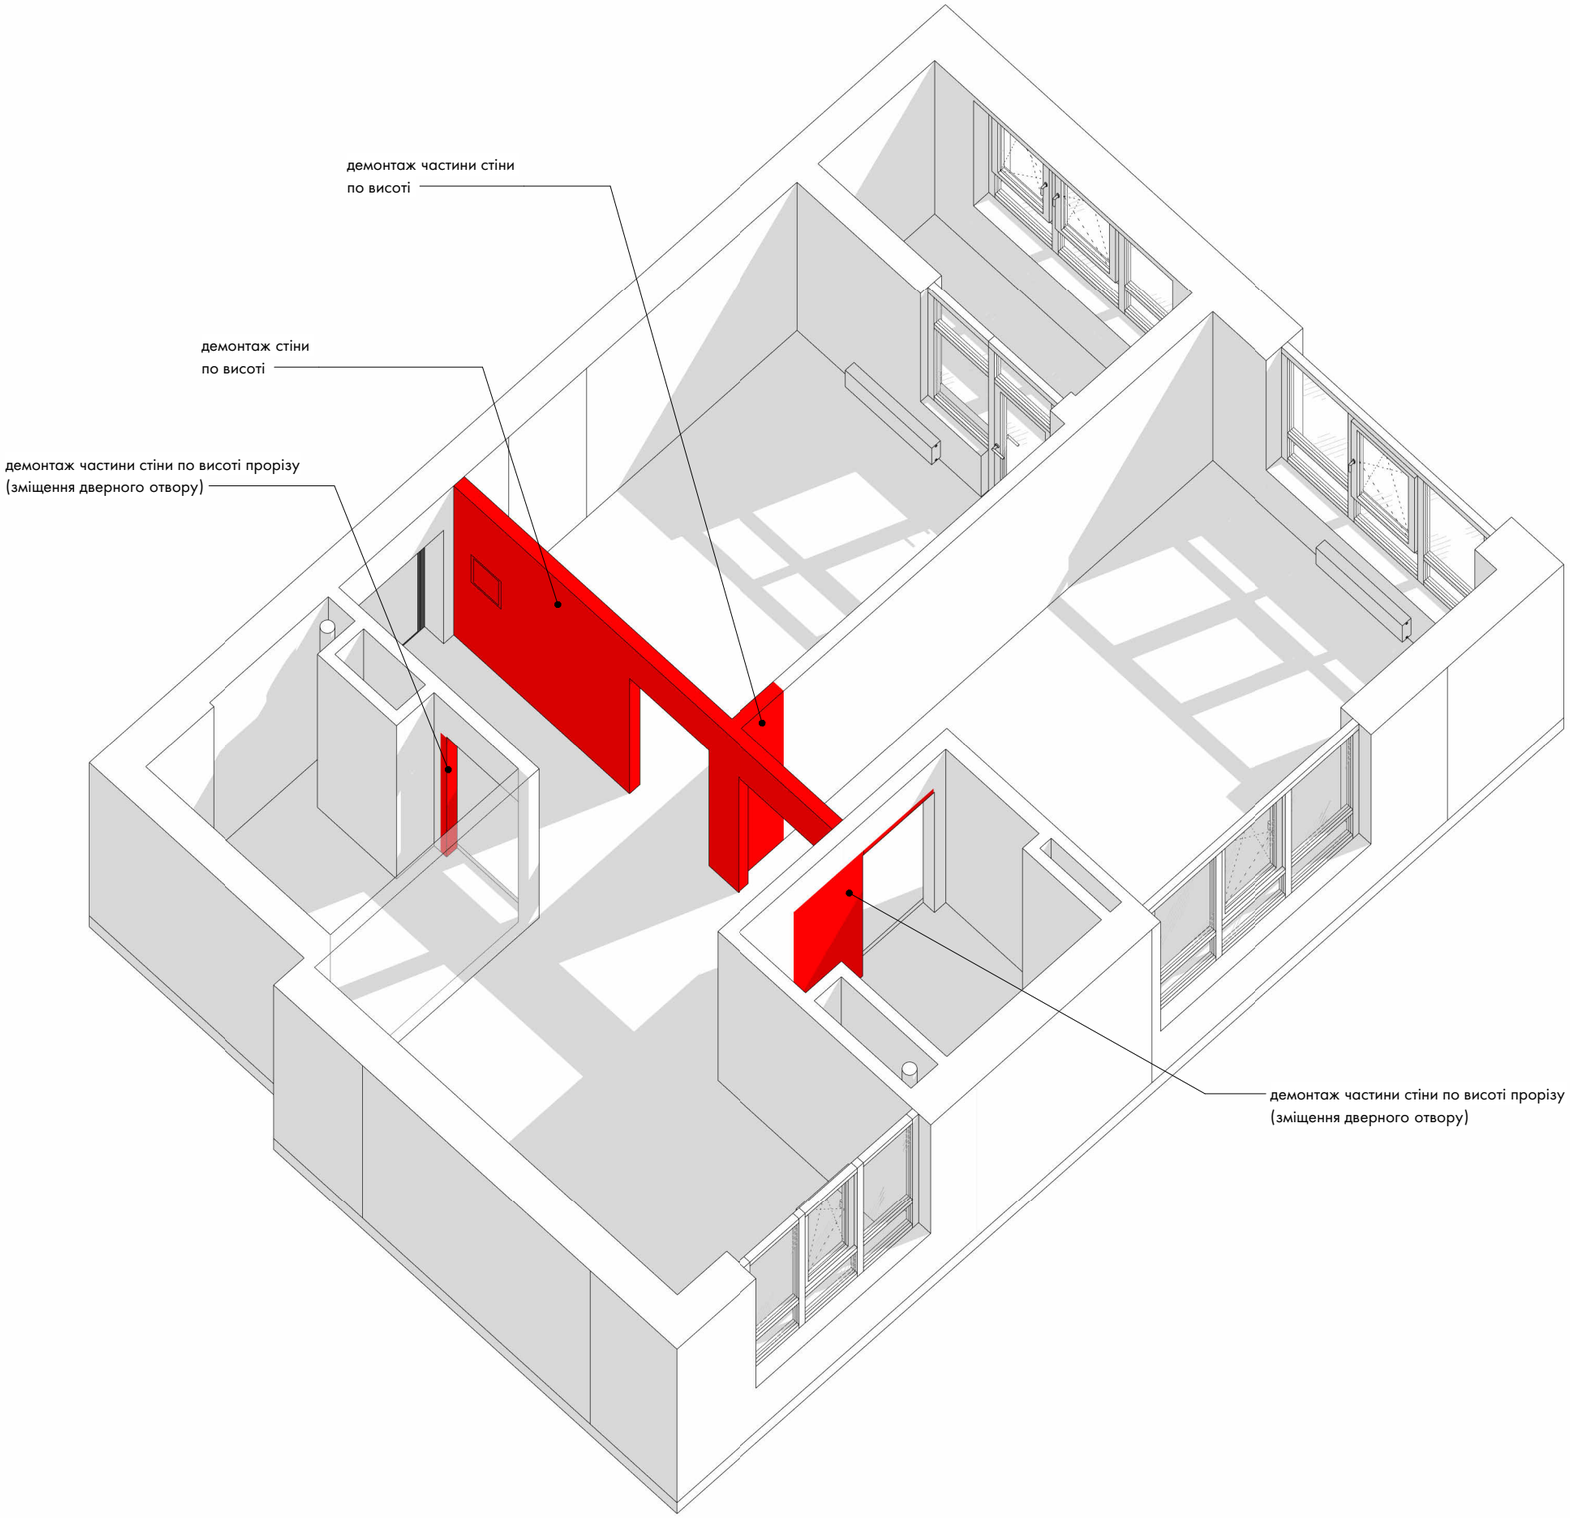

SMIRNOVA
INTERIOR DESIGN

Назва проєкту:	Квартира
Адреса проєкту:	вул.Вавілових 11, кв.216

3D-схема демонтажу
А-18

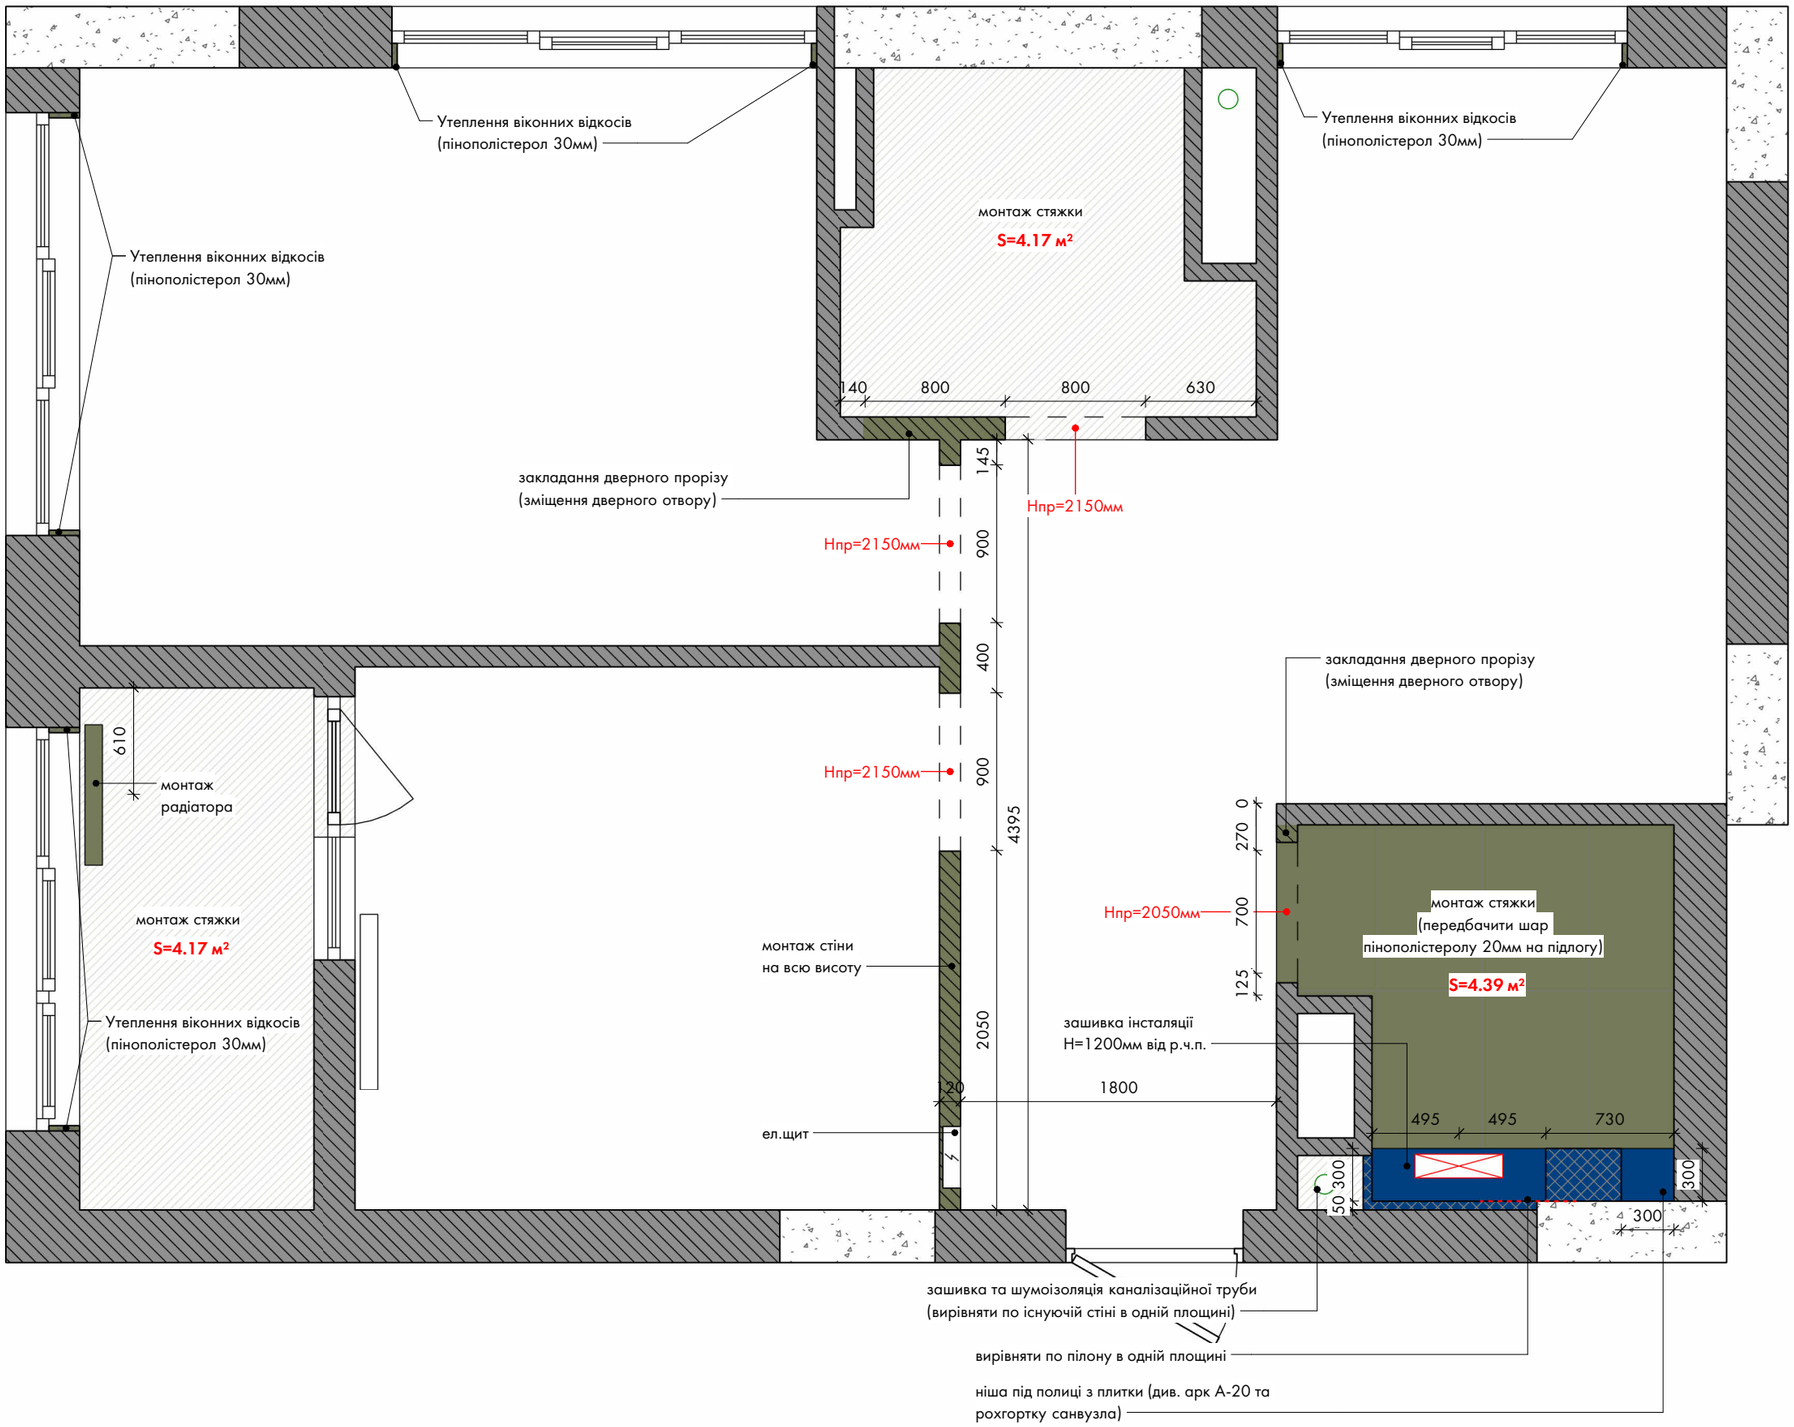

УМОВНІ ПОЗНАЧЕННЯ:

- монтаж перегородок
- монтаж ГКЛ / ГКЛВ перегородок
- монтаж стяжки
- монтаж інсталяції під унітаз


ПРИМІТКИ:

1. Всі розміри уточнити по місцю.
2. За позначку 0,000 прийнятий рівень чистої підлоги;
3. Висоти прорізів надані від чистового рівня підлоги.
4. Висоту приміщень до плити перекриття уточнити після вирівнювання поверхонь та визначення рівня чистої підлоги у всіх приміщеннях об'єкта.
5. Передбачити гідроізоляцію підлоги у вологих приміщеннях із закладом на стіни на 300 мм, а в зоні душової на всю висоту від стелі до підлоги.
6. У вологих приміщеннях перегородки виконати із вологостійкого ГКЛ.
7. Конструкцію стіни за унітазом з бачком прихованого монтажу зашити після встановлення інсталяції (бачка).
8. Встановити ревізійні люки прихованого монтажу для обслуговування стояків з комунікаціями; розташування та розміри люків уточнити на місці.
9. Необхідну кількість матеріалів розрахувати на місці після демонтажних робіт.
10. Виконати закладні елементи для підвісної шафи та підвісної тумби в санвузлі.

SMIRNOVA
INTERIOR DESIGN


Назва проєкту:	Квартира
Адреса проєкту:	вул.Вавілових 11, кв.216

План монтажу
А-19

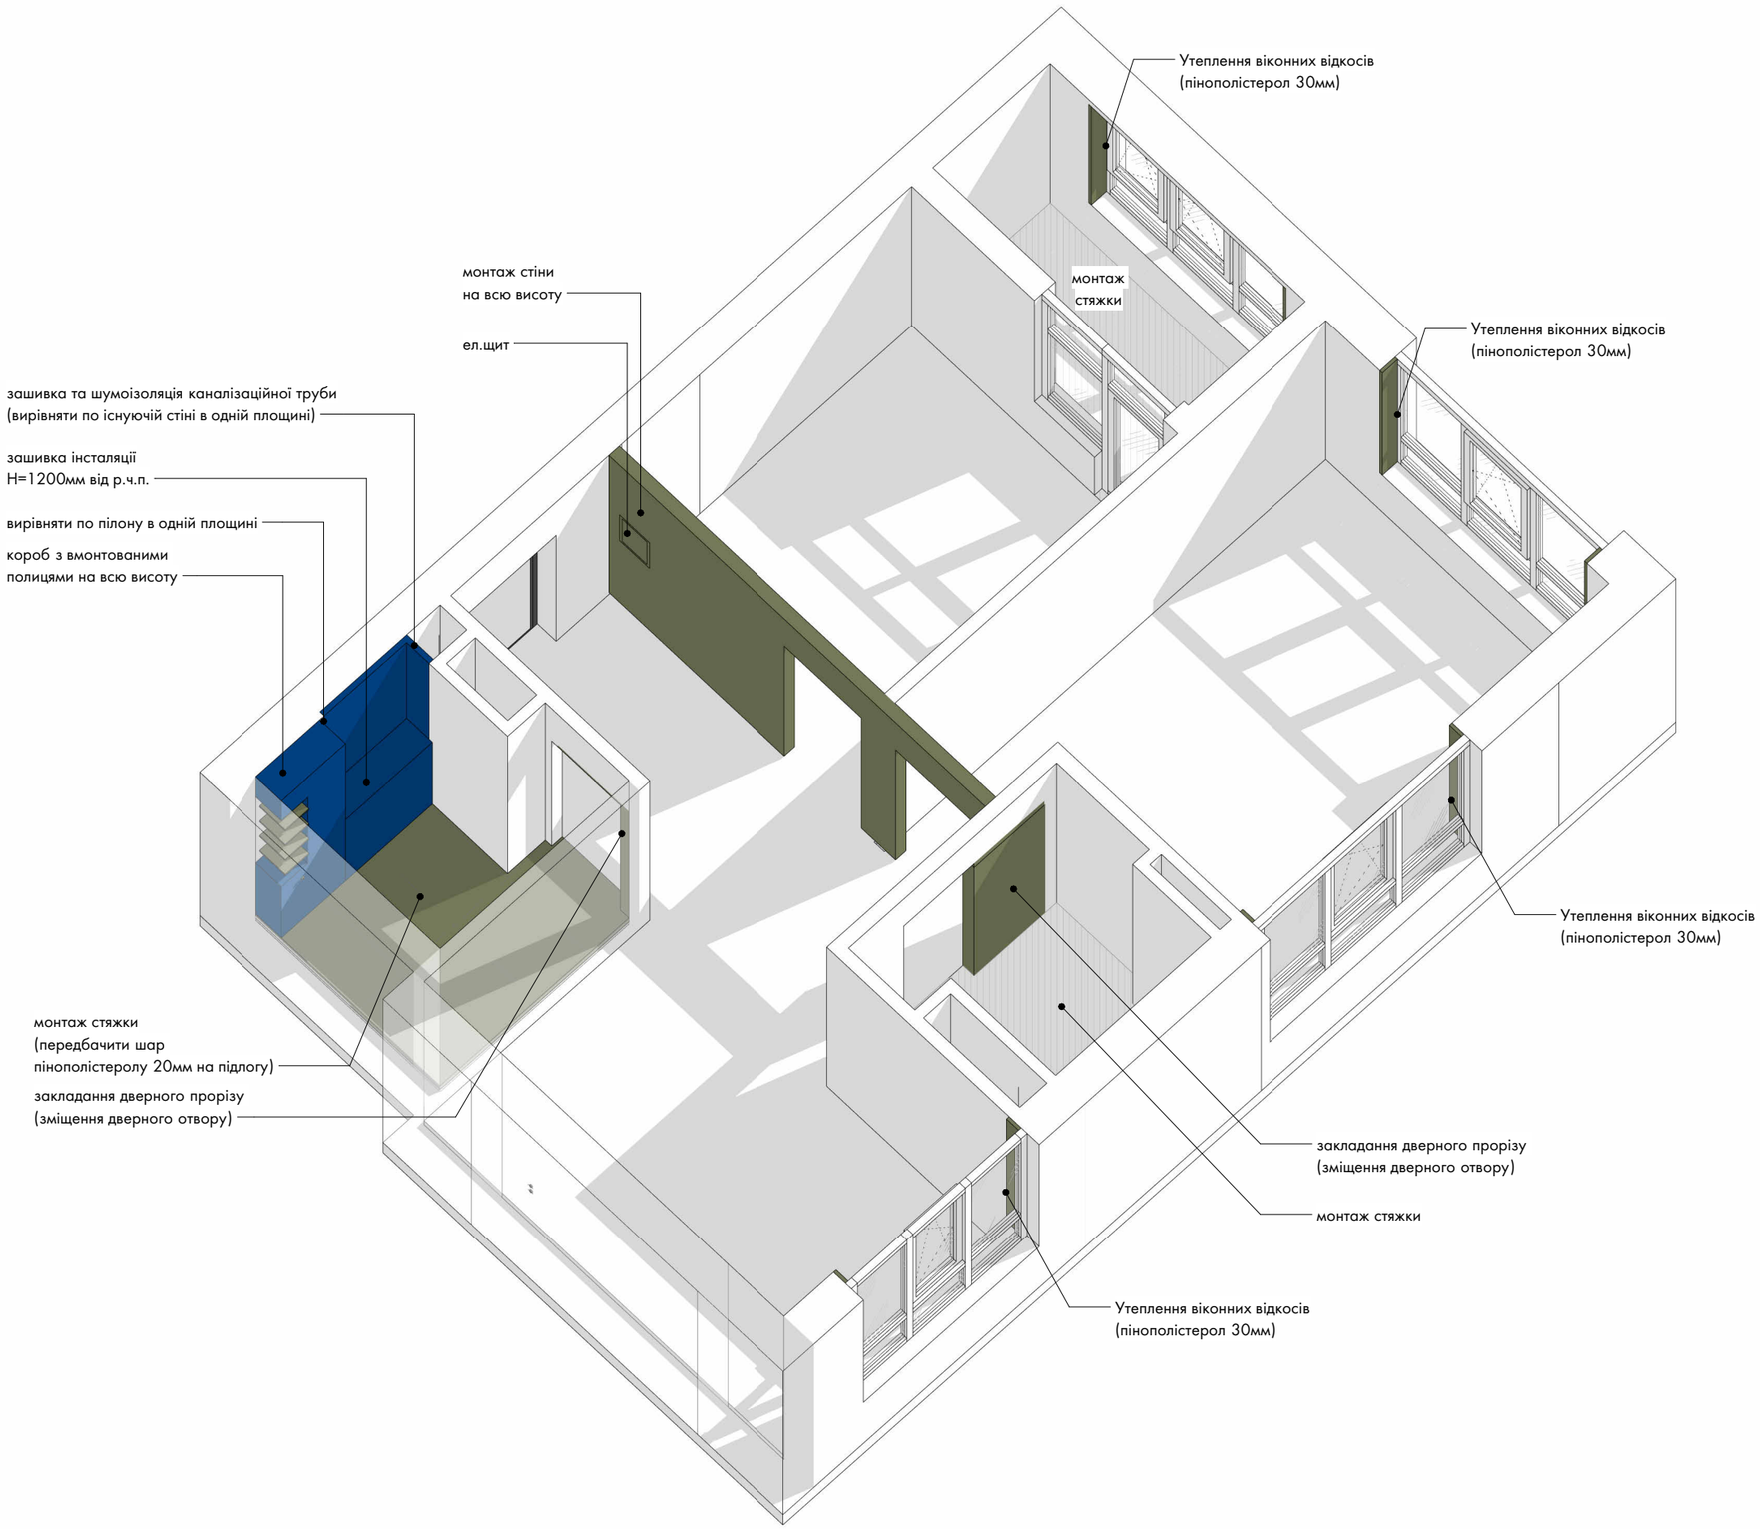

УМОВНІ ПОЗНАЧЕННЯ:

- монтаж перегородок
- монтаж ГКЛ / ГКЛВ перегородок
- монтаж стяжки

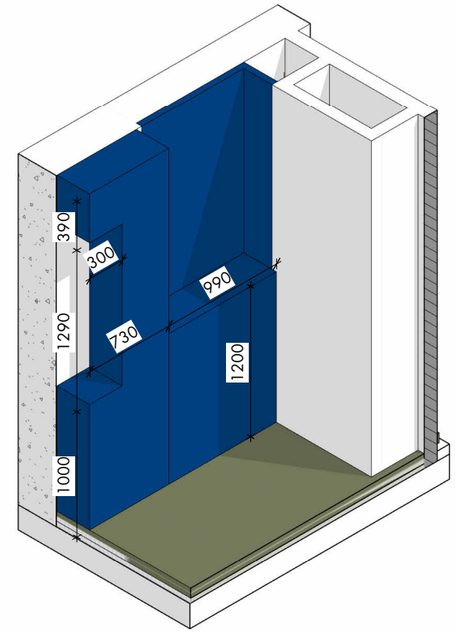


3D - схема (фрагмент санвузла)

SMIRNOVA
INTERIOR DESIGN

Назва проєкту:	Квартира
Адреса проєкту:	вул.Вавілових 11, кв.216

3D-схема монтажу
А-20

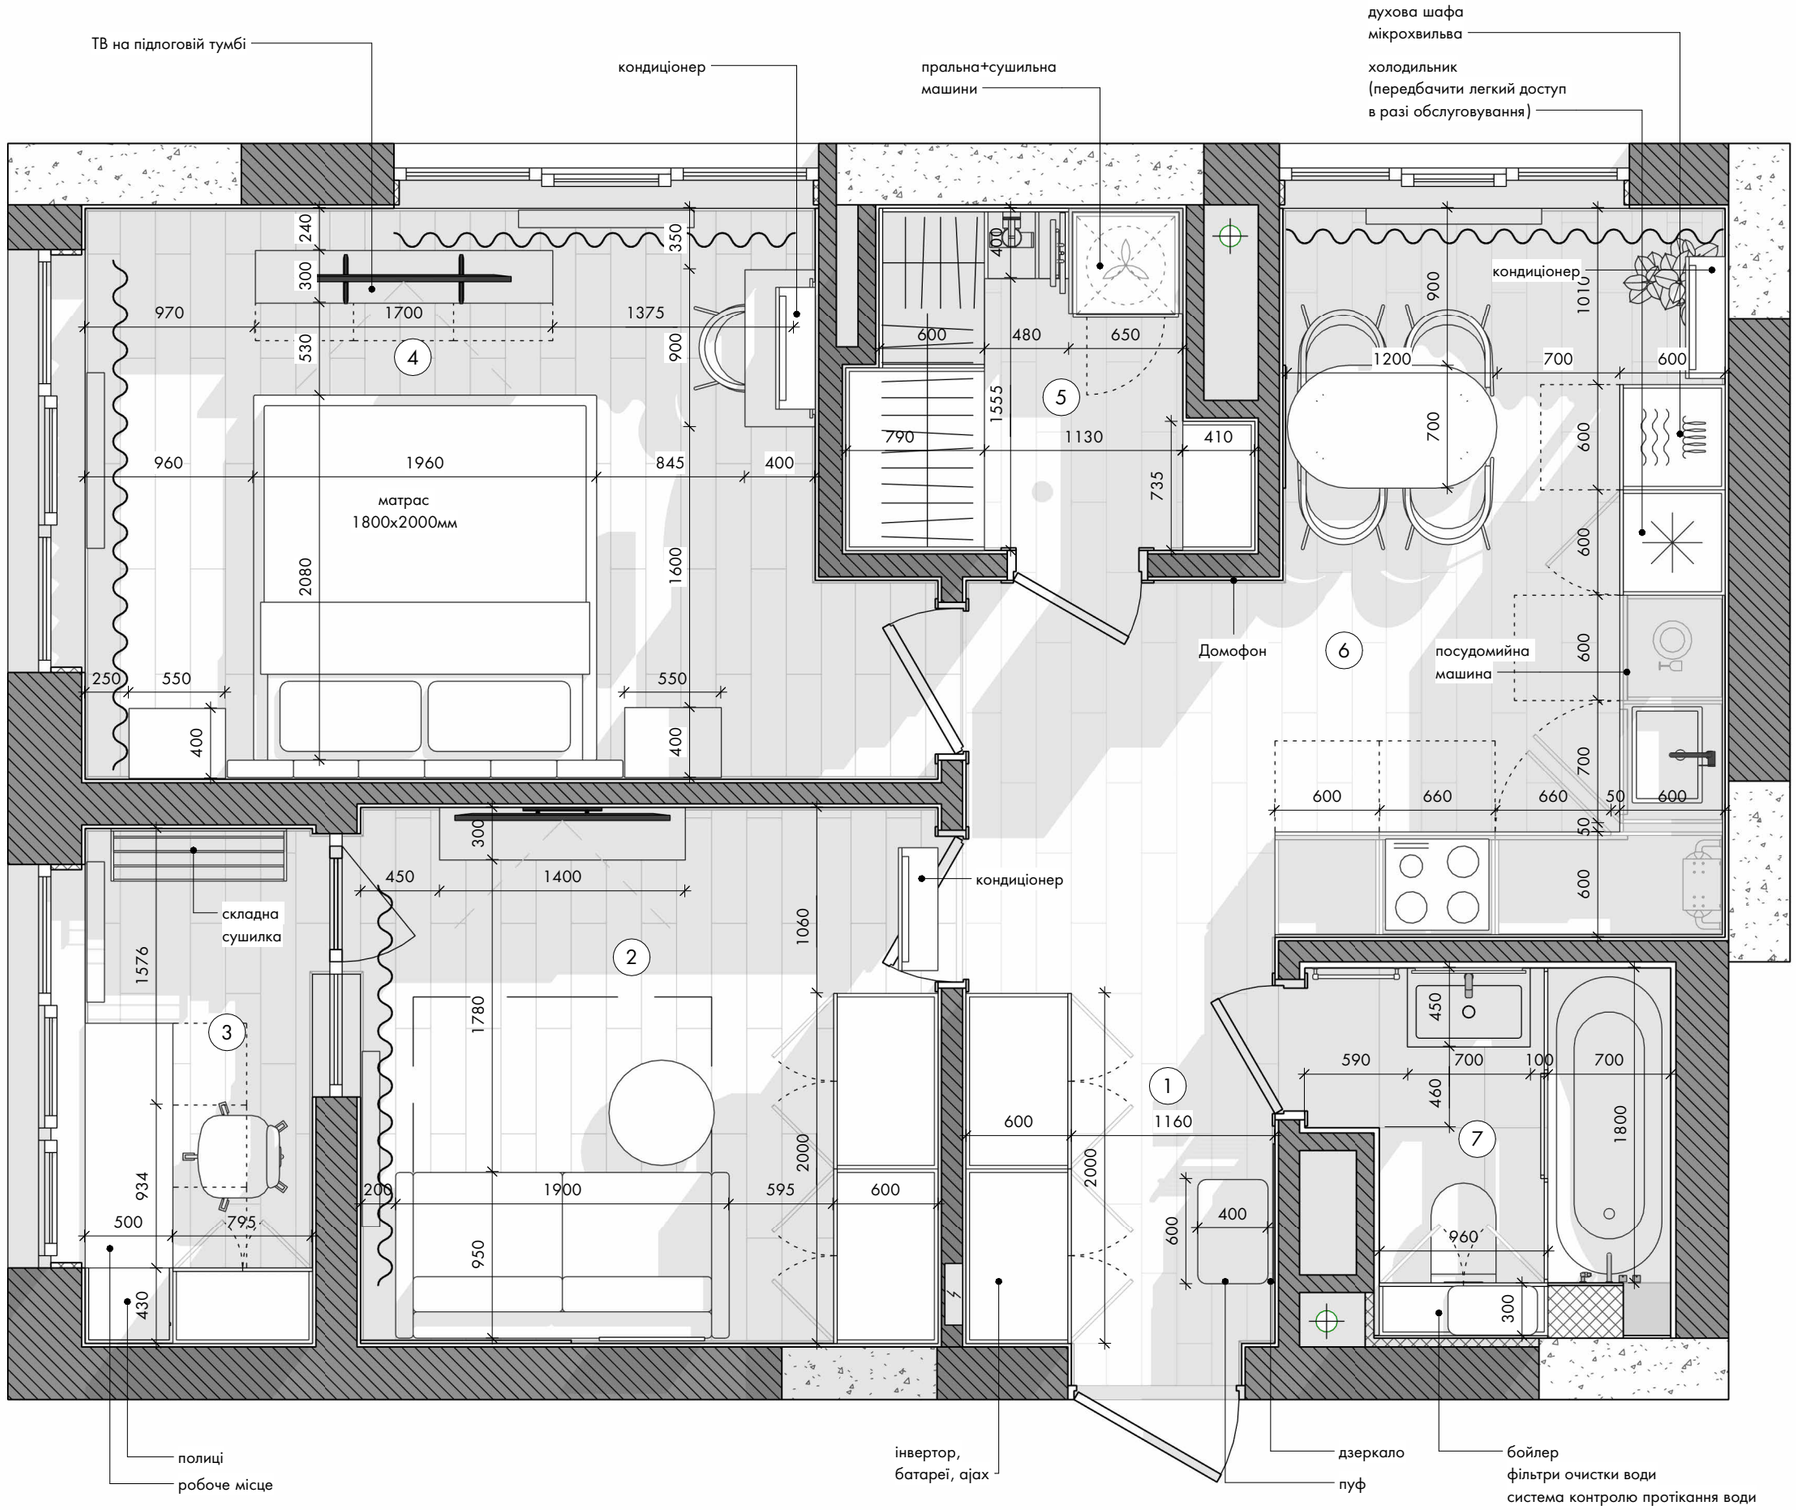

ПРИМІТКИ:

1. Дивитись аркуш разом із кресленнями елементів на замовлення й візуалізаціями.
2. Перед виконанням робіт та замовленням меблів виміряти фактичні габарити підготовлених конструкцій.
3. Усі розміри кухонних модулів та вбудованих шаф уточнювати фірмою-виробником після обміру об'єкта.

Специфікація приміщень

№	Назва	Площа
1	Передпокій	4.05 м²
2	Кімната	10.06 м²
3	Лоджія	3.81 м²
4	Спальня	14.38 м²
5	Гардеробна	3.88 м²
6	Кухня-вітальня	14.15 м²
7	Санвузол	2.30 м²
Загальна площа:		52.62 м²

SMIRNOVA
INTERIOR DESIGN

Назва проєкту:	Квартира
Адреса проєкту:	вул.Вавілових 11, кв.216

План меблів
А-21




ПРИМІТКИ:

1. Дивитись аркуш разом із планом меблів.

SMIRNOVA
INTERIOR DESIGN

Назва проєкту:	Квартира
Адреса проєкту:	вул.Вавілових 11, кв.216


3D-схема №1
А-22

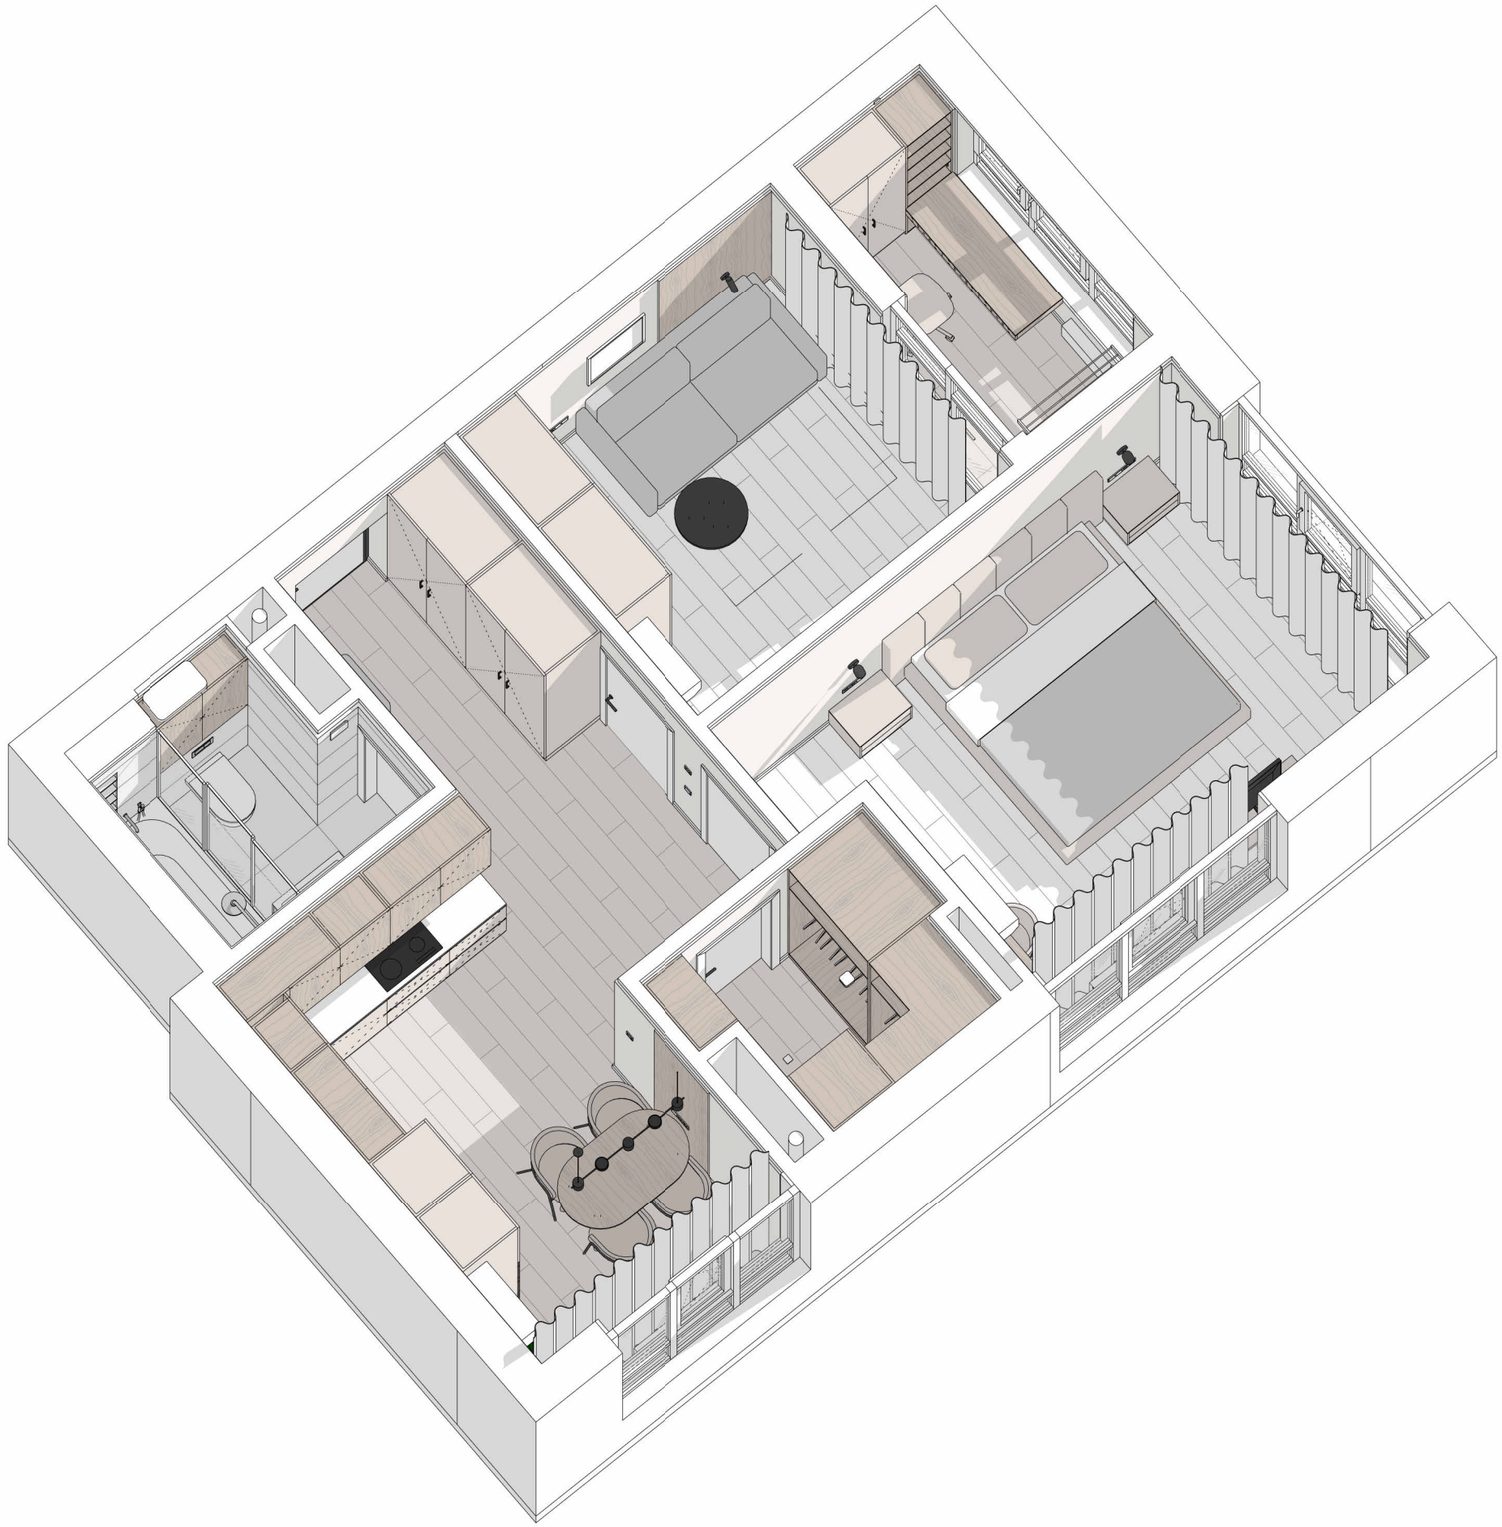

SMIRNOVA
INTERIOR DESIGN

Назва проєкту:	Квартира
Адреса проєкту:	вул.Вавілових 11, кв.216

3D-схема №2
A-23

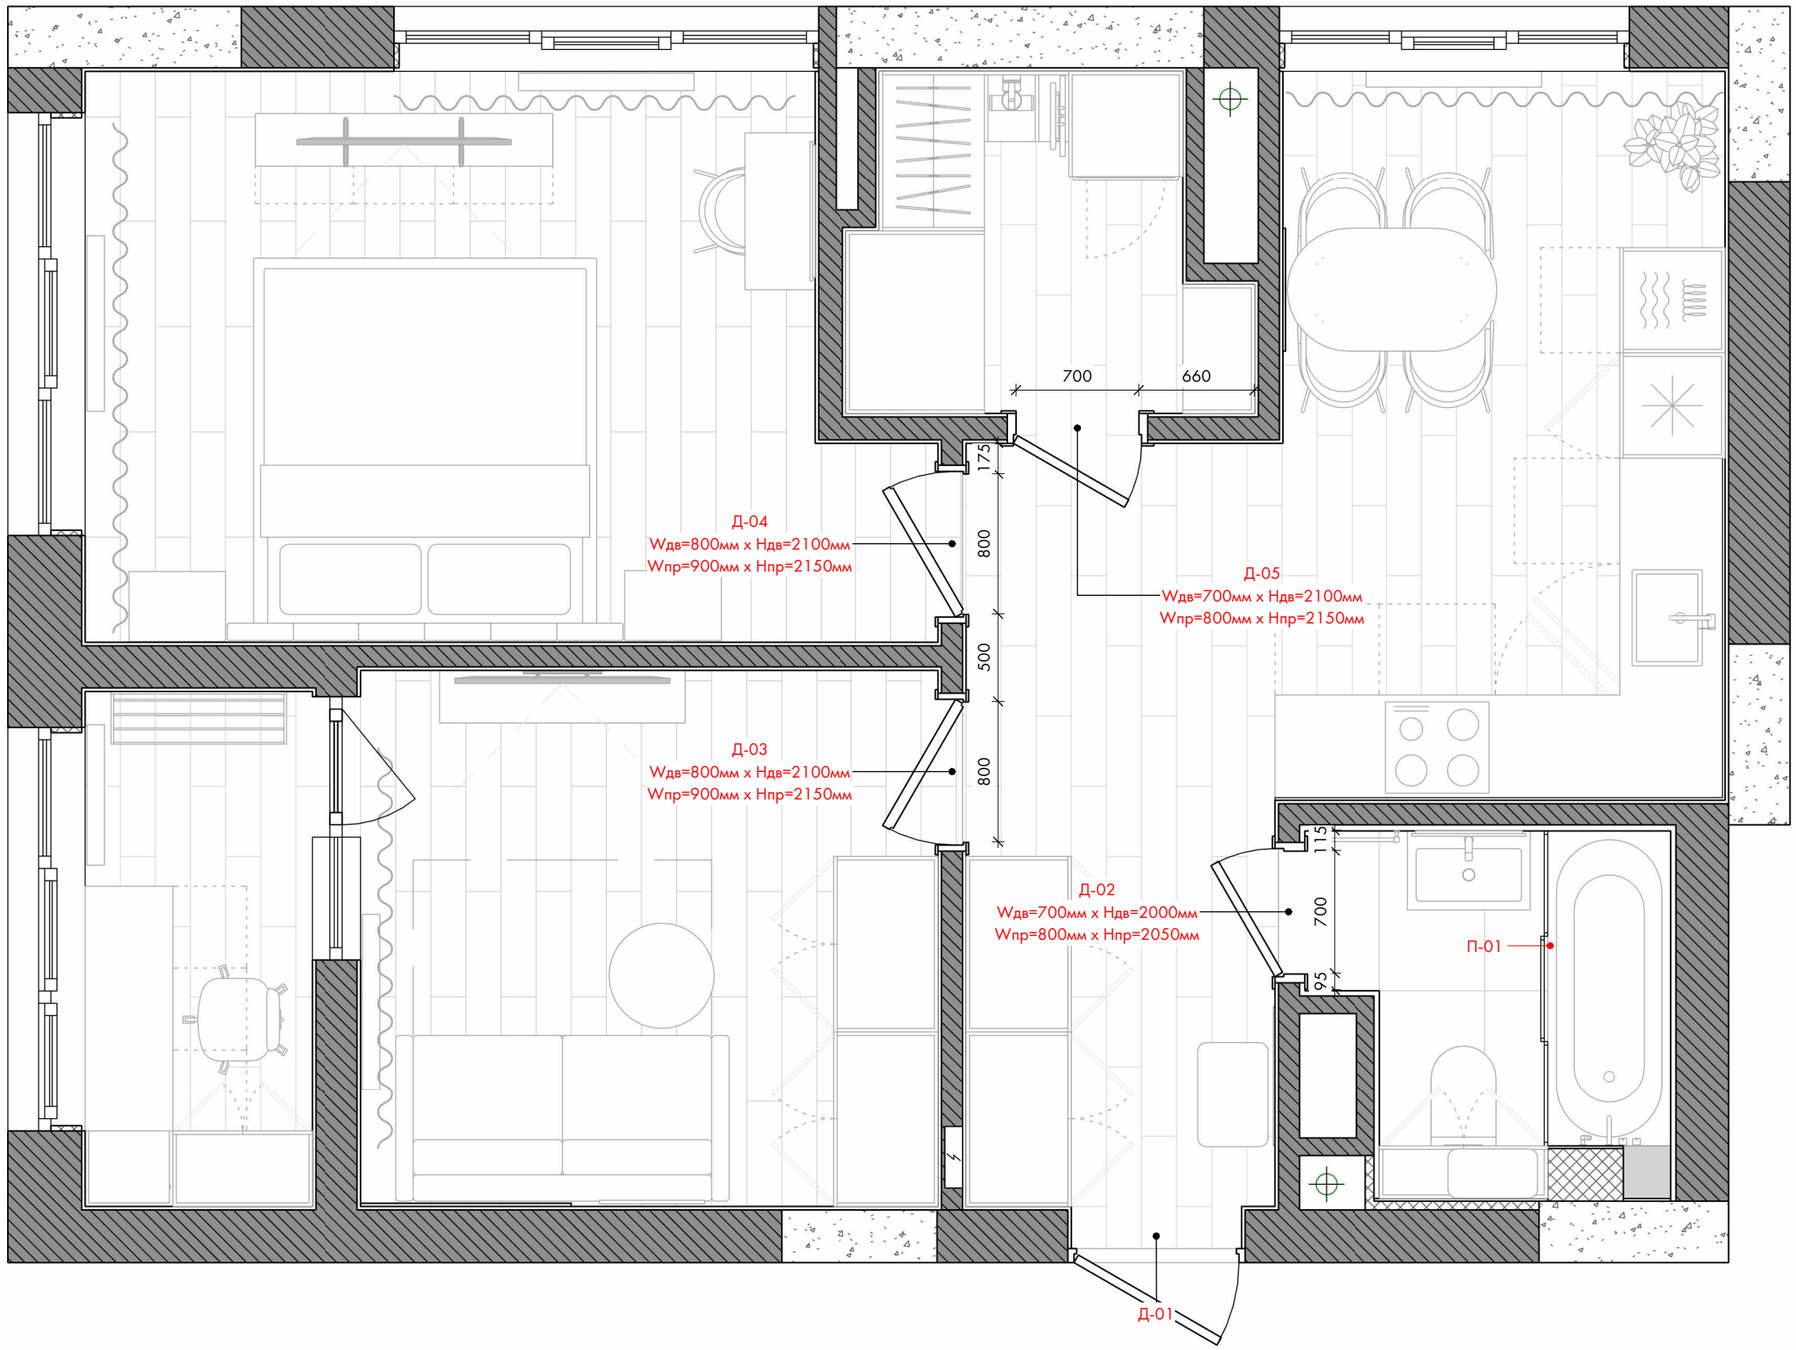

УМОВНІ ПОЗНАЧЕННЯ:

Д-01... - маркування дверей

EQ - еквівалентний (рівнозначний) розмір

ПРИМІТКИ:

1. Всі розміри уточнити по місцю.
2. Перед замовленням дверей та перегородок провести заміри.
3. Матеріал виготовлення дверей уточнити й узгодити із замовником.
4. Дивитися аркуш разом зі специфікацією дверей та перегородок.

Специфікація приміщень

№	Назва	Площа
1	Передпокій	4.05 м²
2	Кімната	10.06 м²
3	Лоджія	3.81 м²
4	Спальня	14.38 м²
5	Гардеробна	3.88 м²
6	Кухня-вітальня	14.15 м²
7	Санвузол	2.30 м²
Загальна площа:		52.62 м²

SMIRNOVA
INTERIOR DESIGN

Назва проєкту:	Квартира
Адреса проєкту:	вул.Вавілових 11, кв.216

План заповнення дверних прорізів
А-24

СПЕЦИФІКАЦІЯ ДВЕРЕЙ

№	Ширина полотна	Висота полотна	Ширина отвору	Висота отвору	Відчинення	Примітки
Д-01	910	2100	1010	2150	Ліворуч назовні	Існуючі вхідні двері
Д-02	700	2000	800	2050	Праворуч назовні	Проектуючі міжкімнатні двері з лиштвою. Ручка, колір чорний, мат. Передбачити магнітні стопери, замок.
Д-03	800	2100	900	2150	Праворуч всередину	Проектуючі міжкімнатні двері з лиштвою. Ручка, колір чорний, мат. Передбачити магнітні стопери.
Д-04	800	2100	900	2150	Ліворуч всередигу	Проектуючі міжкімнатні двері з лиштвою. Ручка, колір чорний, мат. Передбачити магнітні стопери.
Д-05	700	2100	800	2150	Ліворуч назовні	Проектуючі міжкімнатні двері з лиштвою. Ручка, колір чорний, мат. Передбачити магнітні стопери.


ПРИМІТКИ:

1. Всі розміри уточнити по місцю.
2. Перед замовленням дверей провести заміри.
3. Матеріал виготовлення дверей уточнити й узгодити із замовником.
4. Дивитися аркуш разом з планом дверей та перегородок.

SMIRNOVA
INTERIOR DESIGN

Назва проєкту:	Квартира
Адреса проєкту:	вул.Вавілових 11, кв.216

Специфікація дверей
А-25

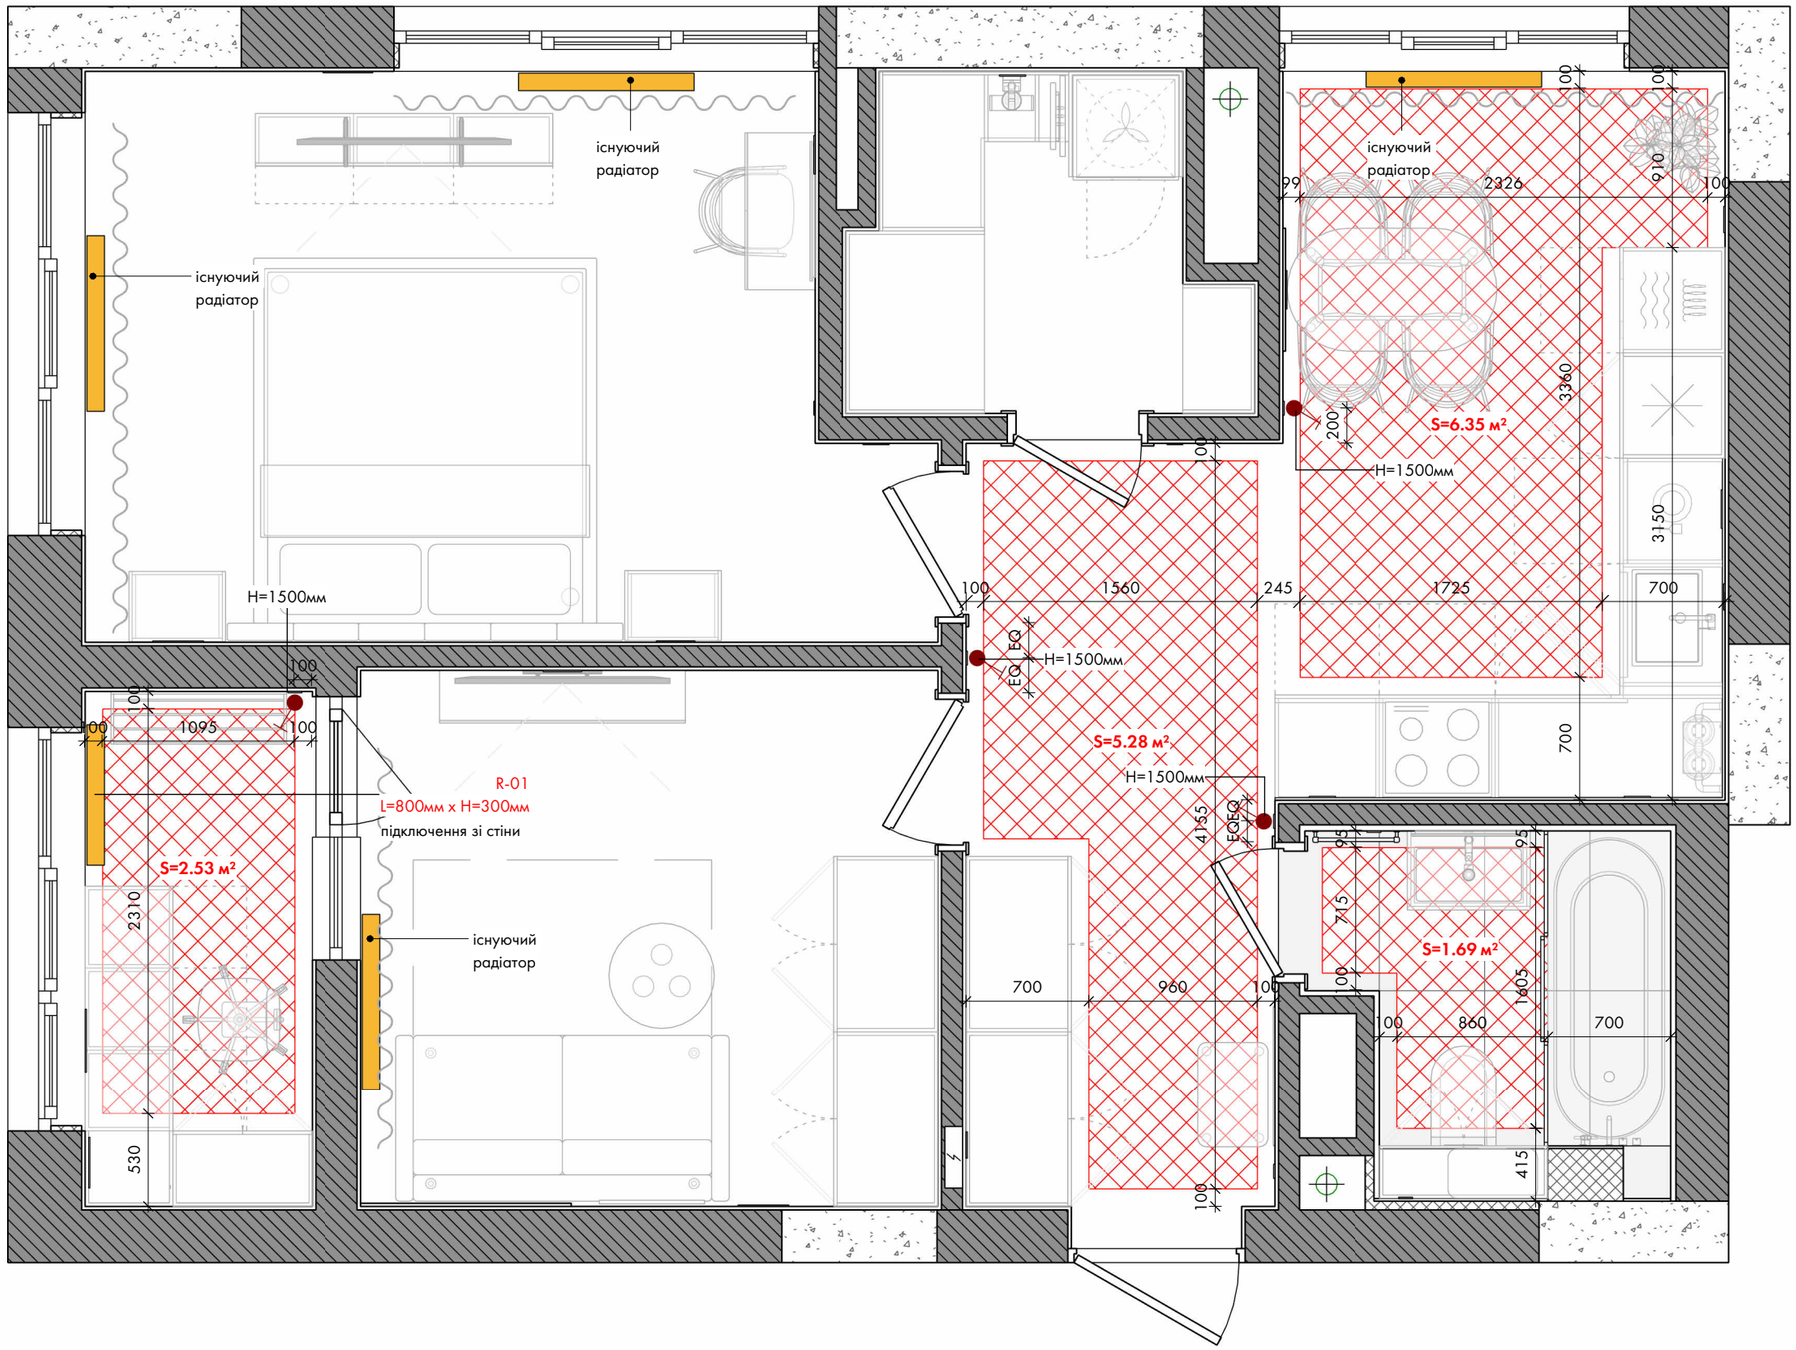

УМОВНІ ПОЗНАЧЕННЯ:

R-01... - маркування радіаторів опалення

EQ - еквівалентний (рівнозначний) розмір

- електрична тепла підлога

Специфікація теплої підлоги

Назва	Площа
Електрична тепла підлога	15.85 м²

Специфікація терморегуляторів

Символ	Назва	Кількість
	Терморегулятор	4

ПРИМІТКИ:


1. Всі розміри уточнити на місці.
2. Розмір, потужність радіаторів підібрати та, при необхідності, скоригувати з фахівцем.
3. У проєкті закладено електричну теплу підлогу.
4. Всі прив'язки теплої підлоги узгодити та, при необхідності, скоригувати з фахівцем.
5. Остаточне розташування терморегуляторів уточнити по місцю та узгодити з фахівцем.

SMIRNOVA
INTERIOR DESIGN

Назва проєкту:	Квартира
Адреса проєкту:	вул.Вавілових 11, кв.216


План опалення

A-26

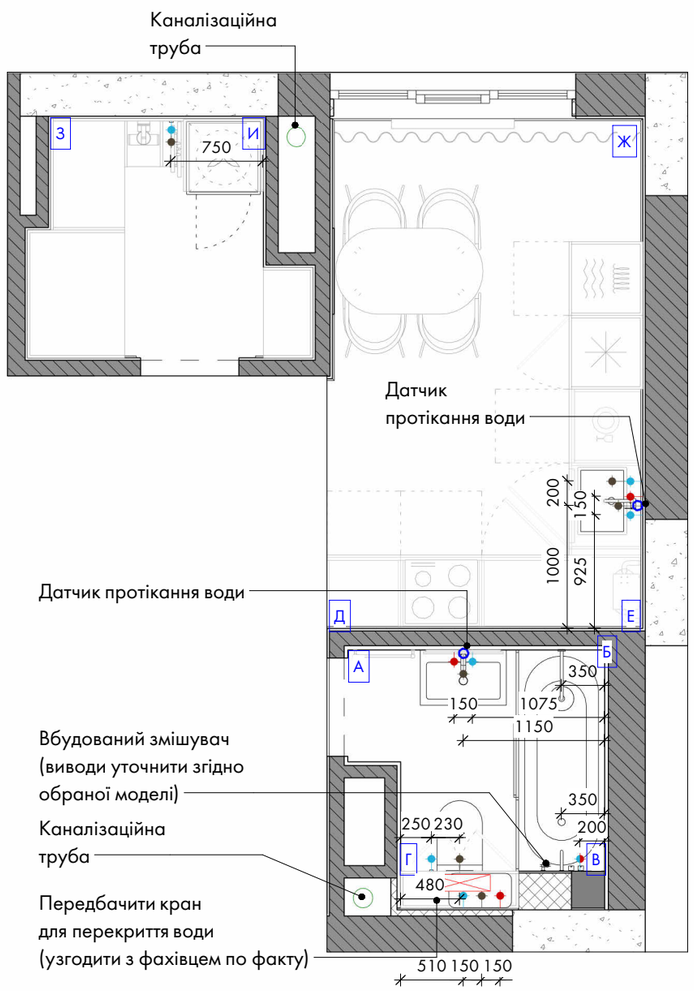


План сантехнічних виводів

1 : 50

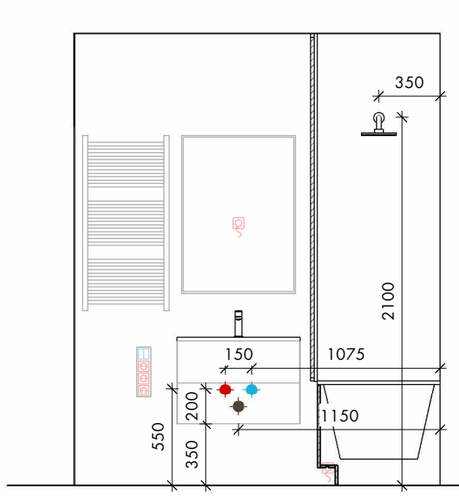


А-Б

1 : 35

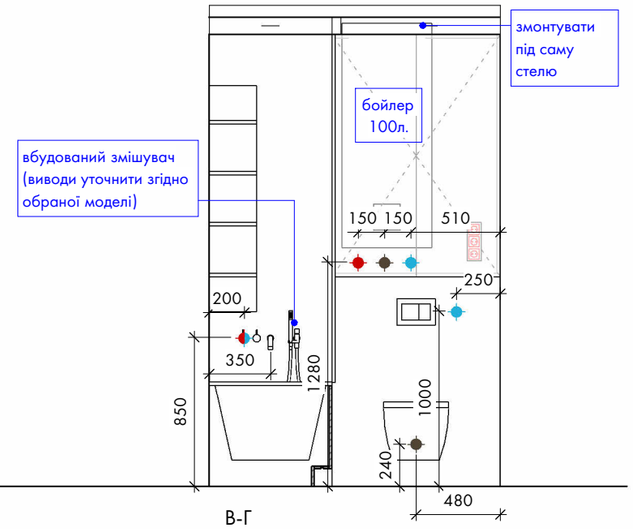


В-Г

1 : 35

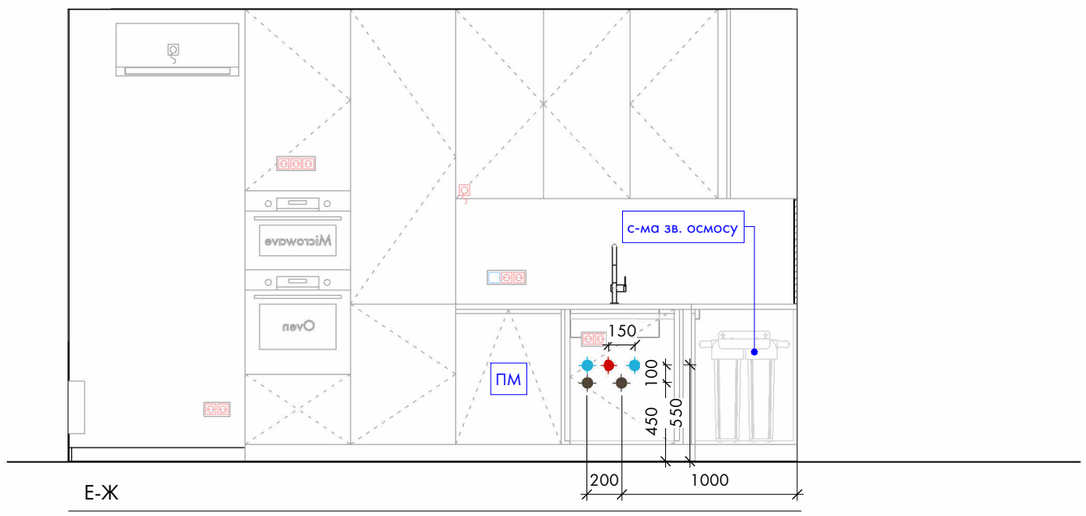

Е-Ж

1 : 35

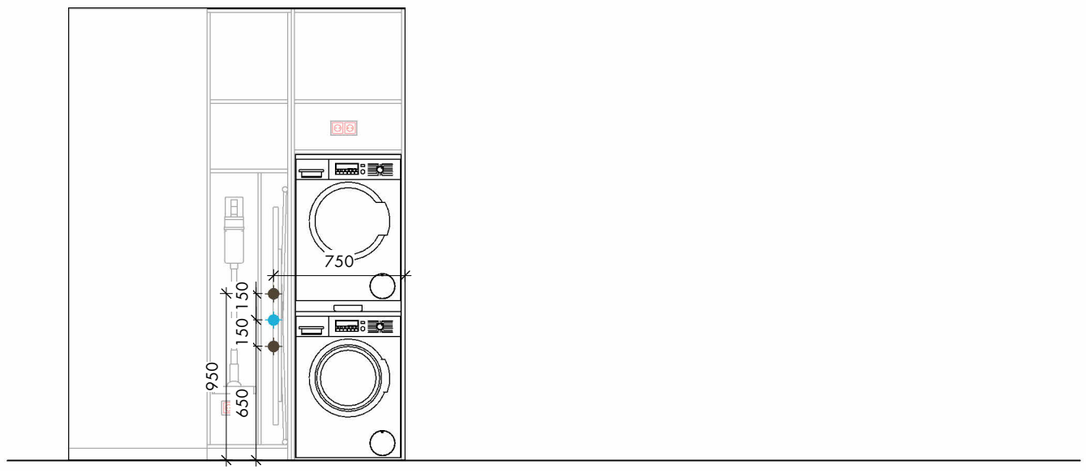

З-И

1 : 35

УМОВНІ ПОЗНАЧЕННЯ:

- холодне водопостачання
- гаряче водопостачання
- вбудована частина змішувача
- водовідведення
- інсталяція під унітаз
- 01 - маркування сантехнічних приладів
- EQ - еквівалентний (рівнозначний) розмір


ПРИМІТКИ:

1. Всі розміри уточнити на місці.
2. Всі розміри вказані з урахуванням оздоблювальних матеріалів.
3. Всі висоти надані від чистового рівня підлоги.
4. Виконати ухил до трапу 0.02%.
5. Точне місцезнаходження стояків на об'єкті визначити на місці.
6. Привязки вивода комунікацій уточнити після кінцевого підбору сантехнічного обладнання.
7. Монтаж сантехнічного обладнання виконувати згідно з інструкціями до виробів.
8. Для зливa унітаза використовувати трубу діаметром 100 мм, для інших не менше 50 мм.
9. Рекомендований ухил каналізаційних труб: для труб діаметром не 50 мм-0,03 (3 см на 1 м.п. труби), для труб діаметром 100 мм-0,02 (2 см на 1 м.п. труби).
10. Встановити ревізійні люки прихованого монтажу під оздоблення для обслуговування стояків з комунікаціями , розташування і розмір люків уточнити по місцю.
11. Встановити фільтри для очіщення проточної води на магістралі водопостачання.

SMIRNOVA
INTERIOR DESIGN

Назва проєкту:	Квартира
Адреса проєкту:	вул.Вавілових 11, кв.216

Плани та розгортки сантехніки
А-27

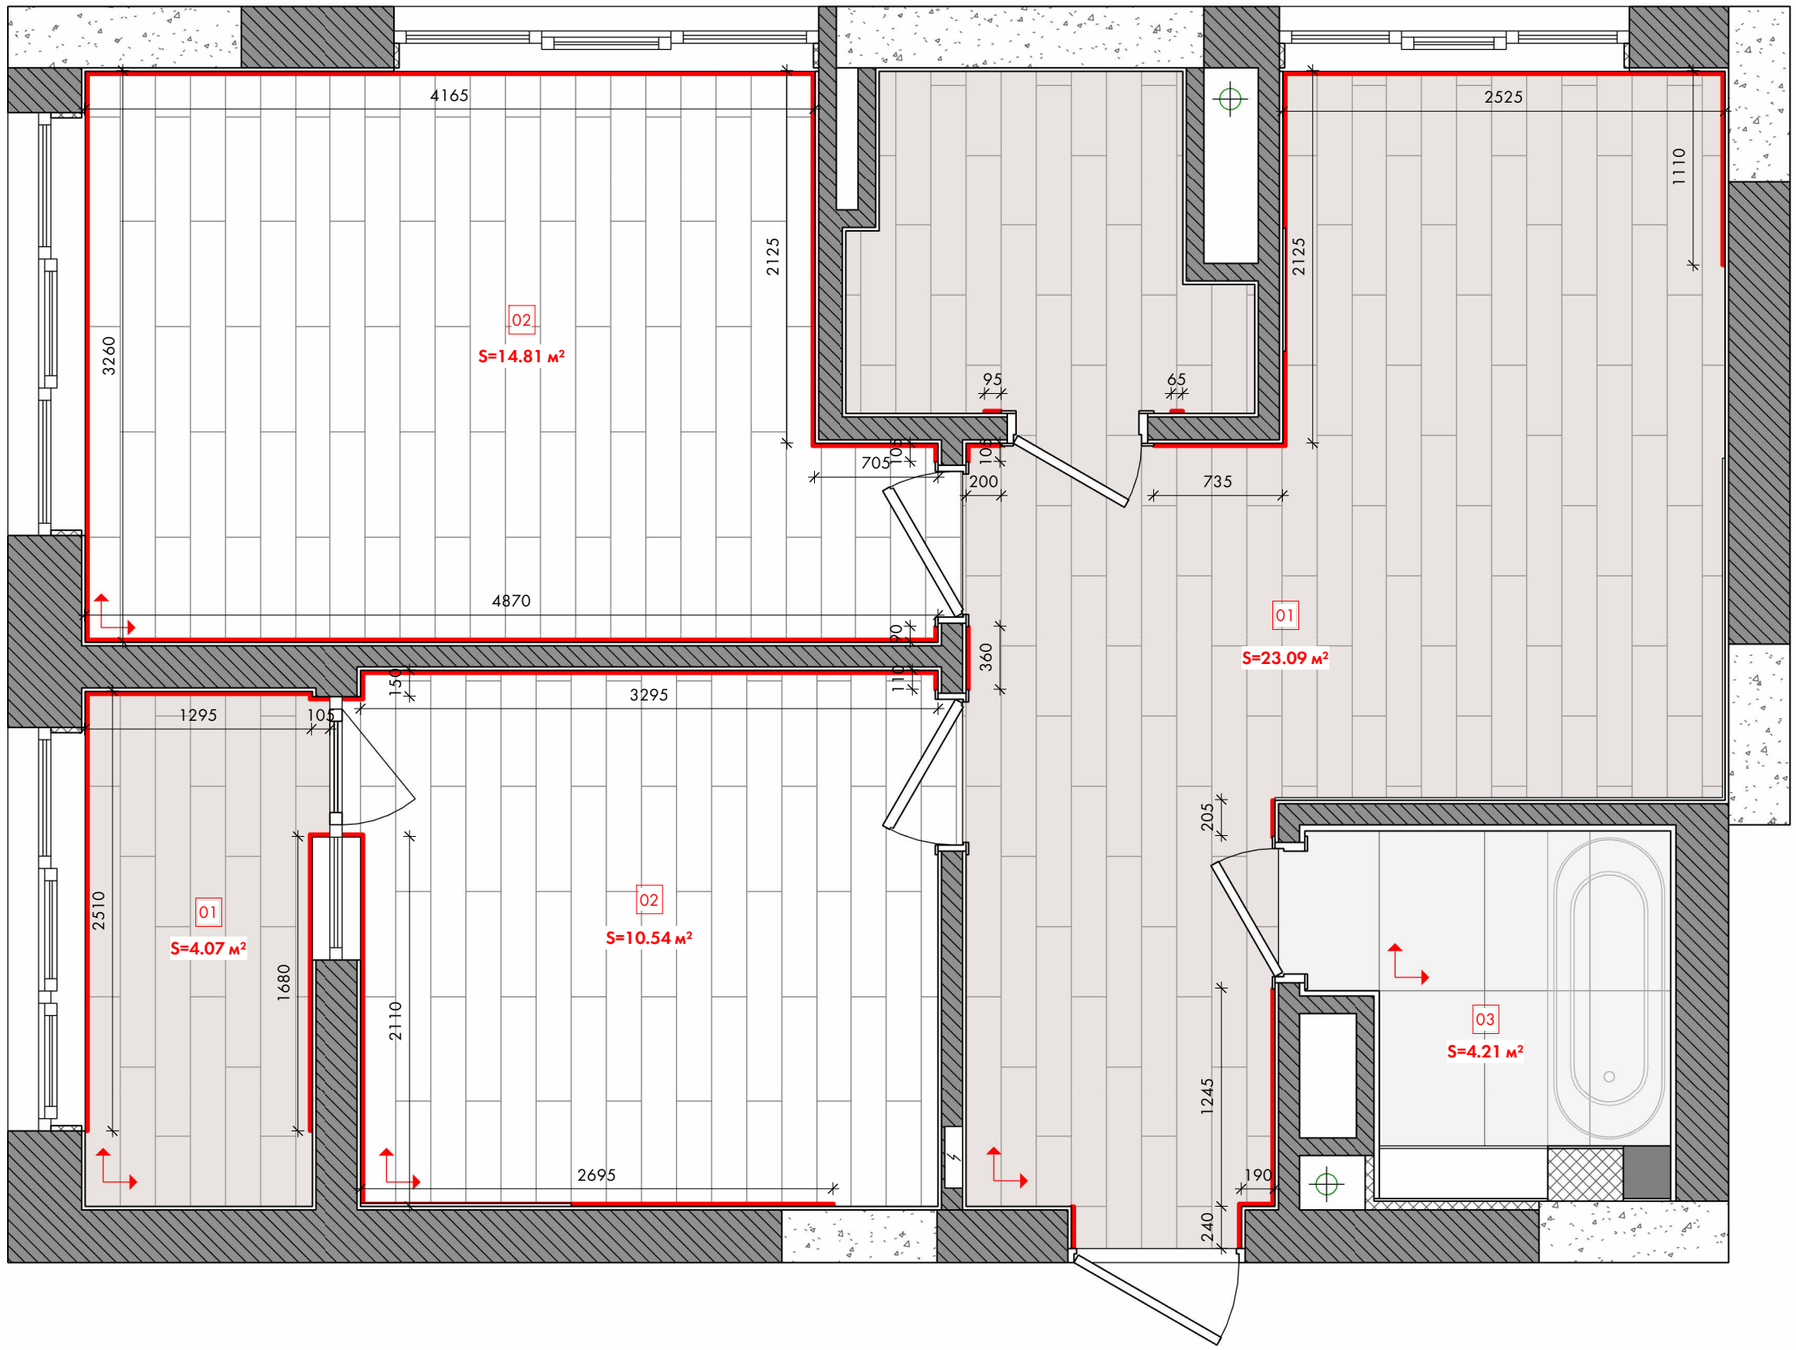

УМОВНІ ПОЗНАЧЕННЯ:

01 - тип покриття

- існуюче покриття підлоги

EQ - еквівалентний (рівнозначний) розмір

- напрям розкладки підлогових покриттів

- плінтус (стіна/підлога)

ПРИМІТКИ:

1. Всі розміри уточнити по місцю.
2. Всі висоти надані від чистового рівня підлоги.
3. Площа підлогових покриттів вказана без запасу та % на підрізку.
4. Загальну довжину плінтуса уточнити на місці перед монтажем.
5. Шов між плитками — 1мм.
6. Стик між покриттями 9мм, заповнюється корковим компенсатором 10мм.
7. Стик покриттів у дверних отворах виконувати в 2х см від сторони відкривання дверей.

Специфікація підлогових покриттів

№	Тип	Площа
01	Плитка керамічна	27.16 м²
02	Ламінат	25.36 м²
03	Плитка 1200x200 мм	4.21 м²


Специфікація плінтусі

Тип	Довжина, м.п.
Плінтус	39.06

SMIRNOVA
INTERIOR DESIGN

Назва проєкту:	Квартира
Адреса проєкту:	вул.Вавілових 11, кв.216

План підлог
А-28

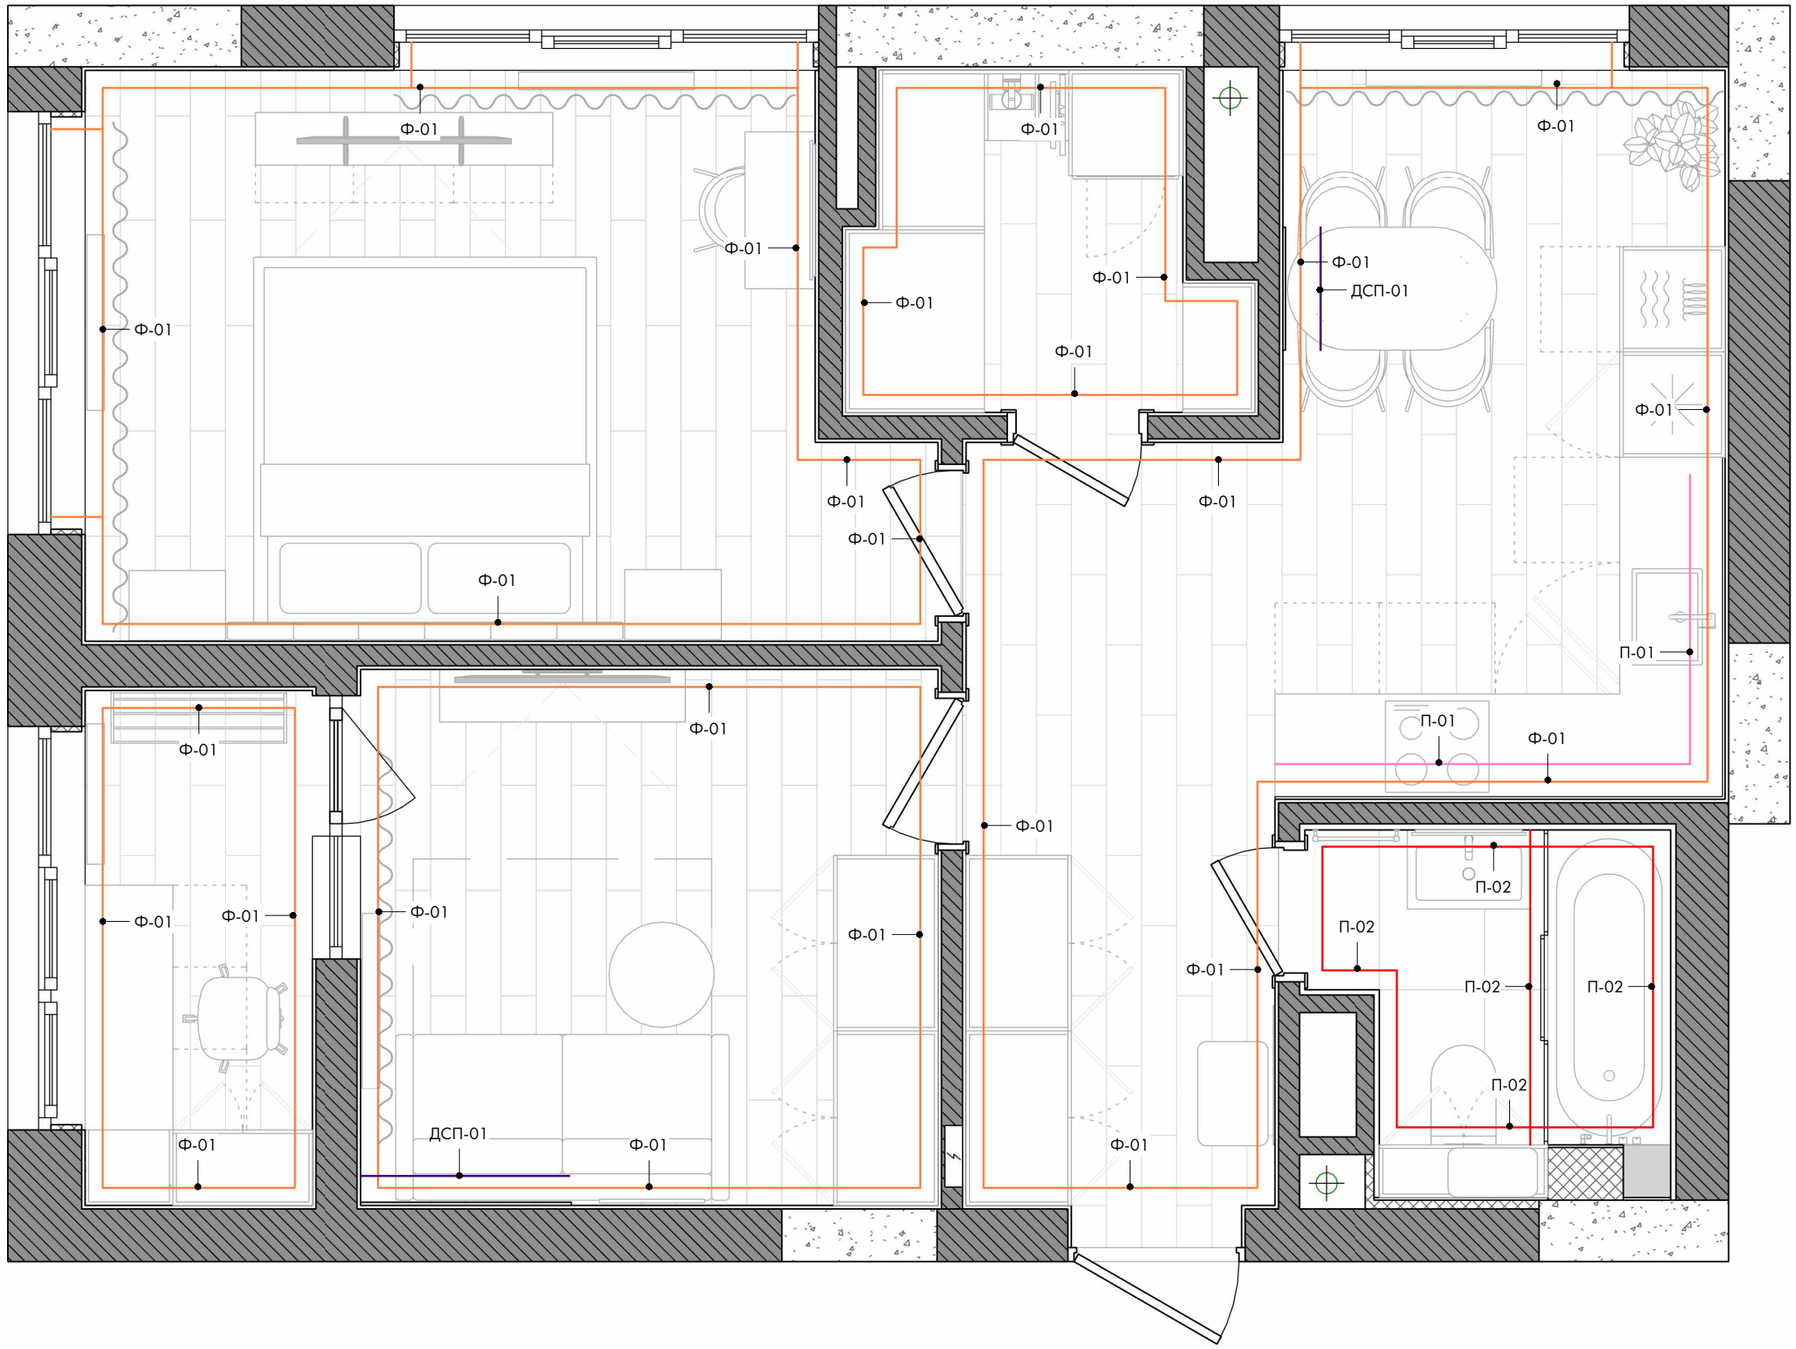

Специфікація оздоблювальних матеріалів стін

УП	№	Оздоблення	Площа
	ДСП-01	ДСП панелі	4.86 м²
	П-01	Плитка 1200х600мм(фартух)	2.70 м²
	П-02	Плитка 1200х600мм(санвузол)	18.98 м²
	Ф-02	Фарбування	140.82 м²

ПРИМІТКИ:

1. Площі покриттів вказані без запасу.
2. Дивитись аркуш разом із розгортками, специфікацією матеріалів та візуалізаціями.
3. Всі відкоси фарбуються в колір стін.


Специфікація приміщень

№	Назва	Площа
1	Передпокій	4.05 м²
2	Кімната	10.06 м²
3	Лоджія	3.81 м²
4	Спальня	14.38 м²
5	Гардеробна	3.88 м²
6	Кухня-вітальня	14.15 м²
7	Санвузол	2.30 м²
Загальна площа:		52.62 м²

SMIRNOVA
INTERIOR DESIGN

Назва проєкту:	Квартира
Адреса проєкту:	вул.Вавілових 11, кв.216

План оздоблювальних матеріалів стін
А-29

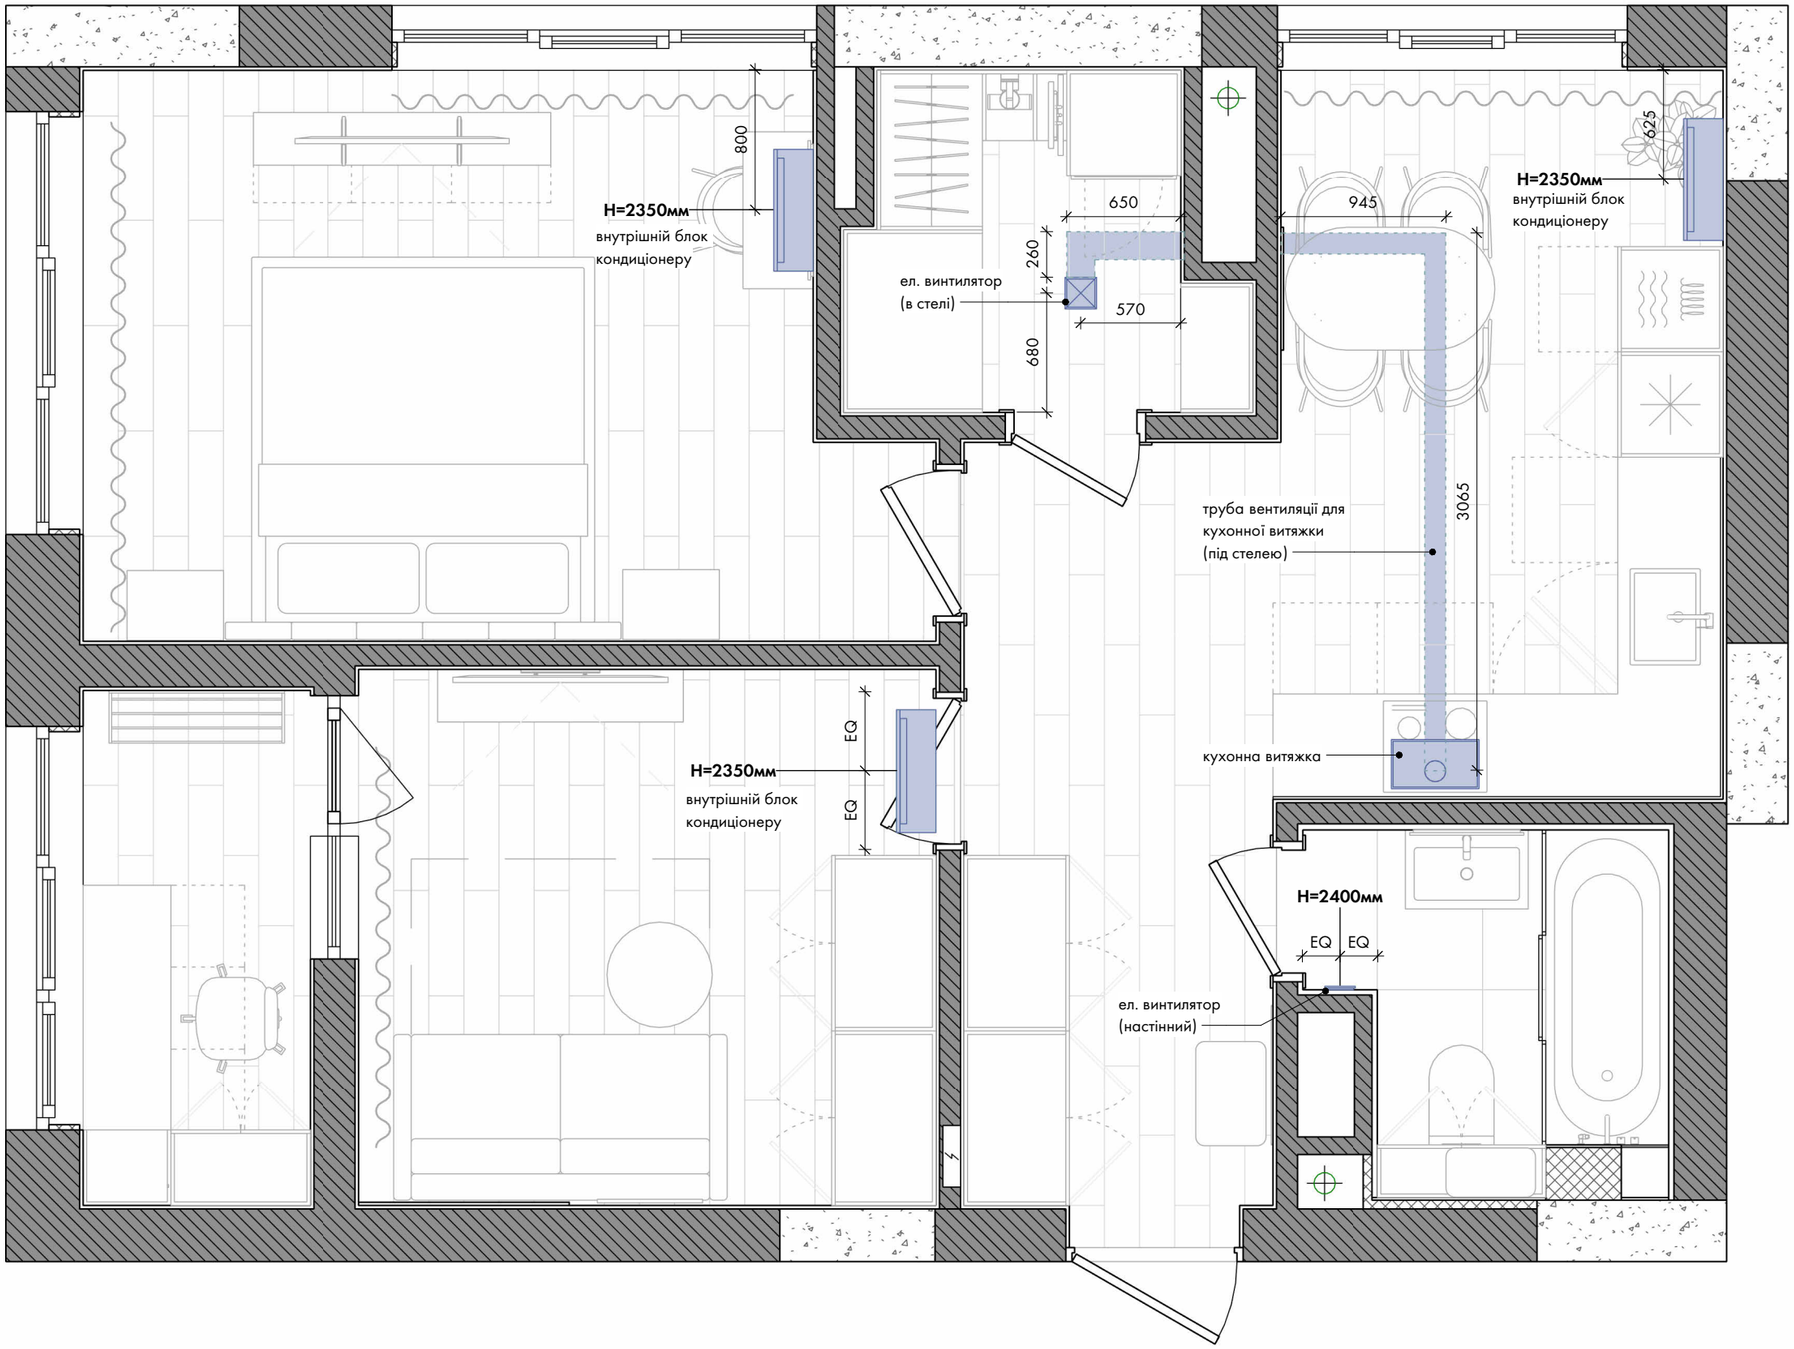

УМОВНІ ПОЗНАЧЕННЯ:

- внутрішній блок кондиціонеру

- електровентилятор

Вентиляційний дифузор прихованого монтажу



Приклад відведення повітропроводу
від кухонної витяжки




ПРИМІТКИ:

1. Всі розміри уточнити на місці.
2. Всі розміри вказані з урахуванням оздоблювальних матеріалів.
3. Всі висоти надані від чистового рівня підлоги.
4. Примусову вентиляцію в гардеробі встановити максимально притискаючись до стелі.
5. На електровентилятор в с/в встановити окрему клавішу вмк./вимик. (див. листи груп світла). В с/в настінна ел.вентилятор.
6. Точну схему прокладання вентиляційного відведення узгодити з профільним спеціалістом.
7. Розміщення зовнішніх блоків кондиціонеру визначити по місцю.
8. Вивід дренажного шлангу від кондиціонера визначити по місцю.
9. Прокладку трас і дренажних шлангів від кондиціонера узгодити зі спеціалістом монтажником.
10. План вентиляції дан схематично, узгодити з профільним спеціалістом.
11. Дивитись лист разом з розгортками.
12. Відведення від кухонної витяжки зробити максимально притискаючись до плити перекриття над стелею.
13. Точне місце виведення повітроводу для кухонної витяжки визначити після погодження з фірмою виробником кухні.

SMIRNOVA
INTERIOR DESIGN

Назва проєкту:	Квартира
Адреса проєкту:	вул.Вавілових 11, кв.216

План вентиляції та кондиціонування
А-30

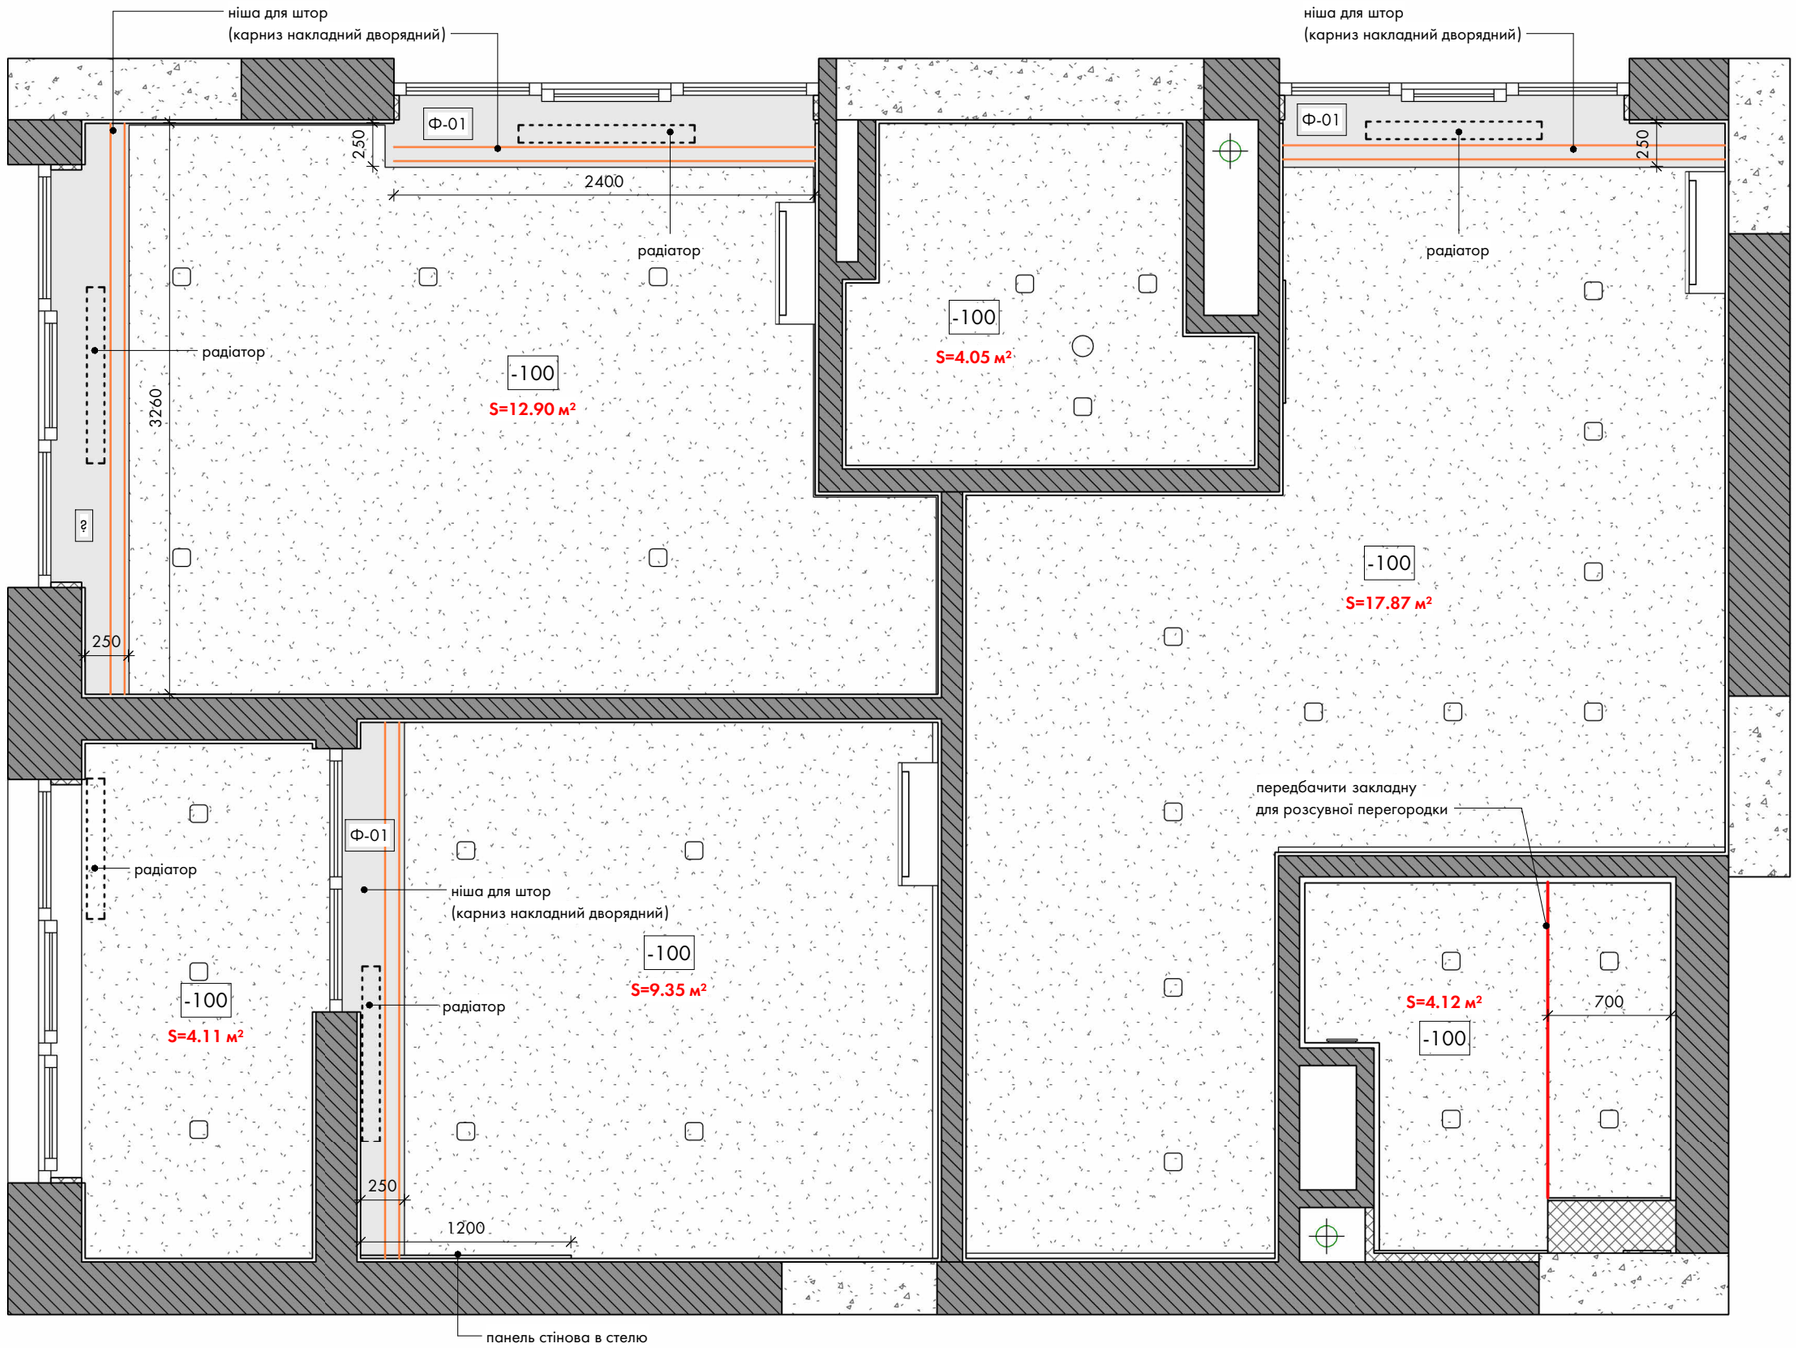

УМОВНІ ПОЗНАЧЕННЯ:

- натяжна стеля
- підшивка ГК 1лист+фарбування ніші для штор
- карниз накладний дворядний
- закладна для душового скла

ПРИМІТКИ:

1. Всі розміри уточнити по місцю.
2. Всі розміри вказані з урахуванням оздоблювальних матеріалів.
3. Дивитись аркуш разом зі схемою вентиляції.

Специфікація оздоблення стель

№	Оздоблення	Площа
Ф-01	Фарбування ніш	5.14 м²

SMIRNOVA
INTERIOR DESIGN

Назва проєкту:	Квартира
Адреса проєкту:	вул.Вавілових 11, кв.216

План стель

А-31



УМОВНІ ПОЗНАЧЕННЯ:

	Вивід 12V	5
	Вимикач місцевий 1-клавішний	10
	Вимикач місцевий 2-клавішний	2
	Вимикач перехресний 1-клавішний	6
	Вимикач прохідний 1-клавішний	2
	Майстер вимикач	1
C-01	-маркування типів світильників	
	-LED-підсвітка 2700K	
EQ	-еквівалентний/рівнозначний розмір	


ПРИМІТКИ:

1. Всі розміри уточнити по місцю.
2. Всі розміри вказані з урахуванням оздоблювальних матеріалів.
3. Всі висоти надані від чистового рівня підлоги.
4. Висота вимикачів H=900мм від у.ч.п., окрім тих, що з виносками.
5. Дивитись аркуш разом з планом груп світла, планом стель та розгортками.
6. Підсвітка для кухонних шаф та інших меблів з використанням світлодіодної ленти поставляється разом із меблями фірмою виробником.
7. Дивитись лист разом з планом розміщення освітлення, планом стель ,розгортками,та специфікацією освітлення.

SMIRNOVA
INTERIOR DESIGN

Назва проєкту:	Квартира
Адреса проєкту:	вул.Вавілових 11, кв.216

План розміщення освітлювальних приладів
A-32

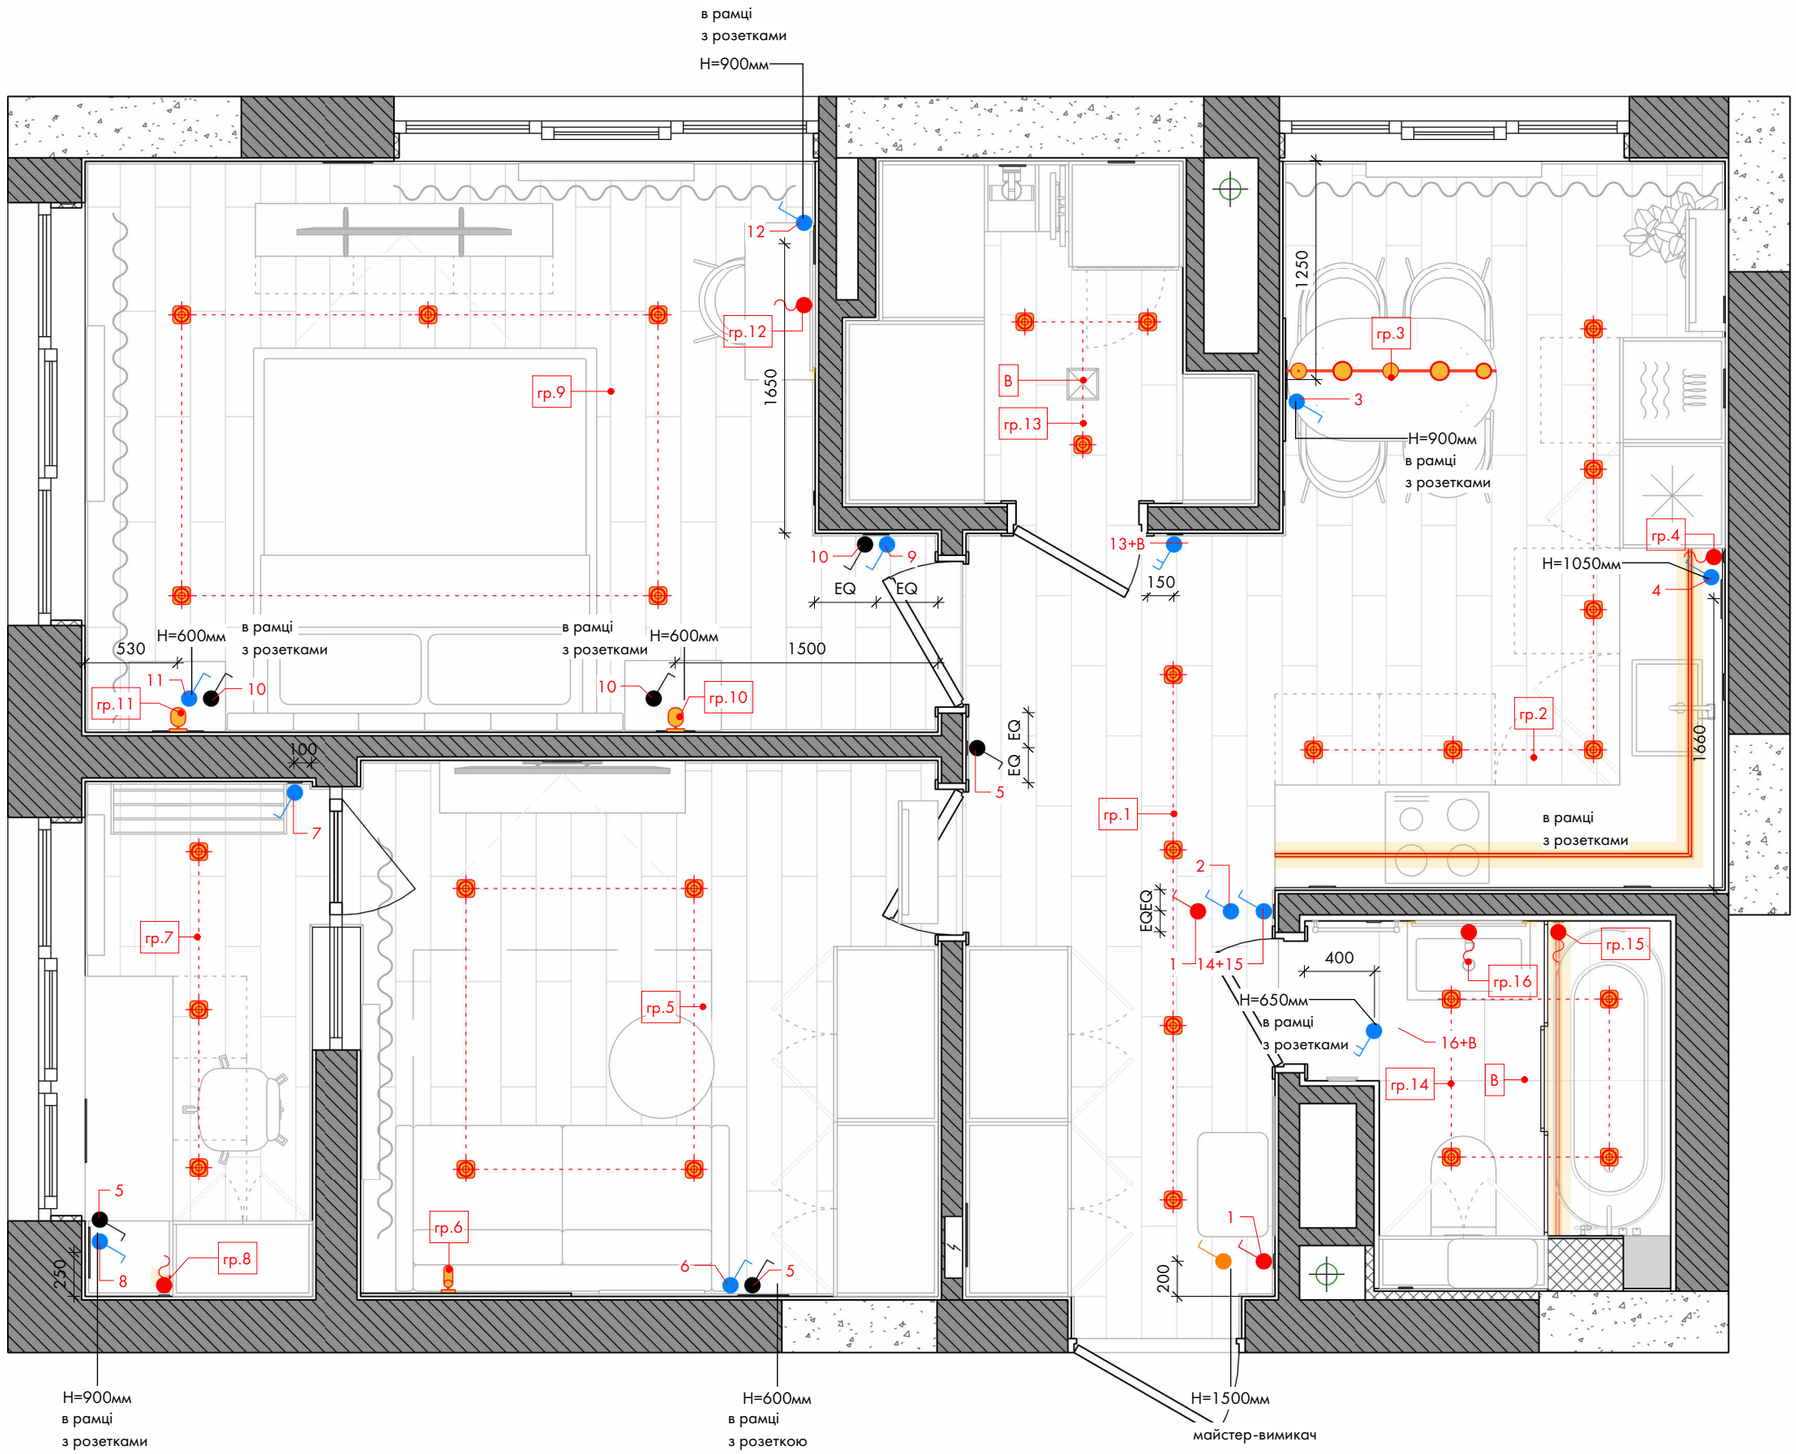

УМОВНІ ПОЗНАЧЕННЯ:

	Вивід 12V	5
	Вимикач місцевий 1-клавішний	10
	Вимикач місцевий 2-клавішний	2
	Вимикач перехресний 1-клавішний	6
	Вимикач прохідний 1-клавішний	2
	Майстер вимикач	1
гр.1	-нумерація груп світла	
1...	-нумерація груп світла	
	-LED-підсвітка 2700K	
EQ	-еквівалентний/рівнозначний розмір	


ПРИМІТКИ:

1. Всі розміри уточнити по місцю.
2. Всі розміри вказані з урахуванням оздоблювальних матеріалів.
3. Всі висоти надані від чистового рівня підлоги.
4. Висота вимикачів H=900мм від у.ч.п., окрім тих, що з виносками.
5. Дивитись аркуш разом з планом груп світла, планом стель та розгортками.
6. Підсвітка для кухонних шаф та інших меблів з використанням світлодіодної ленти поставляється разом із меблями фірмою виробником.
7. Дивитись лист разом з планом розміщення освітлення, планом стель ,розгортками,та специфікацією освітлення.

SMIRNOVA
INTERIOR DESIGN

Назва проєкту:	Квартира
Адреса проєкту:	вул.Вавілових 11, кв.216

План груп світла й вимикачів
А-33

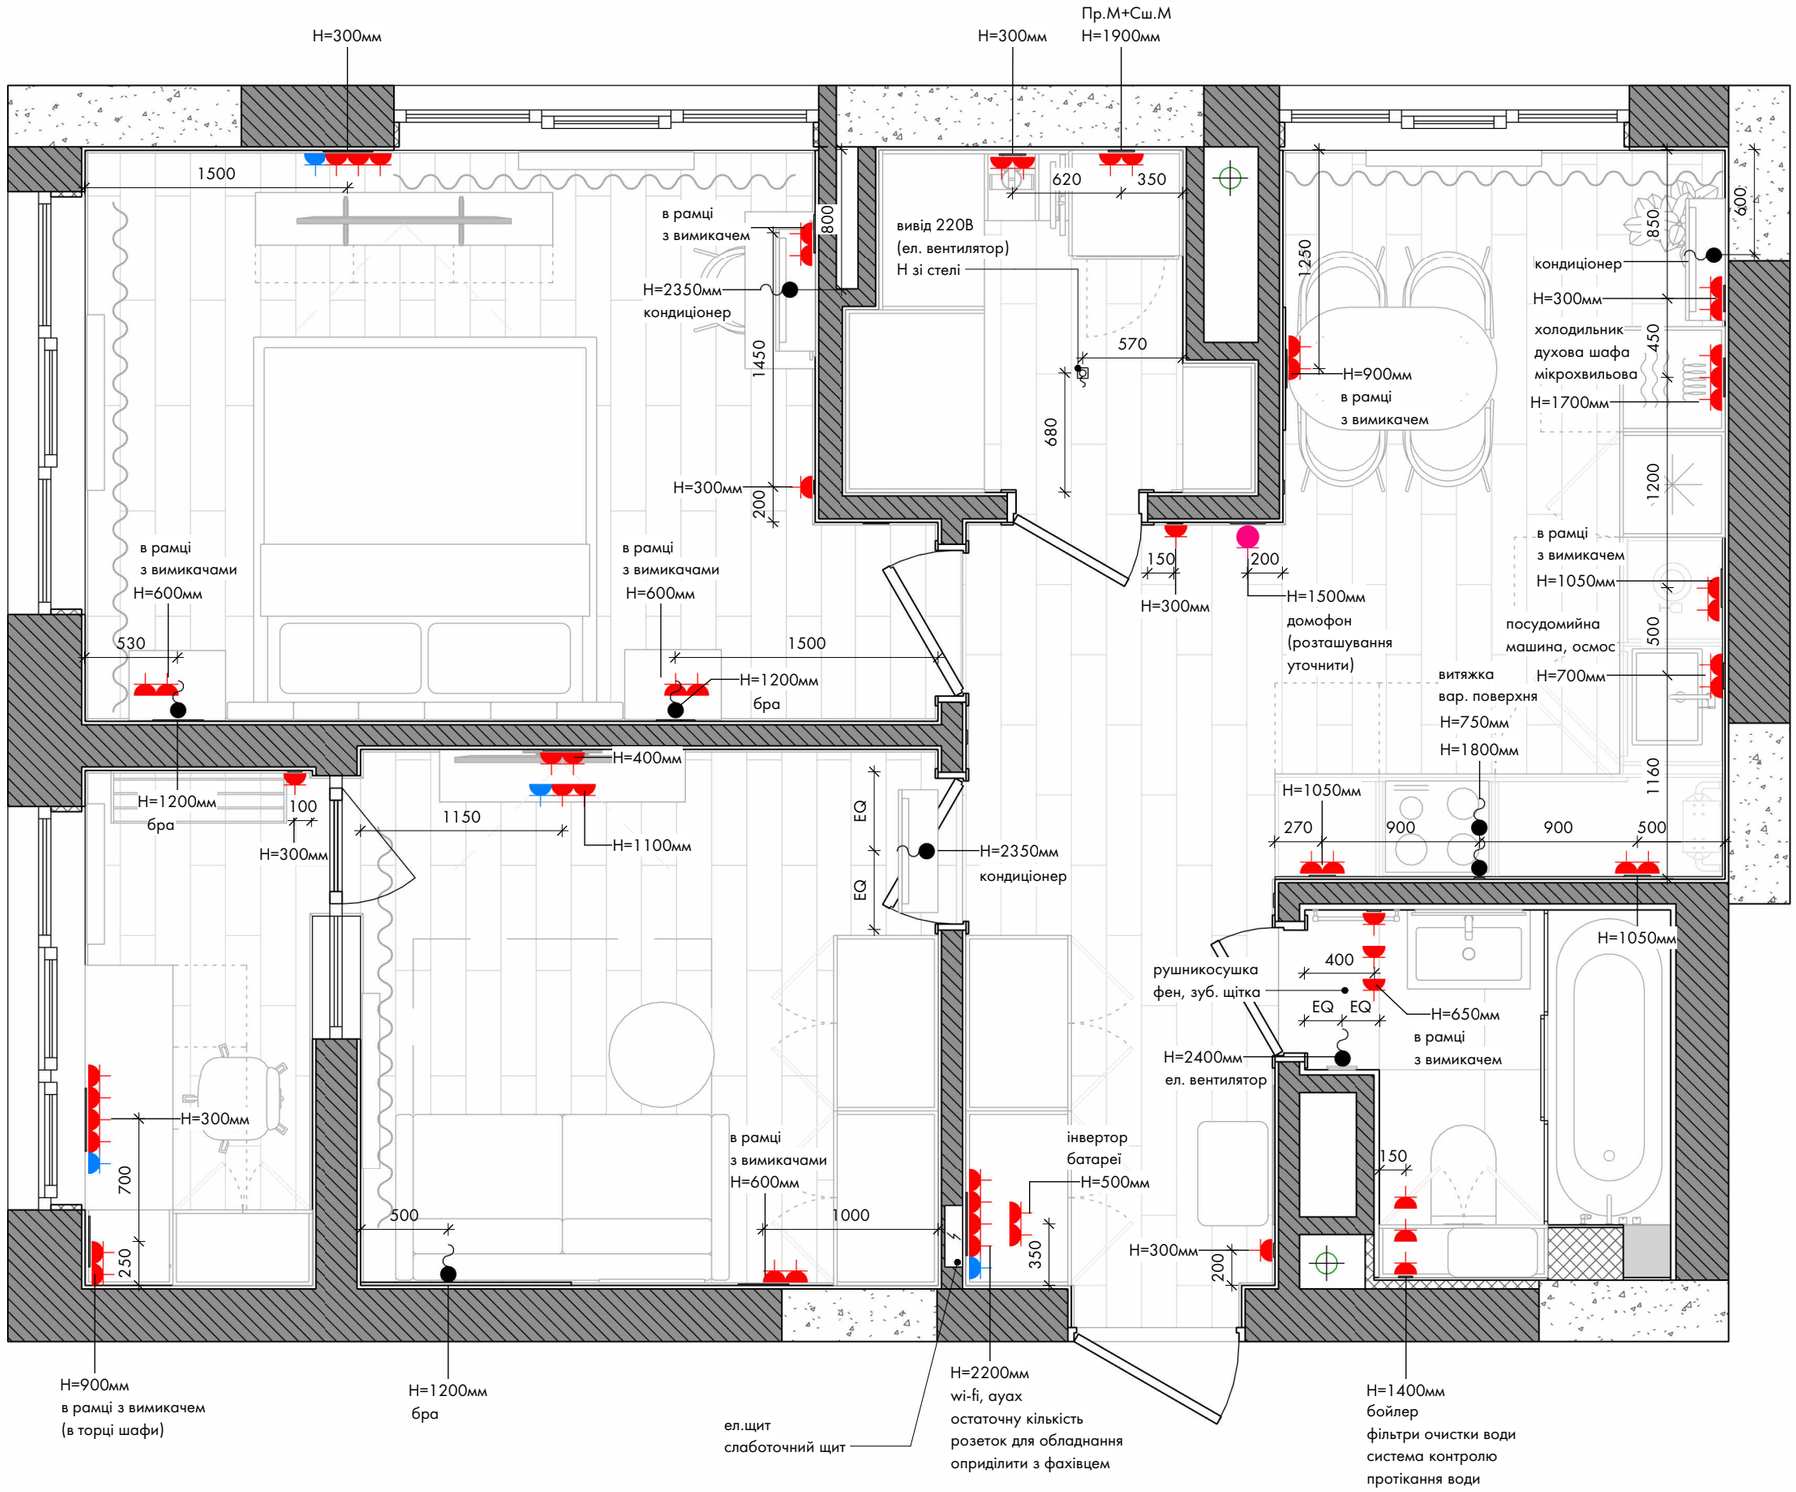

УМОВНІ ПОЗНАЧЕННЯ:

Вивід 220V	10
Домофон	1
Розетка 220V	57
Розетка INT	4

ПРИМІТКИ:

1. Всі розміри уточнити по місцю.
2. Всі розміри вказані з урахуванням оздоблювальних матеріалів.
3. Всі висоти надані від чистового рівня підлоги.
4. Висота розеток Н=300мм від у.ч.п., окрім тих, що з виносками.
5. Дивитись аркуш разом з розгортками.

SMIRNOVA
INTERIOR DESIGN

Назва проєкту:	Квартира
Адреса проєкту:	вул.Вавілових 11, кв.216

План розеток та електровиводів
А-34


СПЕЦИФІКАЦІЯ ОСВІТЛЮВАЛЬНИХ ПРИЛАДІВ

№	Тип	Зображення	Характеристики	Кількість
С-01	Точкові світильники			29
С-02	Бра			1
С-03	Бра (спальня)			2
С-04	Люстра			1
С-41	Lighting_square			1
С-61	Lighting_round			1

СПЕЦИФІКАЦІЯ ЕЛЕКТРОФУРНІТУРИ

Назва	Кількість
Вимикач місцевий 1-клавішний	10
Вимикач місцевий 2-клавішний	2
Вимикач перехресний 1-клавішний	6
Вимикач прохідний 1-клавішний	2
Майстер вимикач	1
Вимикачі	21
Рамка 1х	14
Рамка вертикальна 3х	2
Рамка вертикальна 4х	1
Рамка горизонтальна 2х	9
Рамка горизонтальна 3х	6
Рамка горизонтальна 4х	4
Рамка горизонтальна 5х	2
Рамки	38
Розетка 220V	57
Розетка INT	4
Розетки	61
Терморегулятор	4
Терморегулятори	4

СПЕЦИФІКАЦІЯ LED-ПРОФІЛЮ

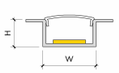Профіль	Тип	Довжина ,м.п.
	Profile built in 15x7	7.74


ПРИМІТКИ:

1. Дивитись аркуш разом із планами освітлення.

SMIRNOVA
INTERIOR DESIGN

Назва проєкту:	Квартира
Адреса проєкту:	вул.Вавілових 11, кв.216

Специфікації освітлення та електрофурнітури
А-35

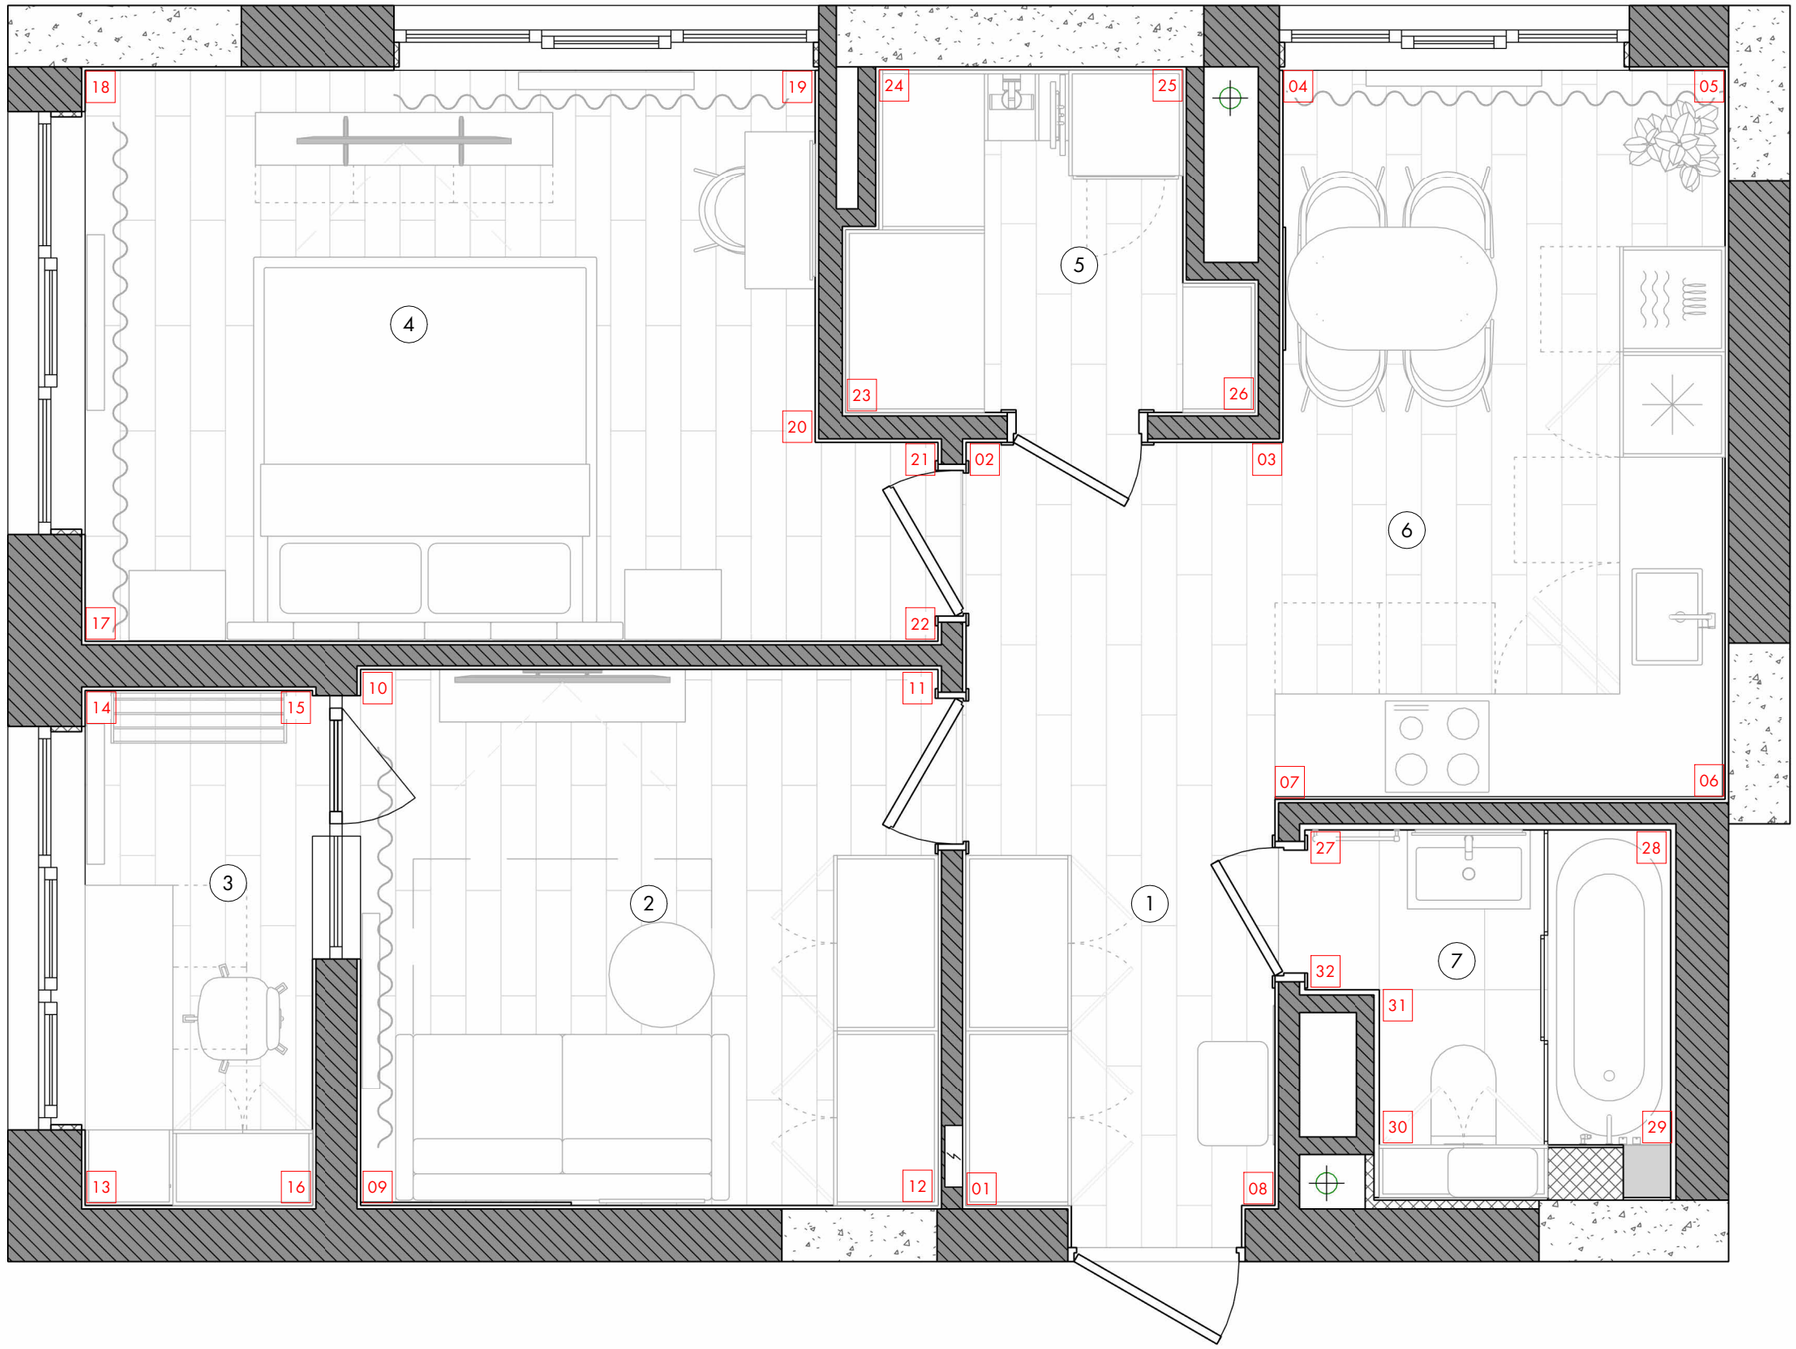

ПРИМІТКИ:

1. Дивитись аркуш разом з розгортками.


Специфікація приміщень

№	Назва	Площа
1	Передпокій	4.05 м²
2	Кімната	10.06 м²
3	Лоджія	3.81 м²
4	Спальня	14.38 м²
5	Гардеробна	3.88 м²
6	Кухня-вітальня	14.15 м²
7	Санвузол	2.30 м²
Загальна площа:		52.62 м²

SMIRNOVA
INTERIOR DESIGN


Назва проєкту:	Квартира
Адреса проєкту:	вул.Вавілових 11, кв.216

План розгорток
А-36

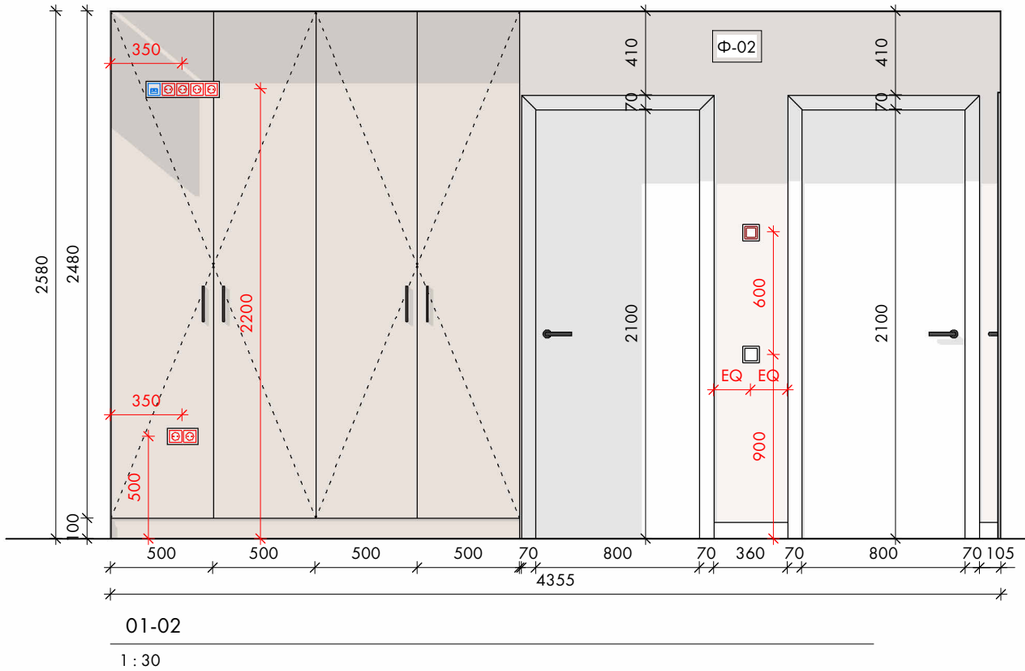


01-02


1 : 30

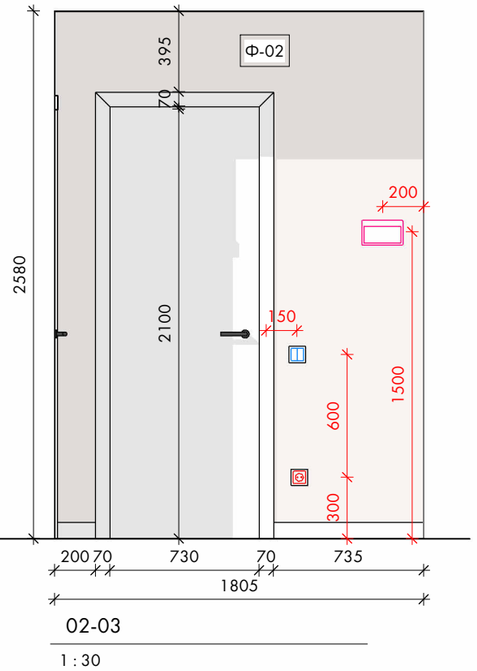

02-03

1 : 30

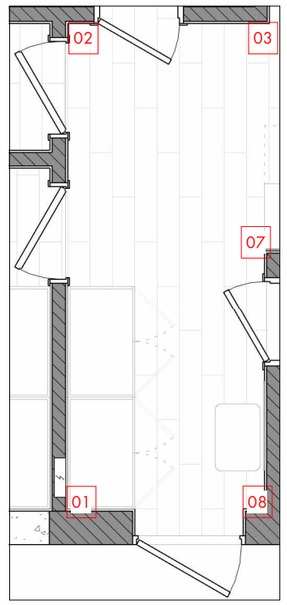

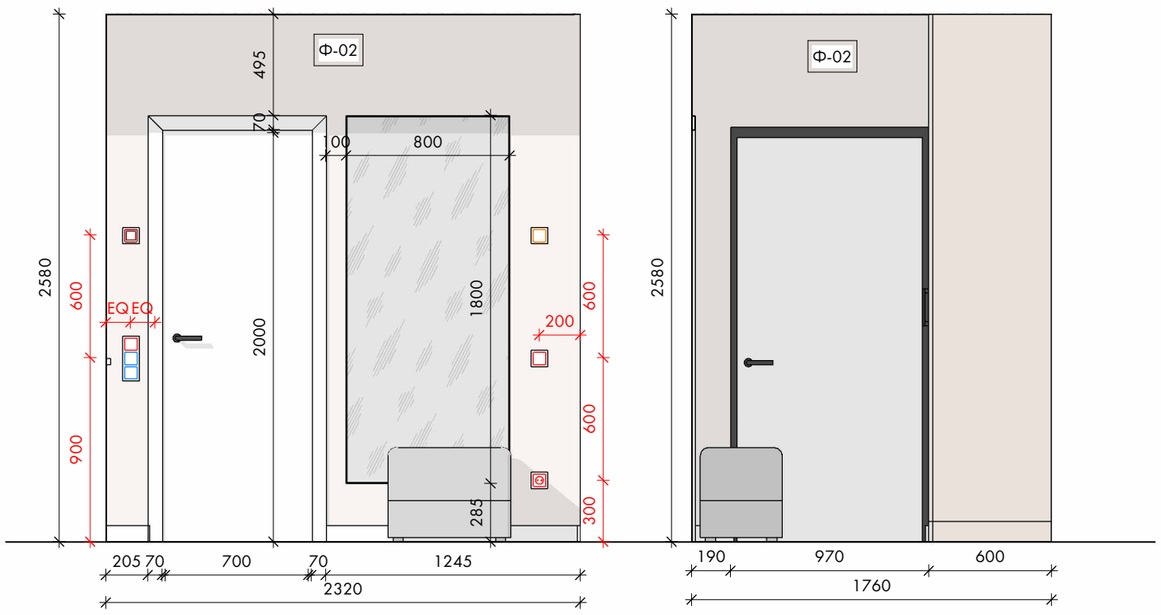


07-08

1 : 30

08-01

1 : 30

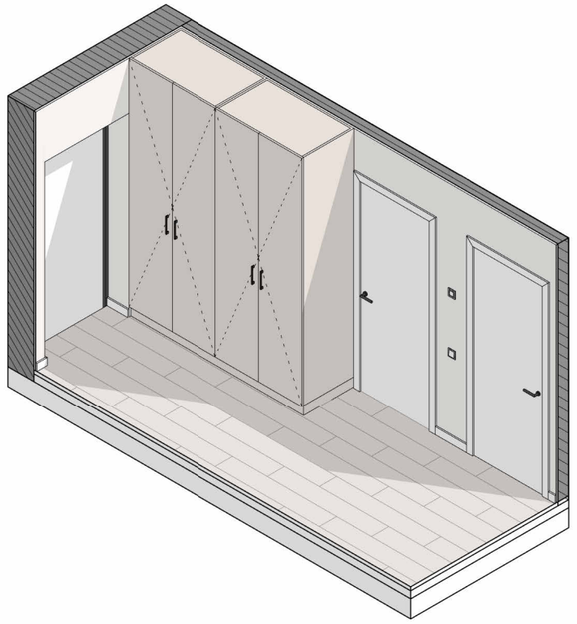

УМОВНІ ПОЗНАЧЕННЯ:

- Вивід 12V
- Вивід 220V
- Вимикач місцевий 1-клавішний
- Вимикач місцевий 2-клавішний
- Вимикач перехресний 1-клавішний
- Вимикач прохідний 1-клавішний
- Домофон
- Майстер вимикач
- Розетка 220V
- Розетка INT
- Терморегулятор

EQ — Еквівалентний (рівнозначний) розмір

Напрям розкладки плитки

Оздоблювальні матеріали

ДСП-01	ДСП панелі	4.86 м²
П-01	Плитка 1200x600мм(фартух)	2.70 м²
П-02	Плитка 1200x600мм(санвузол)	18.98 м²
Ф-02	Фарбування	140.82 м²

ПРИМІТКИ:


1. Всі розміри уточнити по місцю.
2. Всі розміри вказані з урахуванням оздоблювальних матеріалів.
3. Всі висоти надані від чистового рівня підлоги.
4. Дивитись аркуш разом з планами сантехніки, електрики, вентиляції та кондиціювання.

SMIRNOVA
INTERIOR DESIGN

Назва проєкту:	Квартира
Адреса проєкту:	вул.Вавілових 11, кв.216


Розгортка передпокою

А-37

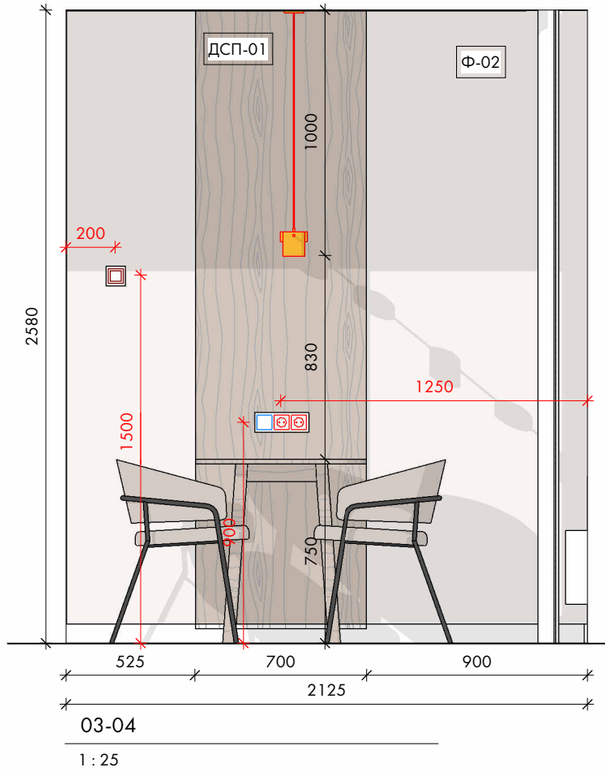


03-04


1 : 25

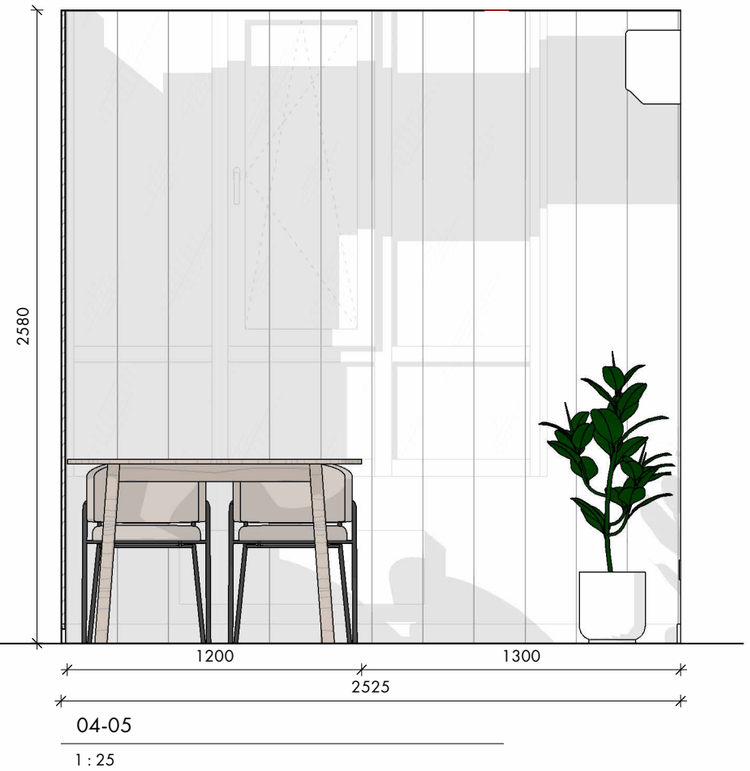

04-05


1 : 25

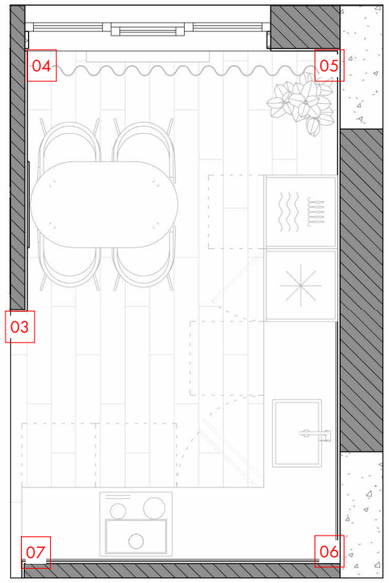

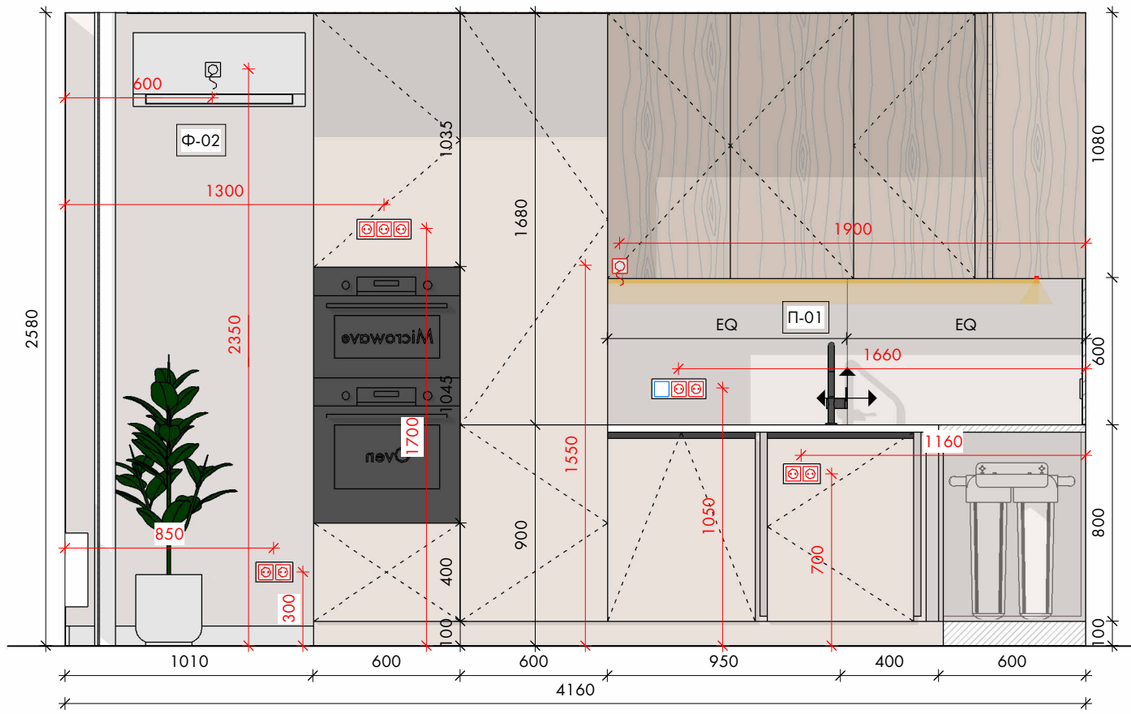

05-06

1 : 25

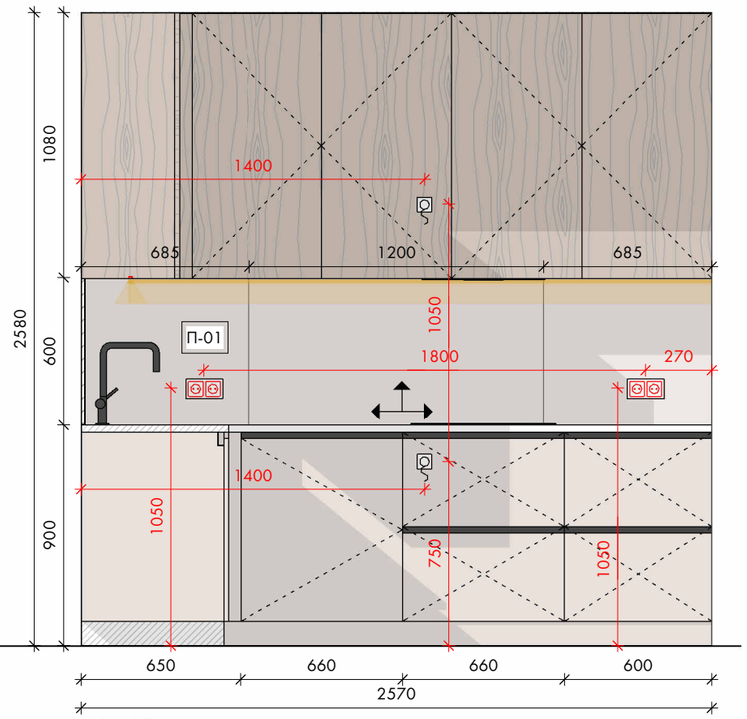

06-07

1 : 25

УМОВНІ ПОЗНАЧЕННЯ:

- Вивід 12V
- Вивід 220V
- Вимикач місцевий 1-клавішний
- Вимикач місцевий 2-клавішний
- Вимикач перехресний 1-клавішний
- Вимикач прохідний 1-клавішний
- Домофон
- Майстер вимикач
- Розетка 220V
- Розетка INT
- Терморегулятор

EQ Еквівалентний (рівнозначний) розмір

Напрям розкладки плитки

Оздоблювальні матеріали

ДСП-01	ДСП панелі	4.86 м²
П-01	Плитка 1200x600мм(фартух)	2.70 м²
П-02	Плитка 1200x600мм(санвузол)	18.98 м²
Ф-02	Фарбування	140.82 м²

ПРИМІТКИ:


1. Всі розміри уточнити по місцю.
2. Всі розміри вказані з урахуванням оздоблювальних матеріалів.
3. Всі висоти надані від чистового рівня підлоги.
4. Дивитись аркуш разом з планами сантехніки, електрики, вентиляції та кондиціювання.

SMIRNOVA
INTERIOR DESIGN

Назва проєкту:	Квартира
Адреса проєкту:	вул.Вавілових 11, кв.216

Розгортка кухні
А-38




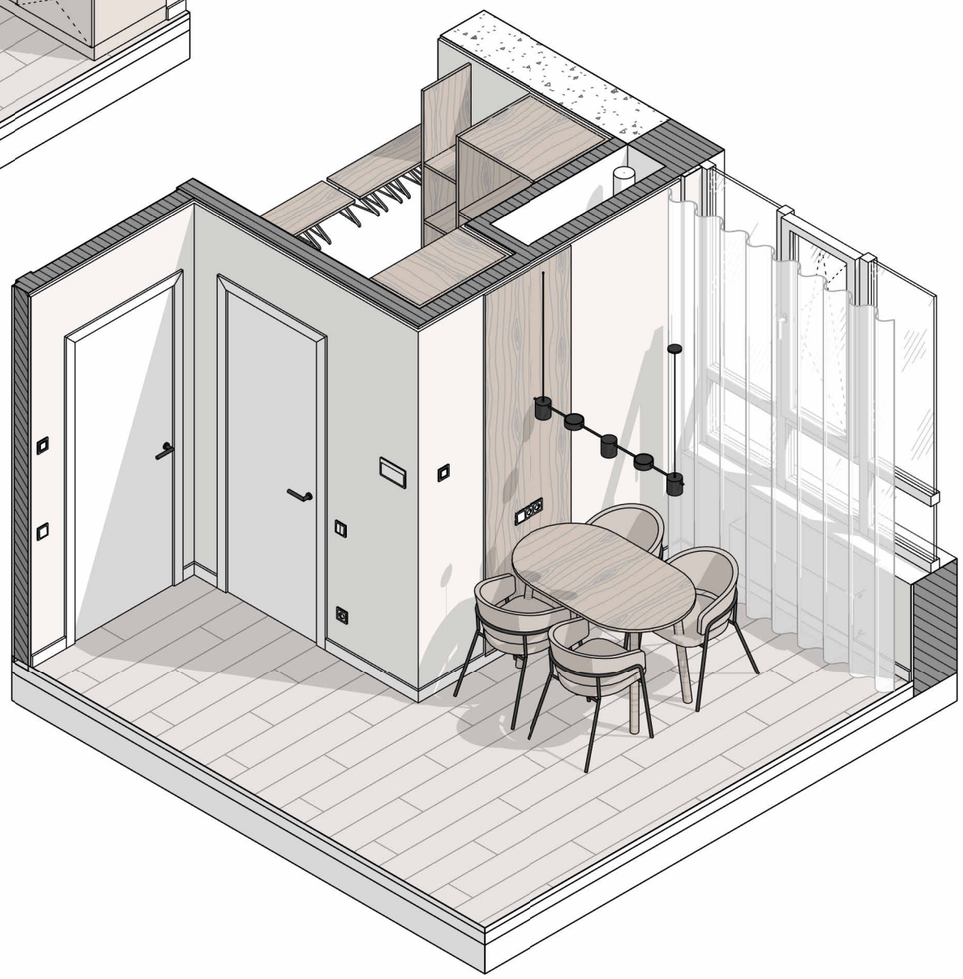

SMIRNOVA
INTERIOR DESIGN


Назва проєкту:	Квартира
Адреса проєкту:	вул.Вавілових 11, кв.216

3D-схема кухні
A-39

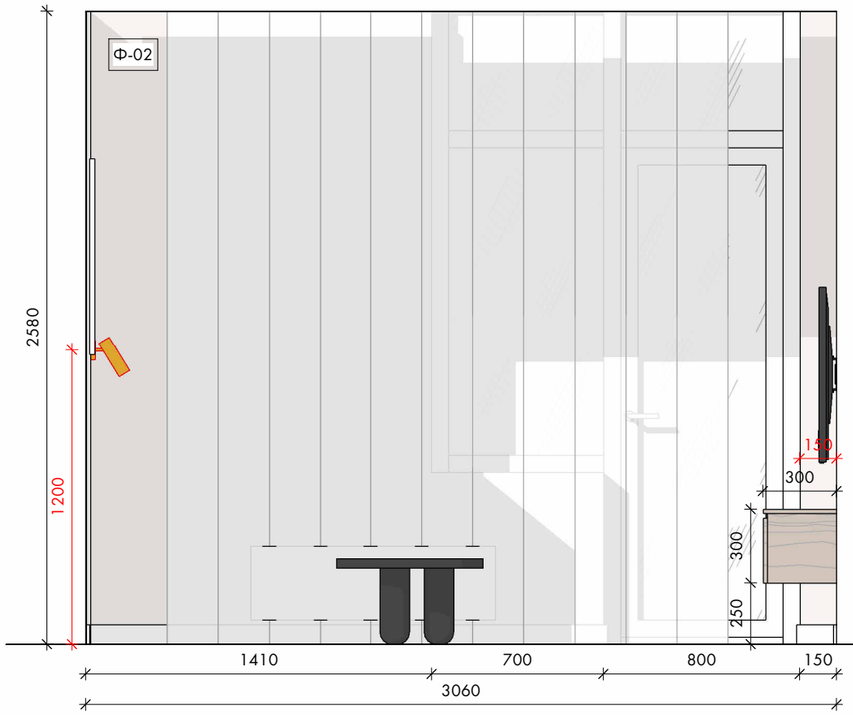


09-10

1 : 25

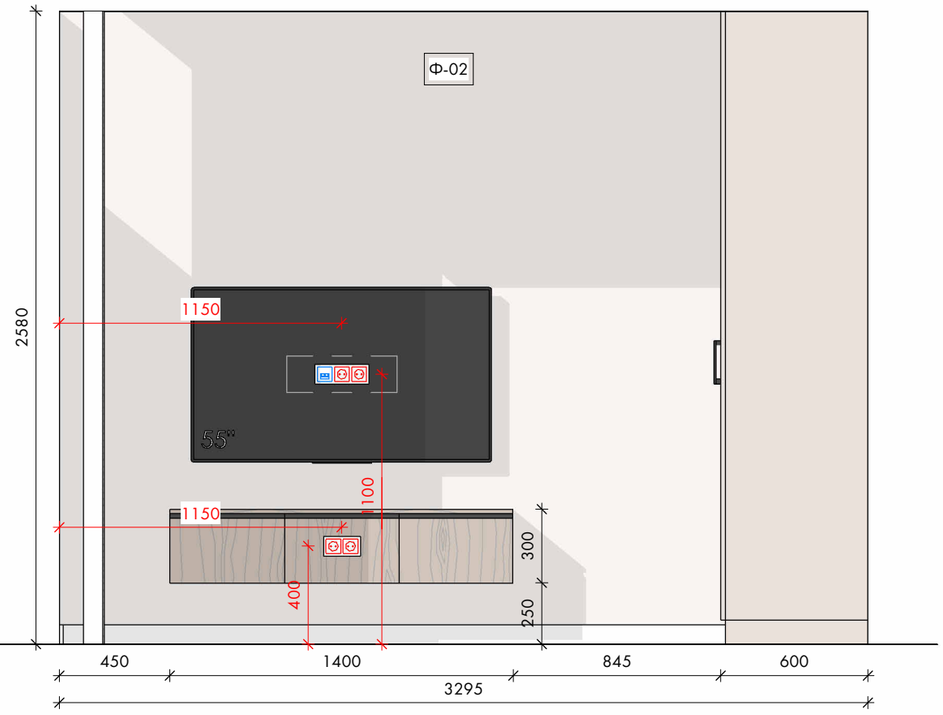


10-11

1 : 25

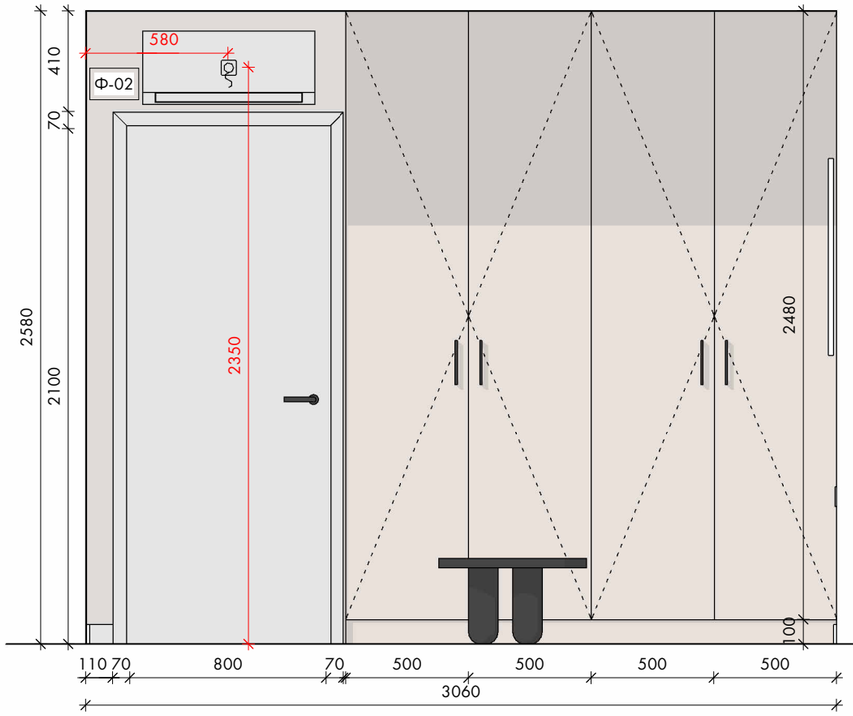

11-12

1 : 25

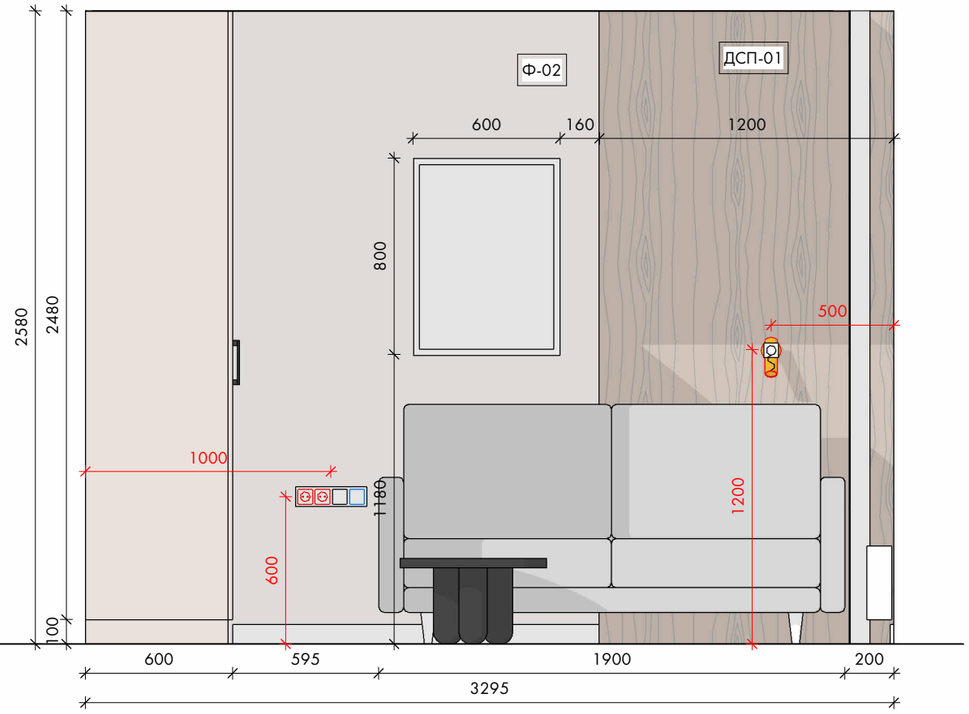

12-09

1 : 25

УМОВНІ ПОЗНАЧЕННЯ:

- Вивід 12V
- Вивід 220V
- Вимикач місцевий 1-клавішний
- Вимикач місцевий 2-клавішний
- Вимикач перехресний 1-клавішний
- Вимикач прохідний 1-клавішний
- Домофон
- Майстер вимикач
- Розетка 220V
- Розетка INT
- Терморегулятор
- EQ Еквівалентний (рівнозначний) розмір
- Напрям розкладки плитки

Оздоблювальні матеріали

ДСП-01	ДСП панелі	4.86 м²
П-01	Плитка 1200x600мм(фартух)	2.70 м²
П-02	Плитка 1200x600мм(санвузол)	18.98 м²
Ф-02	Фарбування	140.82 м²


ПРИМІТКИ:


1. Всі розміри уточнити по місцю.
2. Всі розміри вказані з урахуванням оздоблювальних матеріалів.
3. Всі висоти надані від чистового рівня підлоги.
4. Дивитись аркуш разом з планами сантехніки, електрики, вентиляції та кондиціювання.

SMIRNOVA
INTERIOR DESIGN

Назва проєкту:	Квартира
Адреса проєкту:	вул.Вавілових 11, кв.216

Розгортка кабінету
А-40

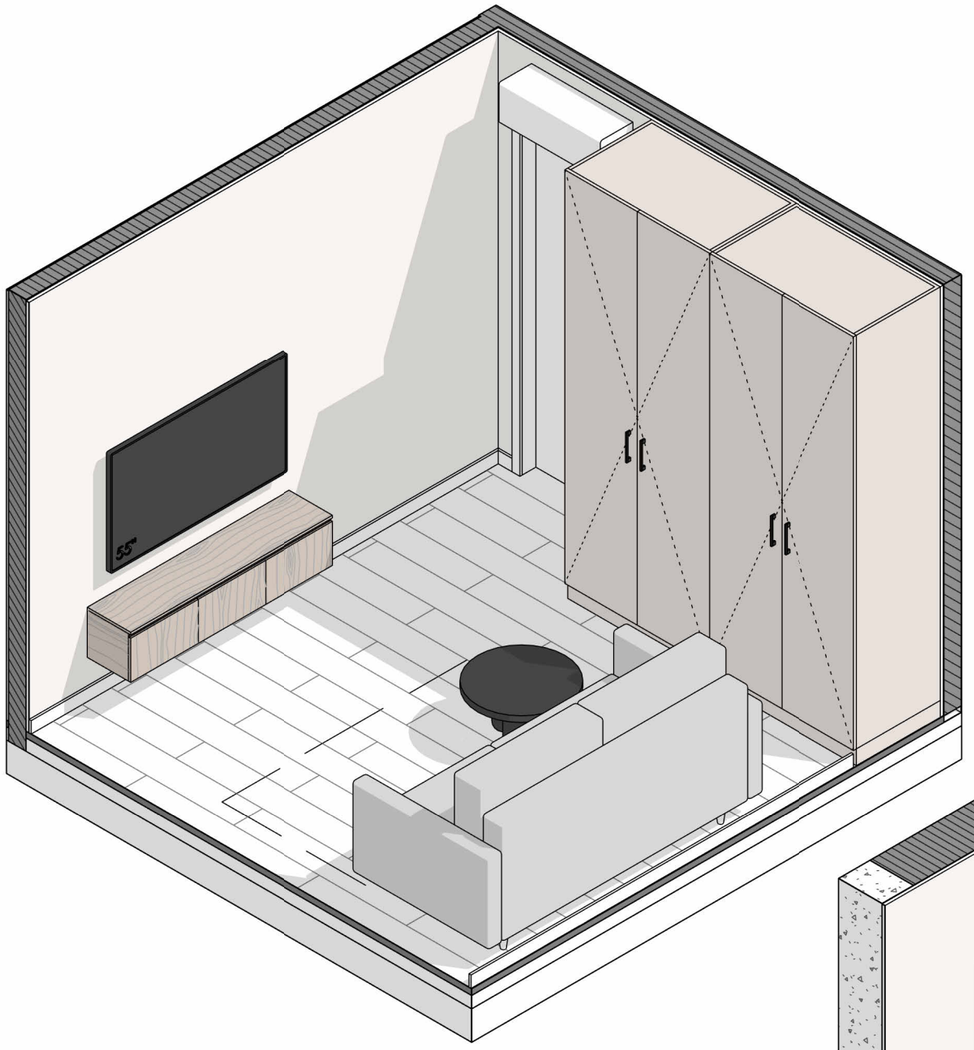


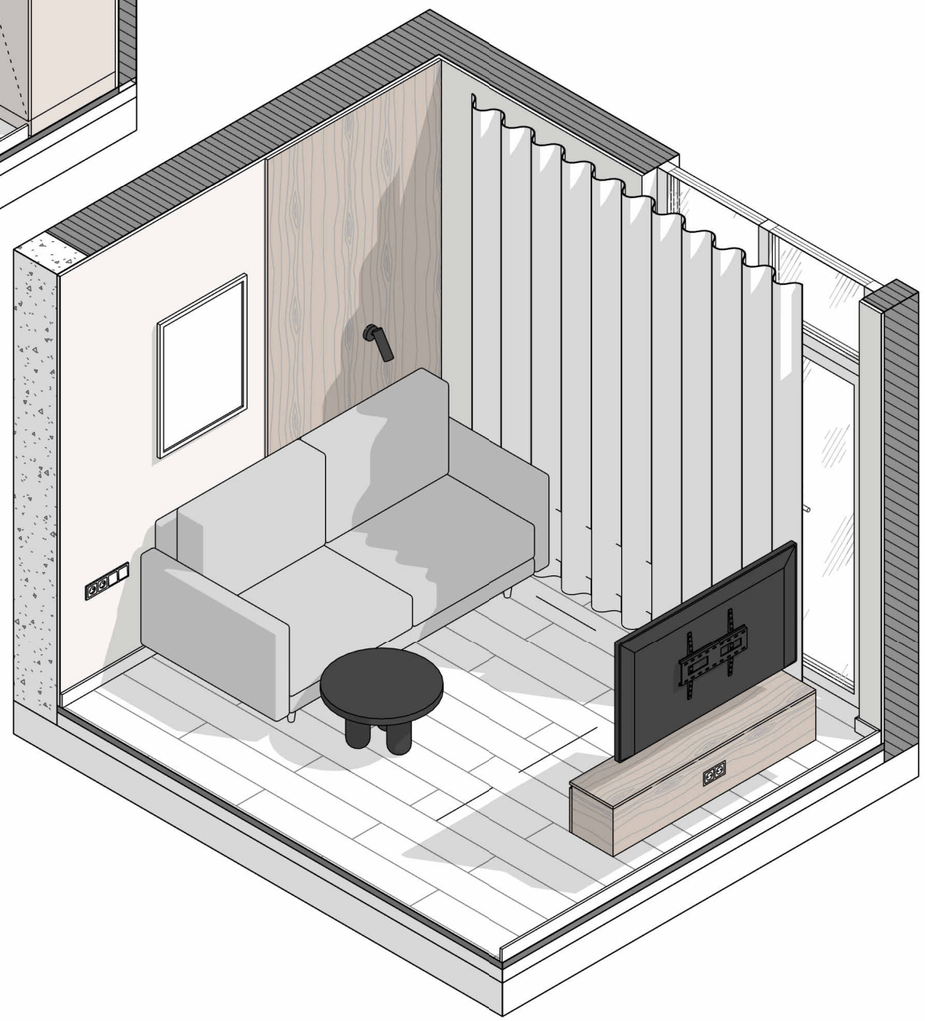

SMIRNOVA
INTERIOR DESIGN


Назва проєкту:	Квартира
Адреса проєкту:	вул.Вавілових 11, кв.216

3D-схема кабінету
А-41

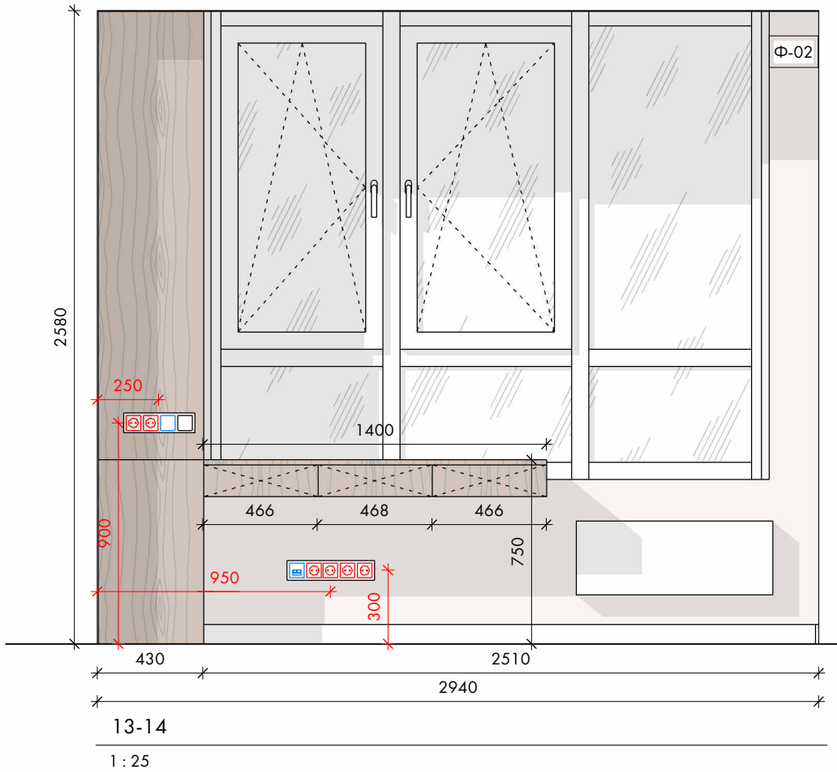


13-14


1 : 25

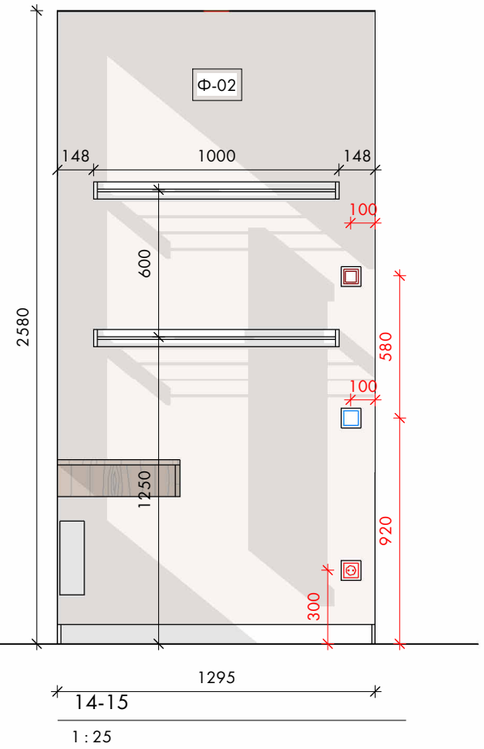

14-15


1 : 25

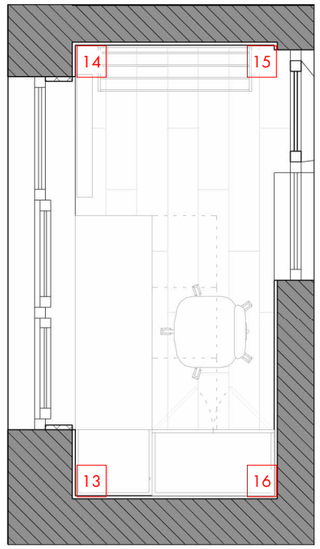

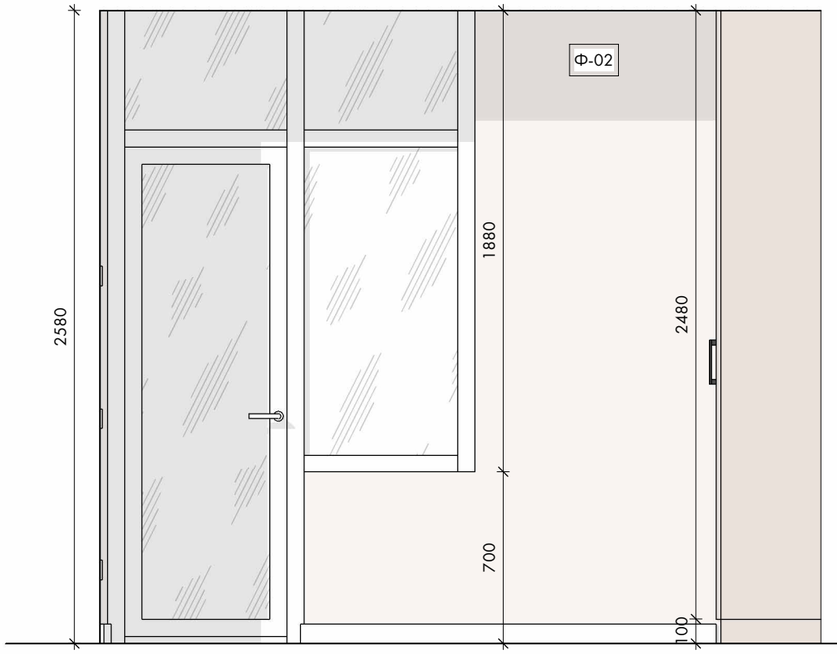


15-16

1 : 25

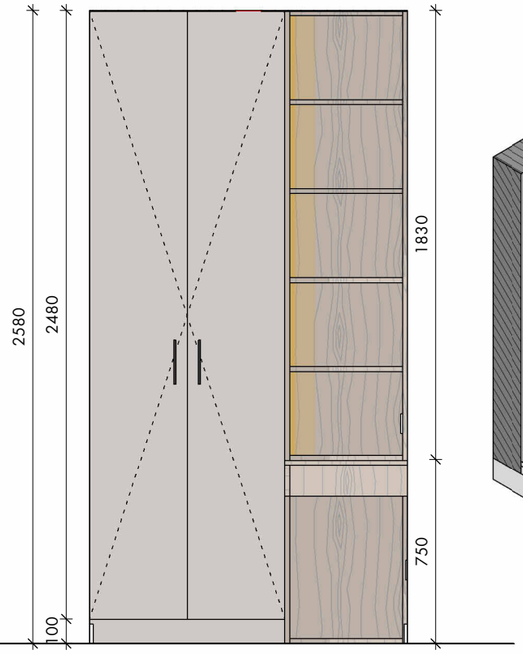

16-13

1 : 25

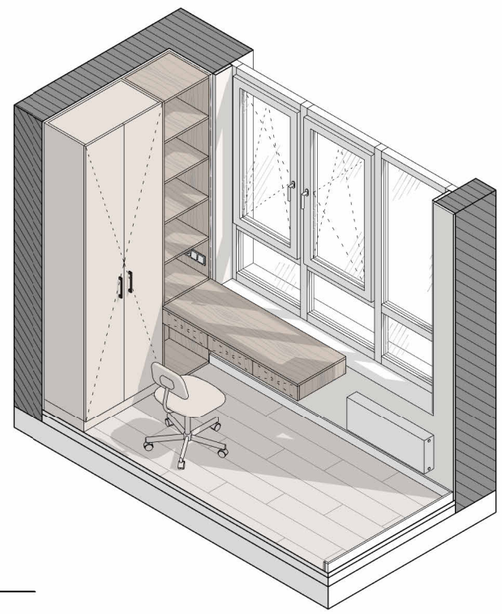

УМОВНІ ПОЗНАЧЕННЯ:

- Вивід 12V
- Вивід 220V
- Вимикач місцевий 1-клавішний
- Вимикач місцевий 2-клавішний
- Вимикач перехресний 1-клавішний
- Вимикач прохідний 1-клавішний
- Домофон
- Майстер вимикач
- Розетка 220V
- Розетка INT
- Терморегулятор

EQ Еквівалентний (рівнозначний) розмір

Напрям розкладки плитки

Оздоблювальні матеріали

ДСП-01	ДСП панелі	4.86 м²
П-01	Плитка 1200x600мм(фартух)	2.70 м²
П-02	Плитка 1200x600мм(санвузол)	18.98 м²
Ф-02	Фарбування	140.82 м²


ПРИМІТКИ:

1. Всі розміри уточнити по місцю.
2. Всі розміри вказані з урахуванням оздоблювальних матеріалів.
3. Всі висоти надані від чистового рівня підлоги.
4. Дивитись аркуш разом з планами сантехніки, електрики, вентиляції та кондиціювання.

SMIRNOVA
INTERIOR DESIGN

Назва проєкту:	Квартира
Адреса проєкту:	вул.Вавілових 11, кв.216

Розгортка балкону
А-42

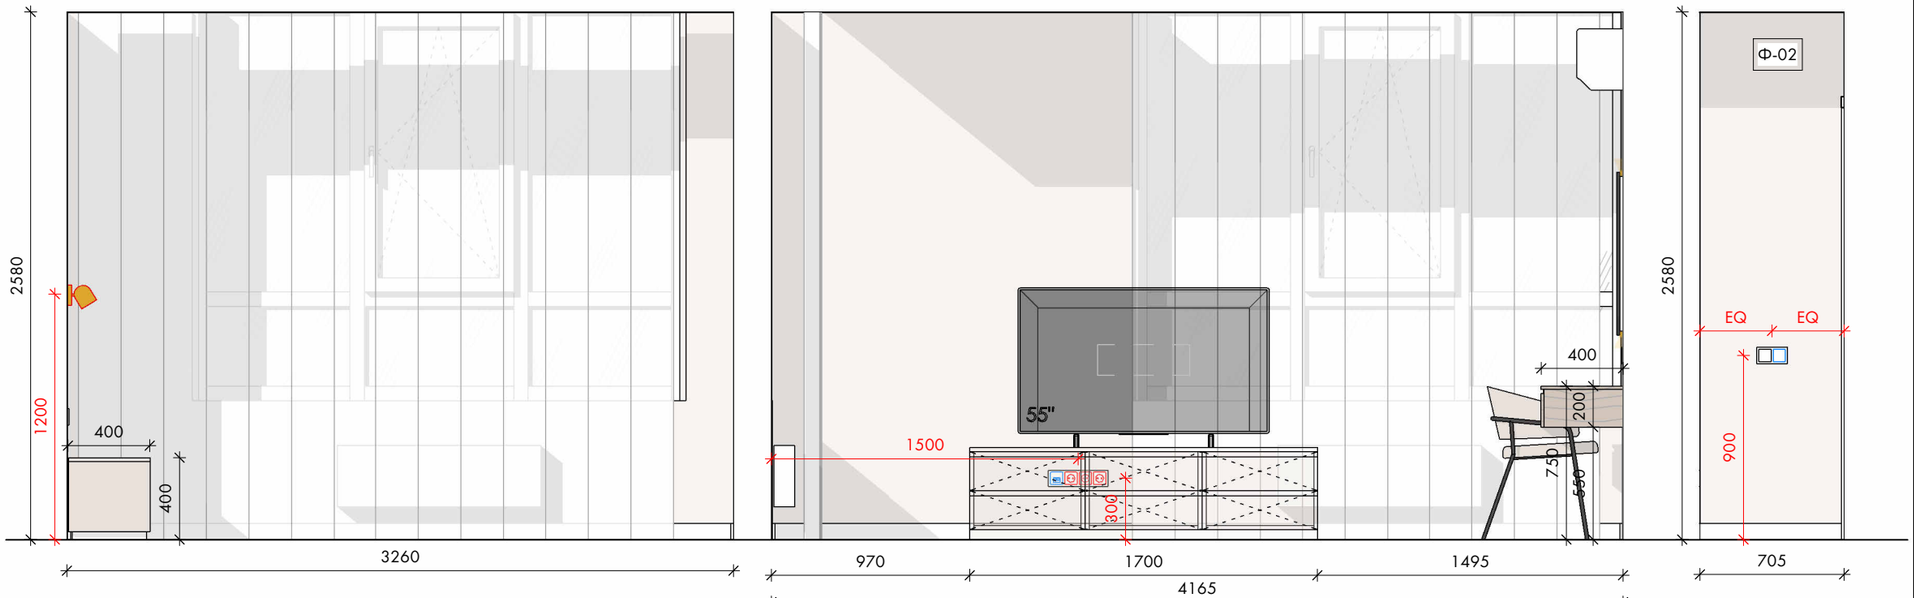

17-18


1 : 30

18-19

1 : 30

20-21

1 : 30

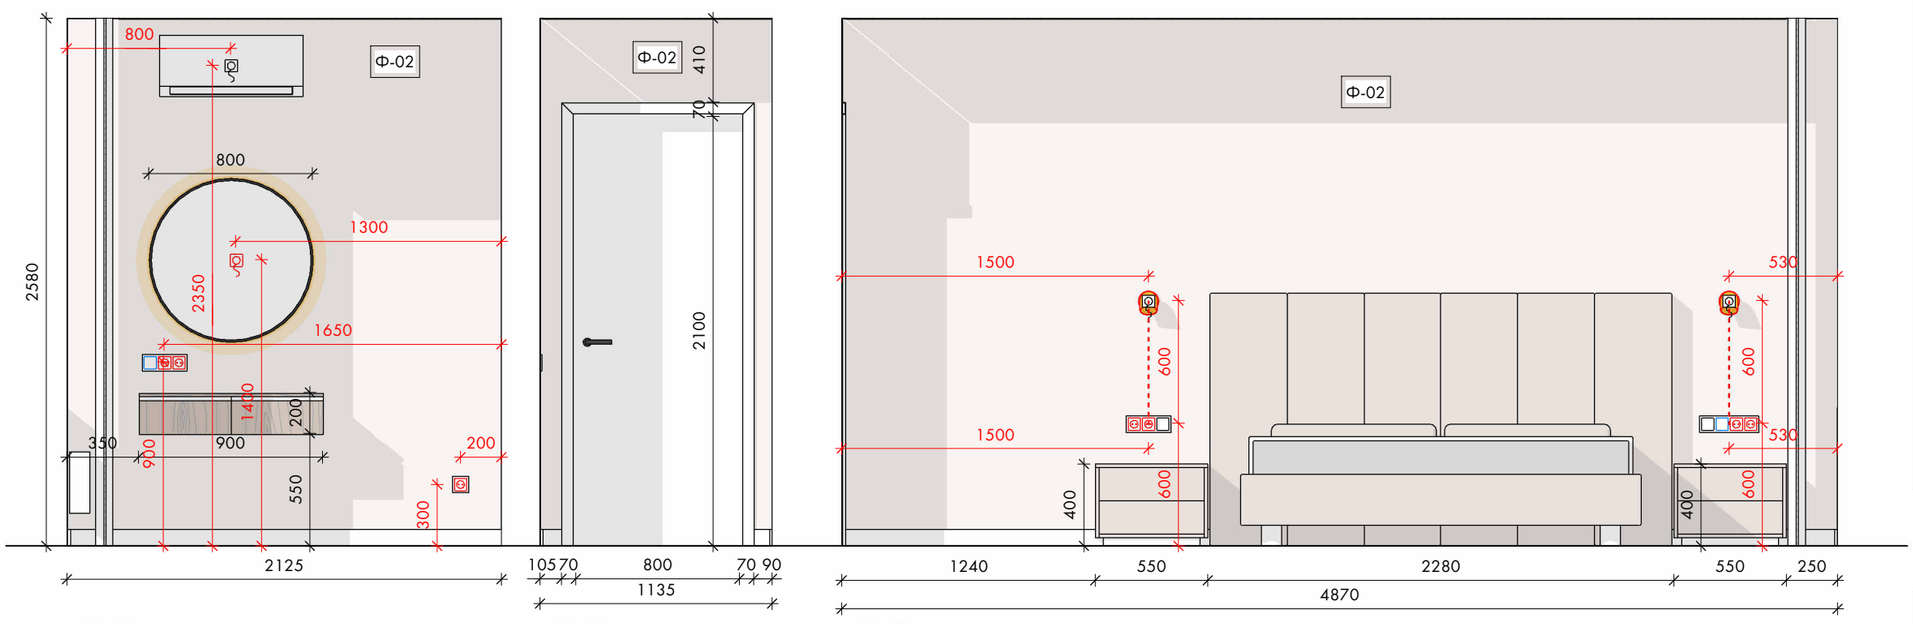

19-20

1 : 30

21-22

1 : 30

22-17


1 : 30

УМОВНІ ПОЗНАЧЕННЯ:

- Вивід 12V
- Вивід 220V
- Вимикач місцевий 1-клавішний
- Вимикач місцевий 2-клавішний
- Вимикач перехресний 1-клавішний
- Вимикач прохідний 1-клавішний
- Домофон
- Майстер вимикач
- Розетка 220V
- Розетка INT
- Терморегулятор

Оздоблювальні матеріали

ДСП-01	ДСП панелі	4.86 м²
П-01	Плитка 1200x600мм(фартух)	2.70 м²
П-02	Плитка 1200x600мм(санвузол)	18.98 м²
Ф-02	Фарбування	140.82 м²

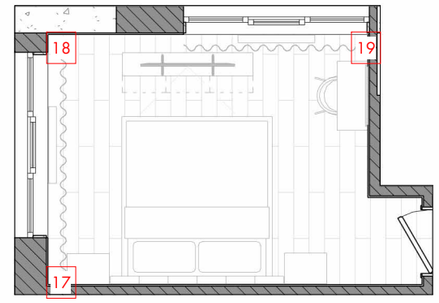

ПРИМІТКИ:

1. Всі розміри уточнити по місцю.
2. Всі розміри вказані з урахуванням оздоблювальних матеріалів.
3. Всі висоти надані від чистового рівня підлоги.
4. Дивитись аркуш разом з планами сантехніки, електрики, вентиляції та кондиціювання.

SMIRNOVA
INTERIOR DESIGN

Назва проєкту:	Квартира
Адреса проєкту:	вул.Вавілових 11, кв.216

Розгортка спальні


А-43



SMIRNOVA
INTERIOR DESIGN


Назва проєкту:	Квартира
Адреса проєкту:	вул.Вавілових 11, кв.216

3D-схема спальні
А-44

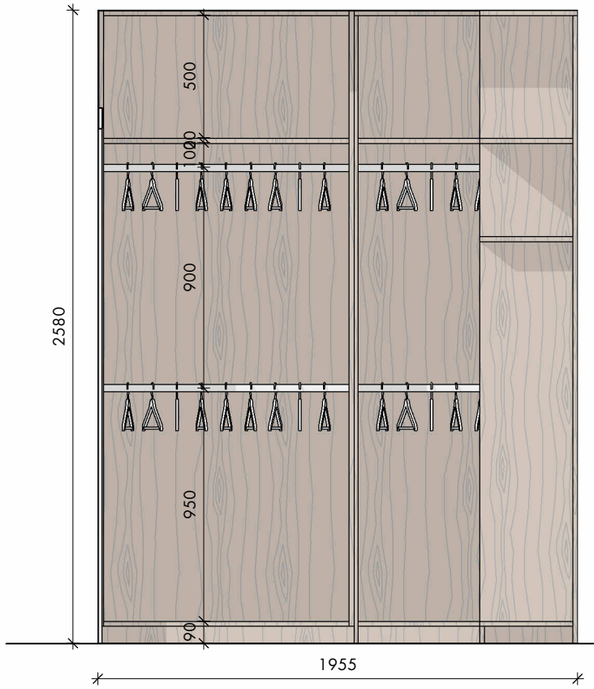


23-24


1 : 25

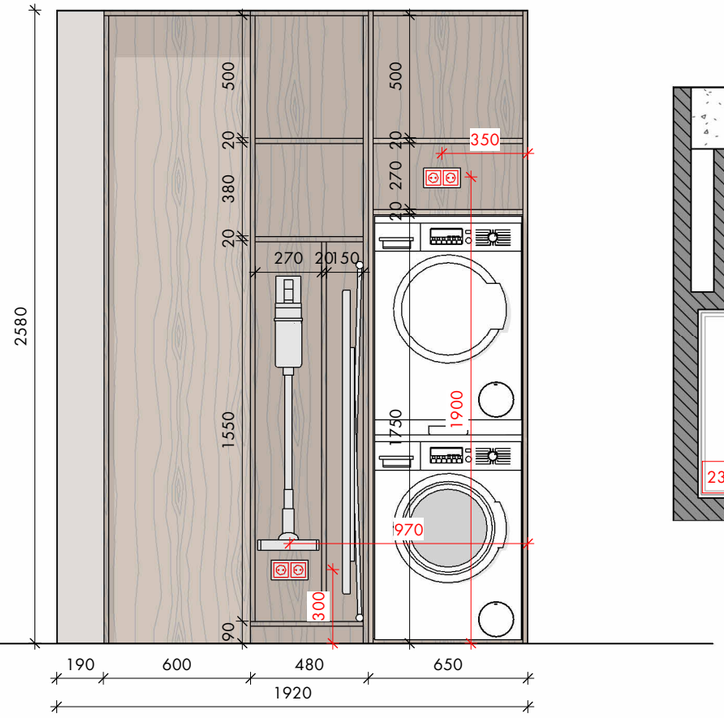

24-25


1 : 25

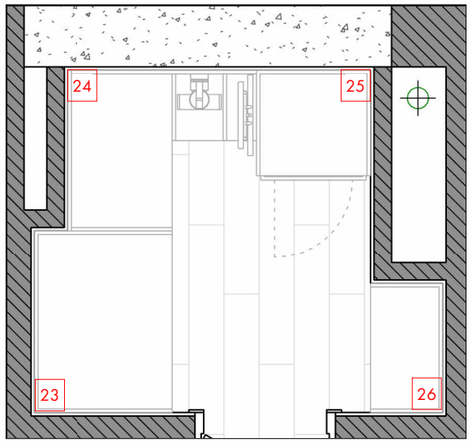

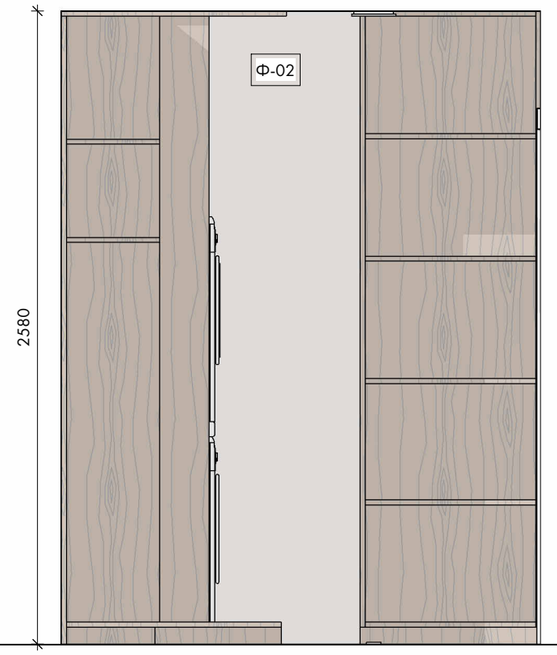


25-26

1 : 25

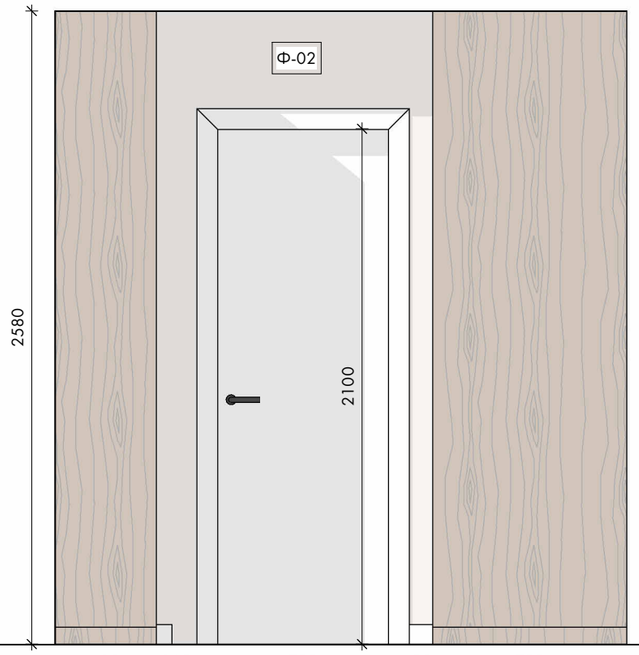

26-23

1 : 25

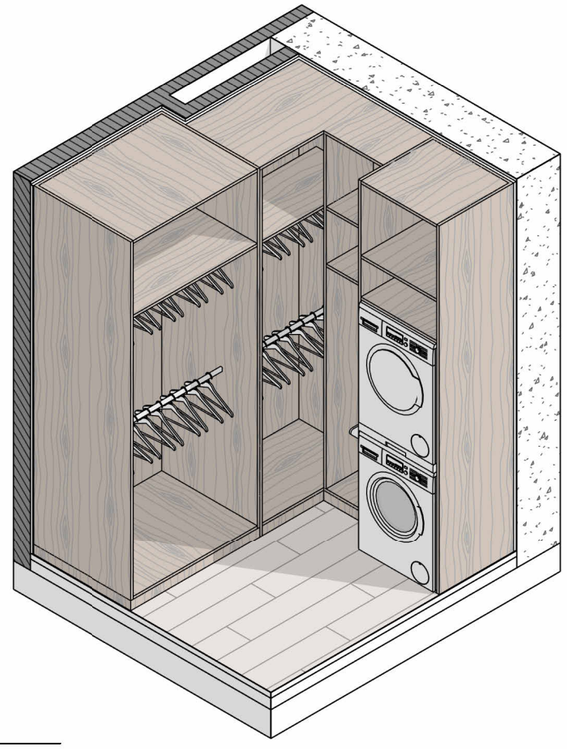

УМОВНІ ПОЗНАЧЕННЯ:

- Вивід 12V
- Вивід 220V
- Вимикач місцевий 1-клавішний
- Вимикач місцевий 2-клавішний
- Вимикач перехресний 1-клавішний
- Вимикач прохідний 1-клавішний
- Домофон
- Майстер вимикач
- Розетка 220V
- Розетка INT
- Терморегулятор

EQ Еквівалентний (рівнозначний) розмір

Напрям розкладки плитки

Оздоблювальні матеріали

ДСП-01	ДСП панелі	4.86 м²
П-01	Плитка 1200x600мм(фартух)	2.70 м²
П-02	Плитка 1200x600мм(санвузол)	18.98 м²
Ф-02	Фарбування	140.82 м²


ПРИМІТКИ:


1. Всі розміри уточнити по місцю.
2. Всі розміри вказані з урахуванням оздоблювальних матеріалів.
3. Всі висоти надані від чистового рівня підлоги.
4. Дивитись аркуш разом з планами сантехніки, електрики, вентиляції та кондиціювання.


SMIRNOVA
INTERIOR DESIGN

Назва проєкту:	Квартира
Адреса проєкту:	вул.Вавілових 11, кв.216

Розгортка гардеробу
А-45

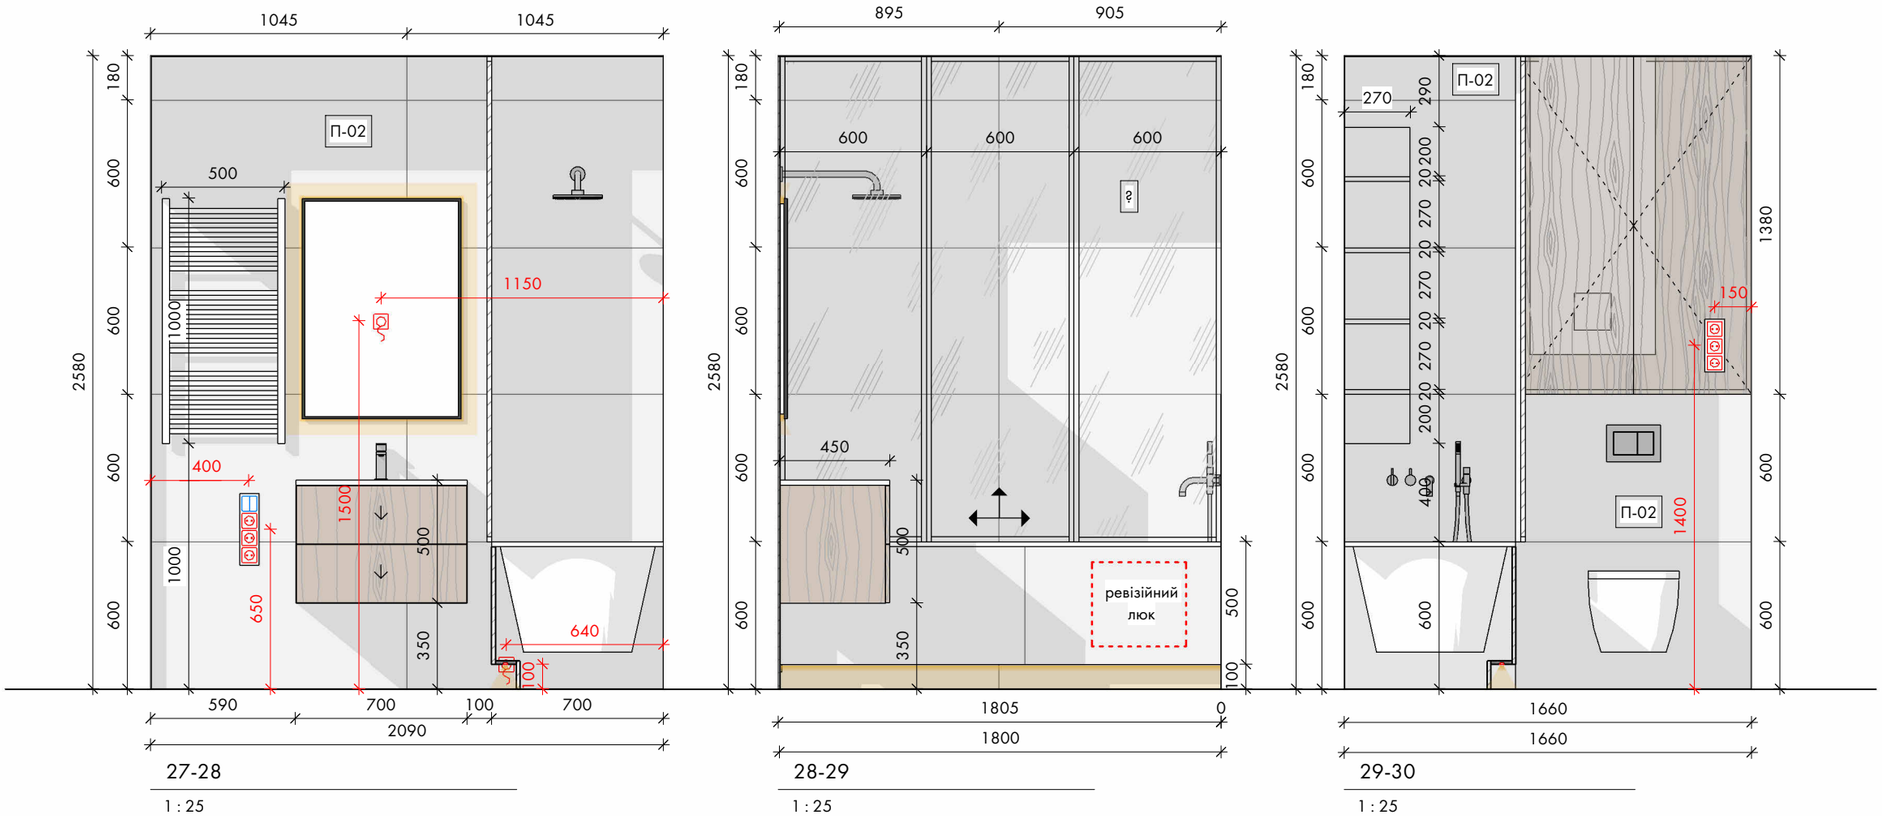

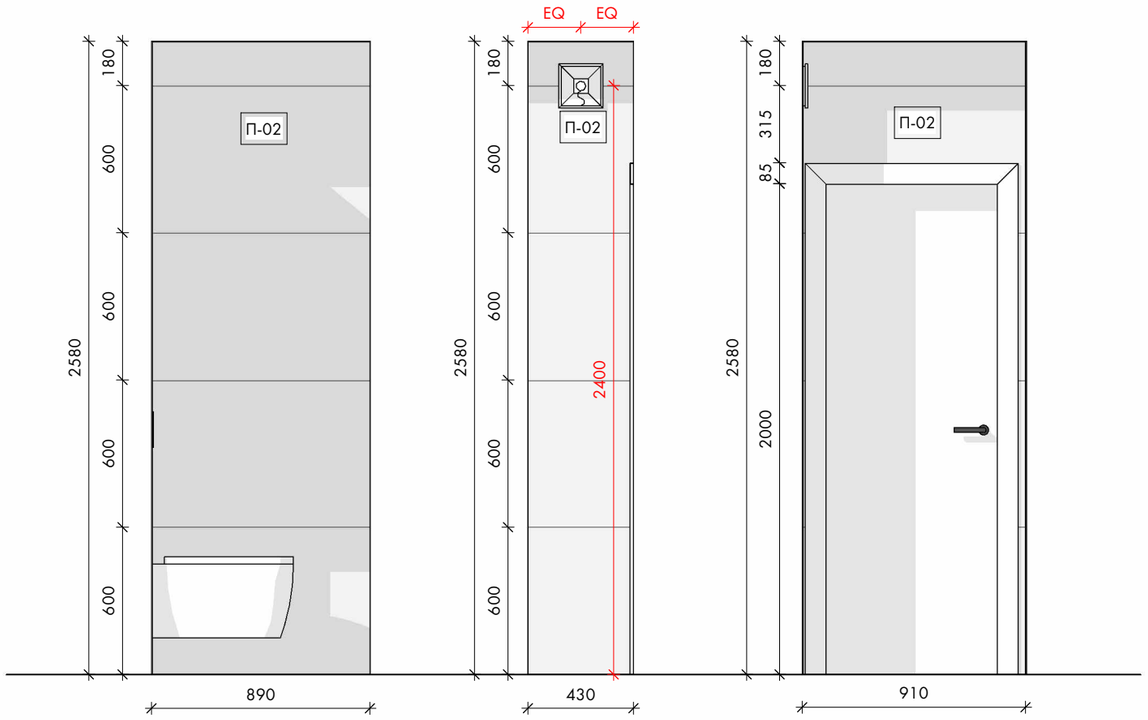

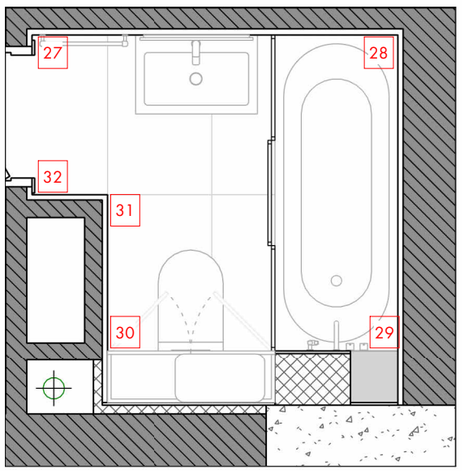

УМОВНІ ПОЗНАЧЕННЯ:

- Вивід 12V
- Вивід 220V
- Вимикач місцевий 1-клавішний
- Вимикач місцевий 2-клавішний
- Вимикач перехресний 1-клавішний
- Вимикач прохідний 1-клавішний
- Домофон
- Майстер вимикач
- Розетка 220V
- Розетка INT
- Терморегулятор

EQ Еквівалентний (рівнозначний) розмір

Напрям розкладки плитки

Оздоблювальні матеріали

ДСП-01	ДСП панелі	4.86 м²
П-01	Плитка 1200x600мм(фартух)	2.70 м²
П-02	Плитка 1200x600мм(санвузол)	18.98 м²
Ф-02	Фарбування	140.82 м²

ПРИМІТКИ:


1. Всі розміри уточнити по місцю.
2. Всі розміри вказані з урахуванням оздоблювальних матеріалів.
3. Всі висоти надані від чистового рівня підлоги.
4. Дивитись аркуш разом з планами сантехніки, електрики, вентиляції та кондиціювання.


SMIRNOVA
INTERIOR DESIGN

Назва проєкту:	Квартира
Адреса проєкту:	вул.Вавілових 11, кв.216

Розгортка санвузла

А-46

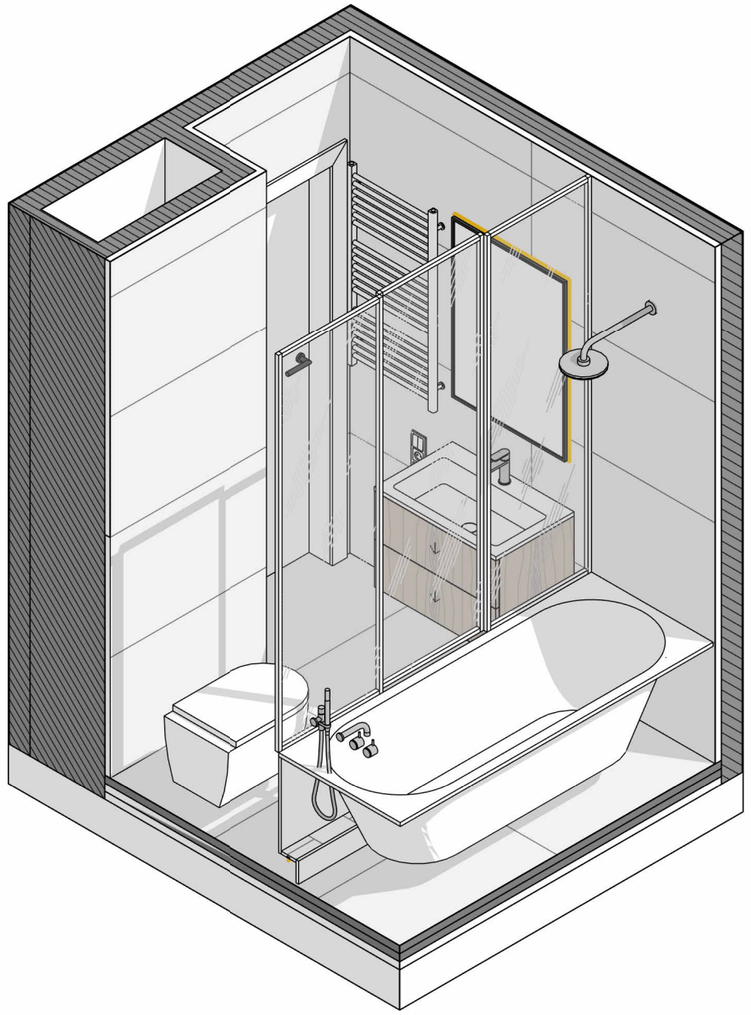

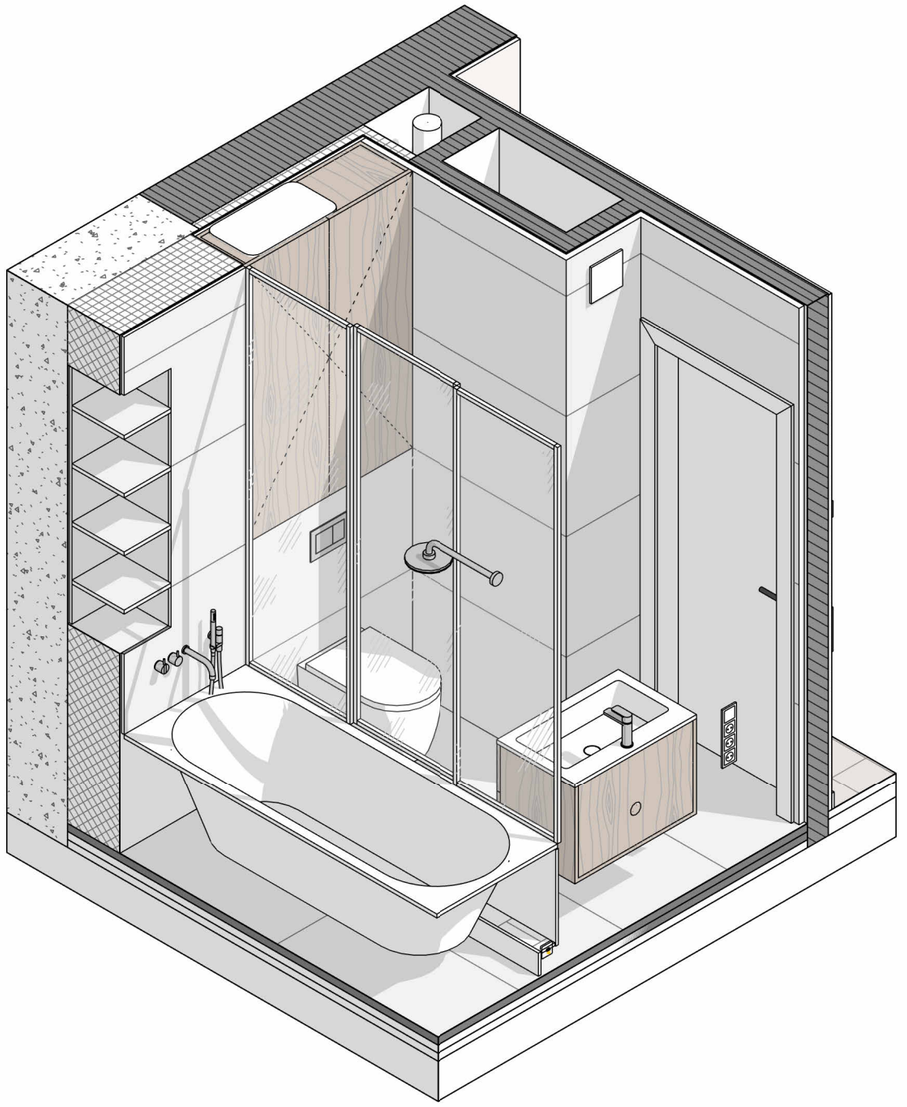

SMIRNOVA
INTERIOR DESIGN

Назва проєкту:	Квартира
Адреса проєкту:	вул.Вавілових 11, кв.216

3D-схема санвузла
А-47